


HQ - Sea Point
P r e f e r r e d

HQ - Sea Point
P r e f e r r e d

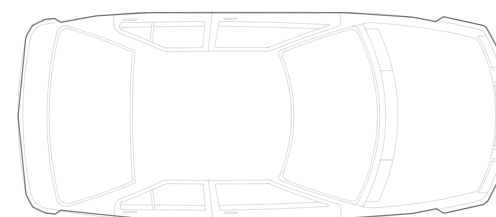

MAIN ROAD

stud.

No bull, just beef.

stud.
THE BURGER SHOP
9 SEA POINT

ORDER & PAY



www.studtheburgershop.co.za
& @stud_the_burger_shop

COLLECT

stud.
THE BURGER SHOP

The Jnr. Burger just
The No Bull Burger just
The Hybrid Burger just
Drop in Deal - On your way
Copy Meal just a bun, but

No cash, just card, or

H.o.
Wine
Beer
Stud City

10.50
10.50
10.50
10.50


just beef.



Stud.

HQ - Sea Point
P r e f e r r e d

Equipment Layout

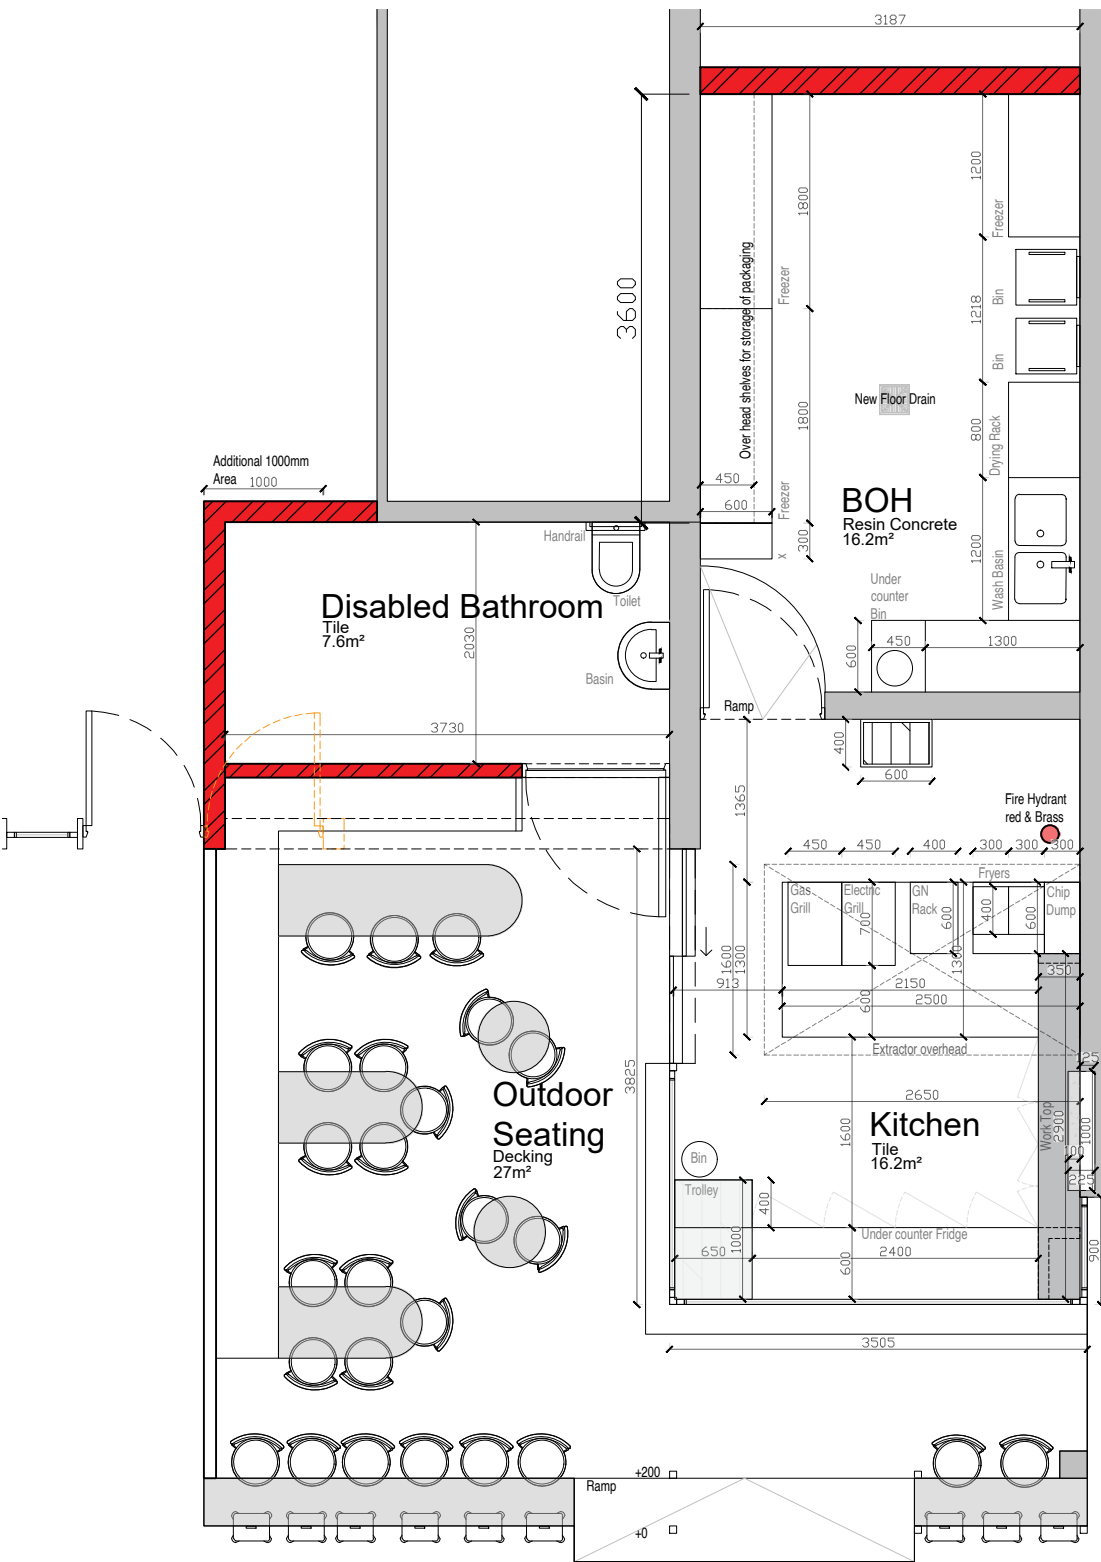

Under counter Fridge

Extractor

Fryers

Chip Dump

Trolley

Trolley #2

Seating


Seating

Table

 Resin Concrete

 Tile

 Balau Decking 19x90mm

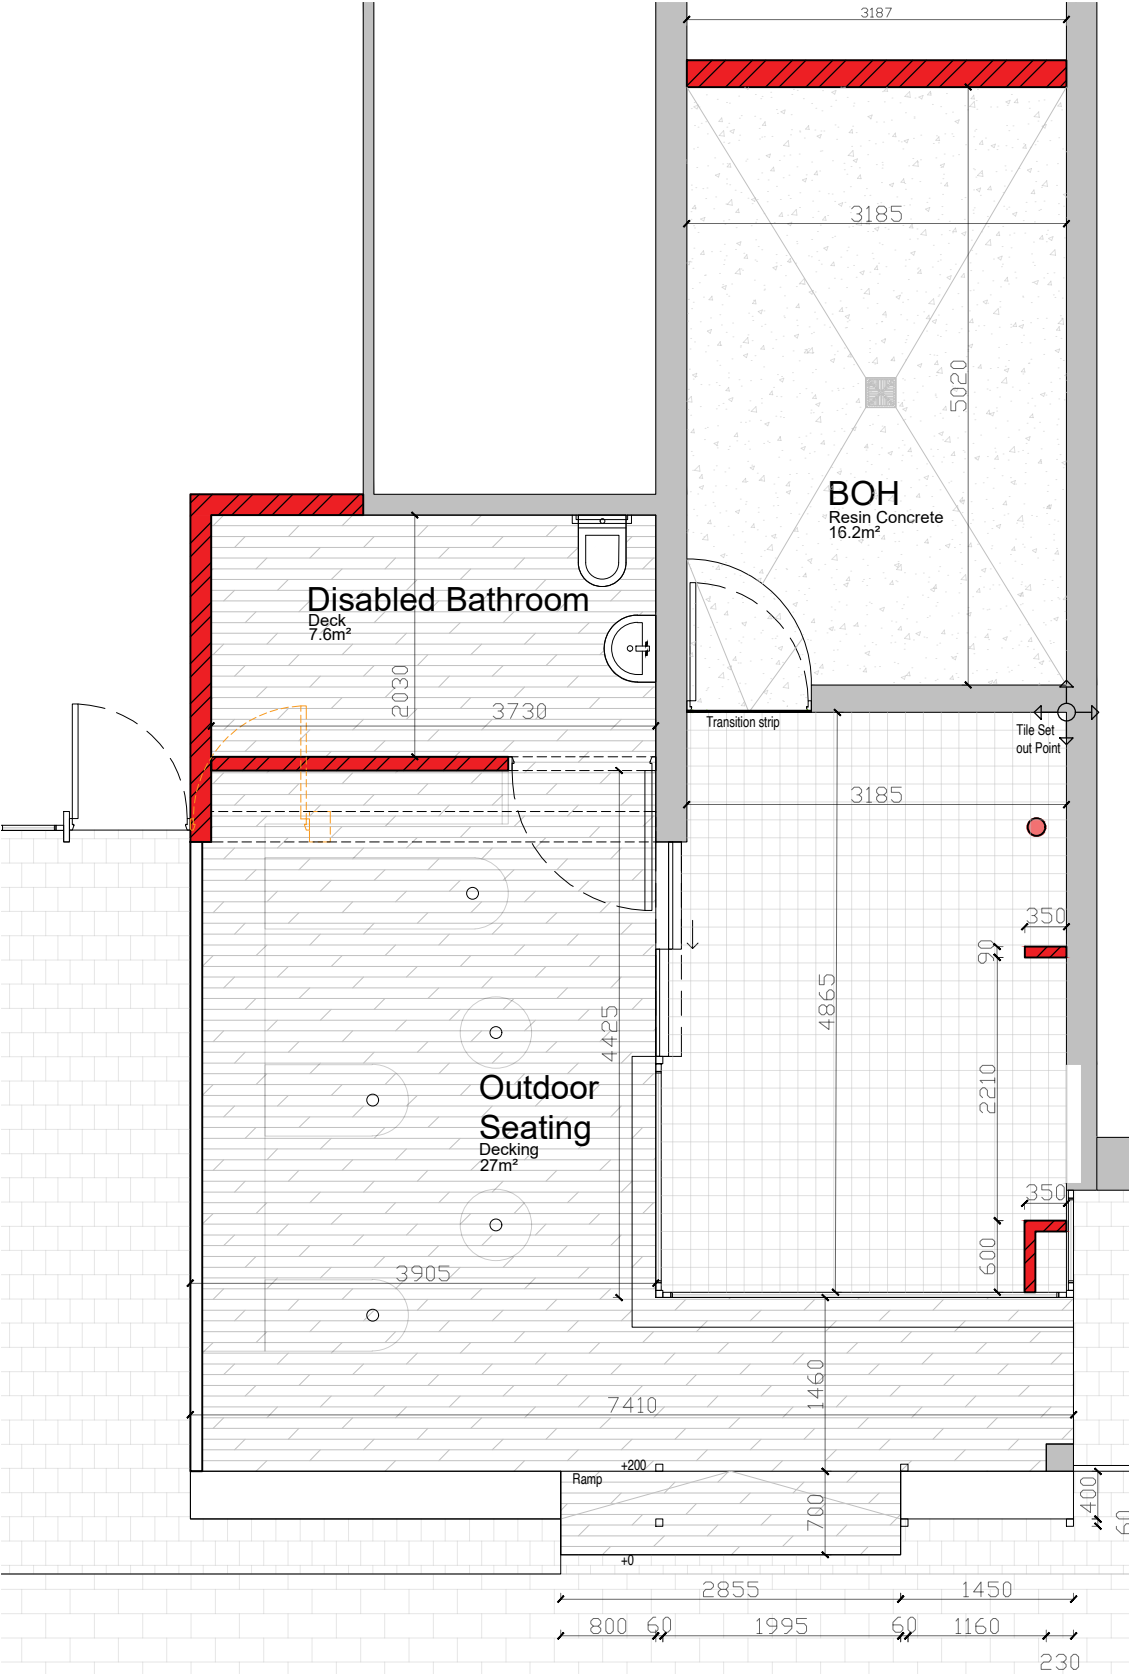

MAIN ROAD


Stud.

HQ - Sea Point
P r e f e r r e d

Lighting Legend



LED White

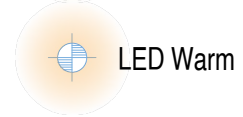


LED Warm

LED Strip Lighting



Light switch
@ 1000mm Form FFL

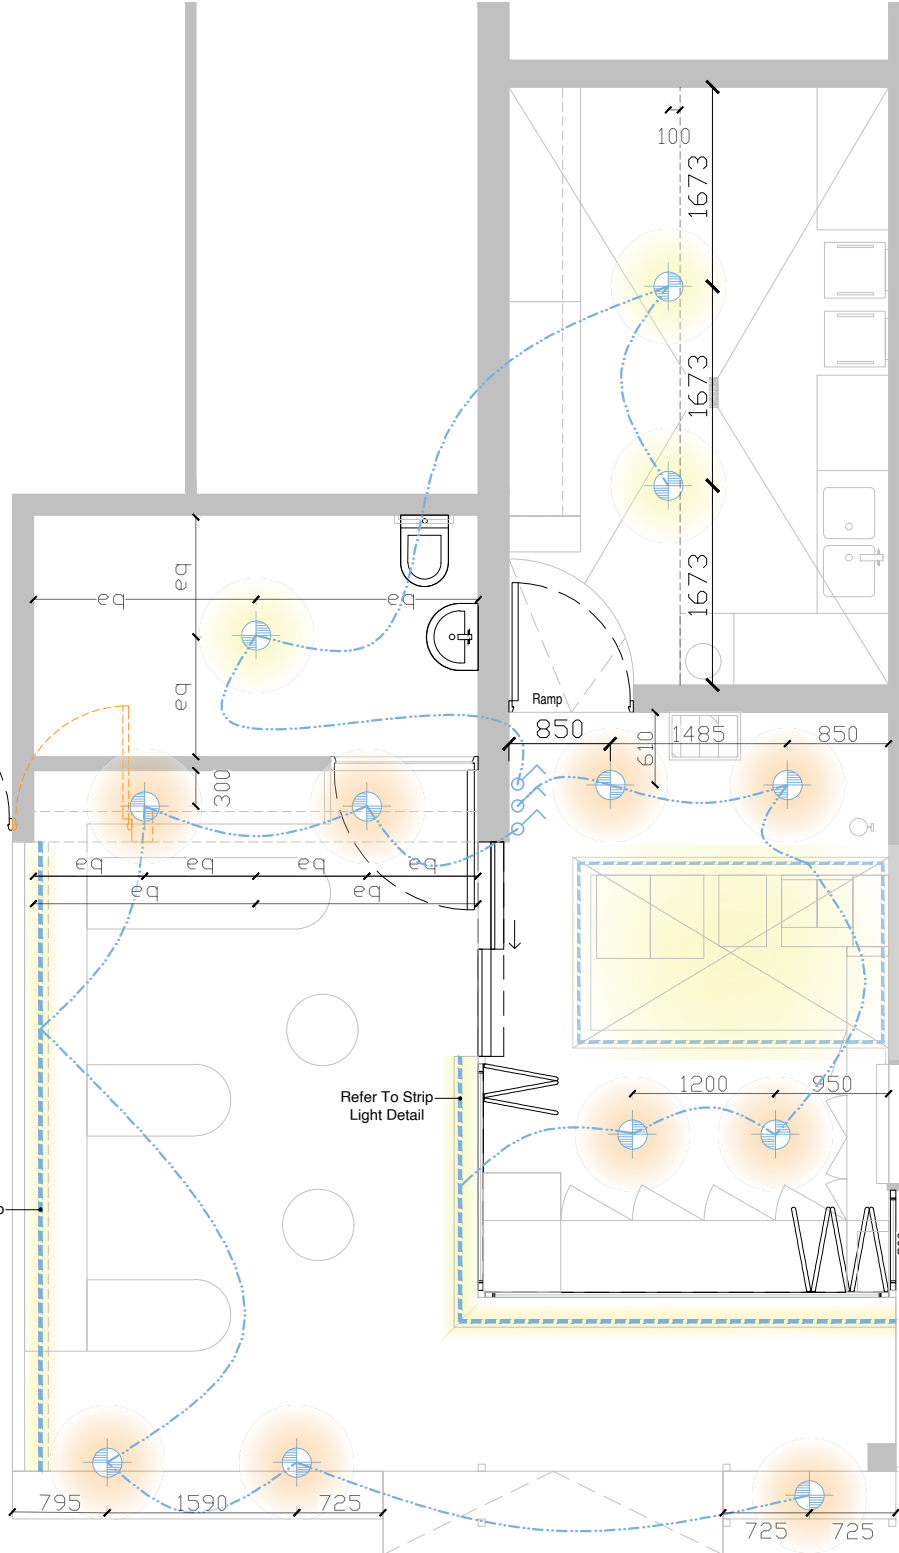


Refer To Strip
Light Detail

Refer To Strip
Light Detail

LIGHTING LAYOUT

SCALE N.T.S

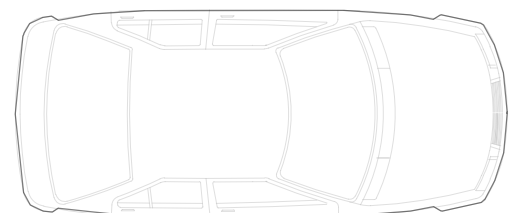


M A I N R O A D

Stud.

HQ - Sea Point
P r e f e r r e d


Plumbing Legend

-  Geyser
-  Hot water
-  Cold water
-  Tap
-  Hot water pipe
-  Cold water pipe
-  Drainage pipe

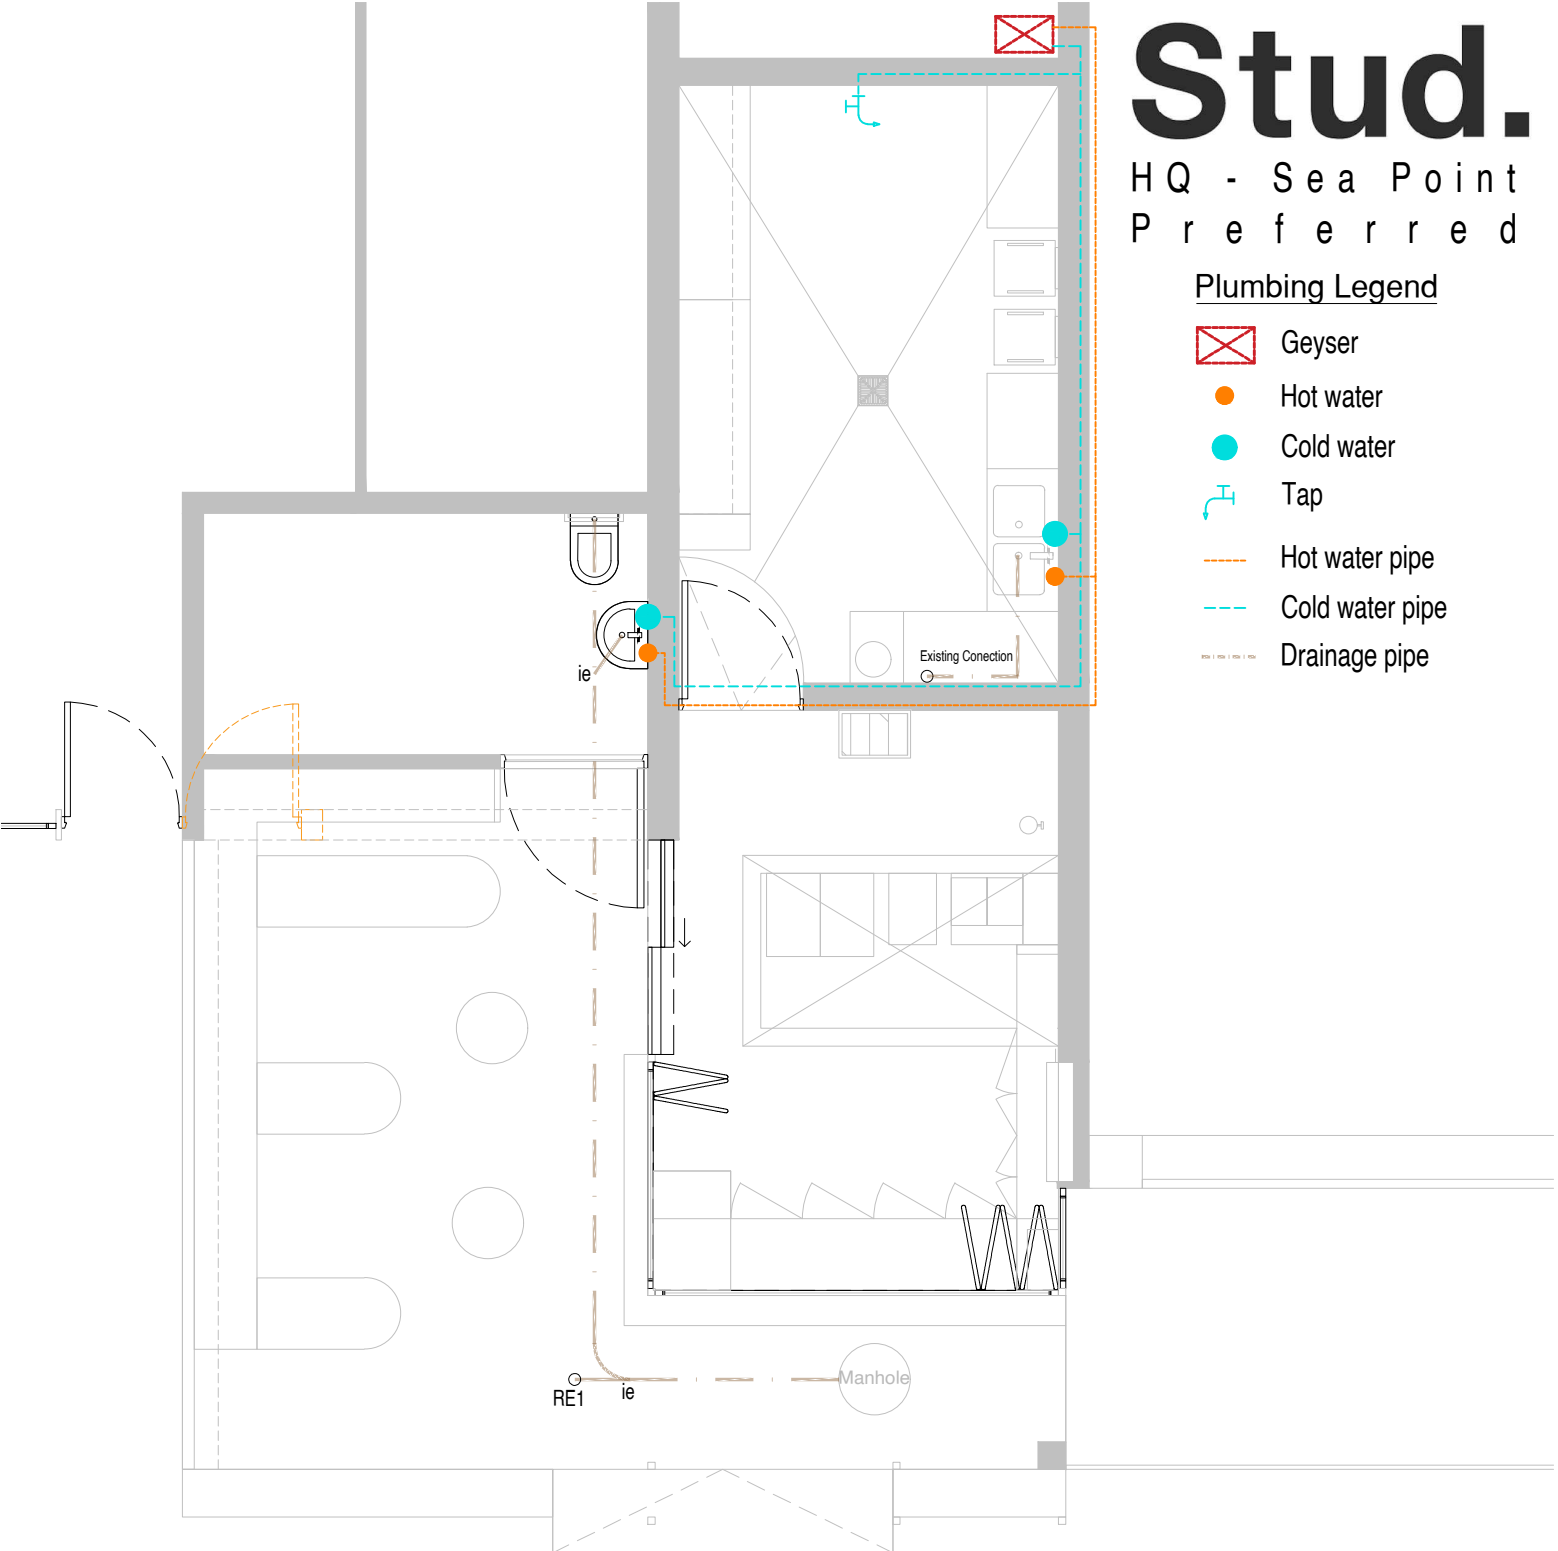

PLUMBING LAYOUT

SCALE: N.T.S

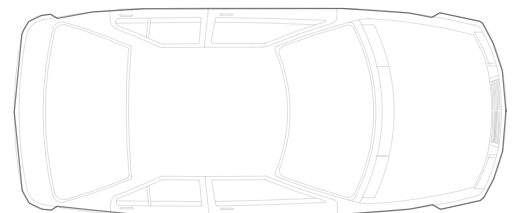

M A I N R O A D

HQ - Sea Point
P r e f e r r e d

-New wall tile.
Cover area: Floor to ceiling

-New wall tile.
Cover area: Floor to ceiling



MAIN ROAD