


1. Contractor to verify all levels, heights and site dimensions before putting any work to hand;
2. any discrepancies to be reported to the architect immediately for clarification;
3. this drawing is not to be scaled - figured dimensions are to be used at all times;
4. all work to be carried out in strict accordance with local authorities requirements, National Building Regulations SANS 10400 and other relevant SANS standards.
5. This drawing is to be read in conjunction with all relevant consultants drawings, details and specifications.
6. All shop drawings are to be submitted for Architects approval prior to manufacture or installation.
7. Only the latest revision is to be used.
8. All dimensions are given in millimeters.
9. The Architect accepts no responsibility for errors resulting from the misinterpretation of this drawing.

© COPYRIGHT:

Please note that the copyright of the literary works, artistic works and published editions contained herein is vested with the JV Architects. Any adaptation, distribution, sale or hire for, or any form of reproduction of these works, in any part or in their entirety, by any party other than the JV Architects is an infringement of this copyright, and the JV Architects reserves the right to claim damages from any party infringing this copyright, unless these rights are varied in writing.


REV	DATE	DESCRIPTION
A	2025.08.28	Deliverable 14

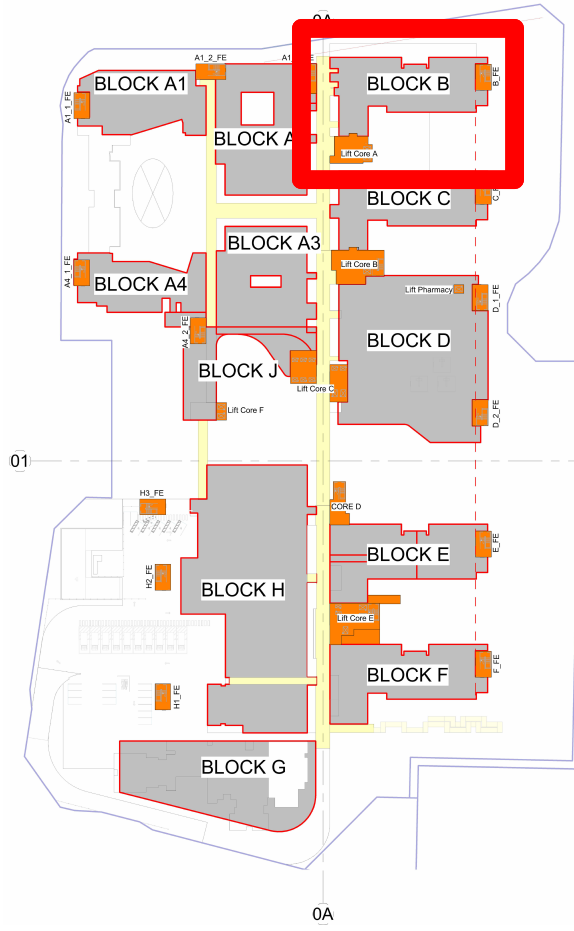

1 4 Level 4 ffl ORTHOPAEDICS 2
SCALE = 1 : 200



2 4 Level 4 ffl ORTHOPAEDICS 2 Cut @ 50 above FFL
SCALE = 1 : 200

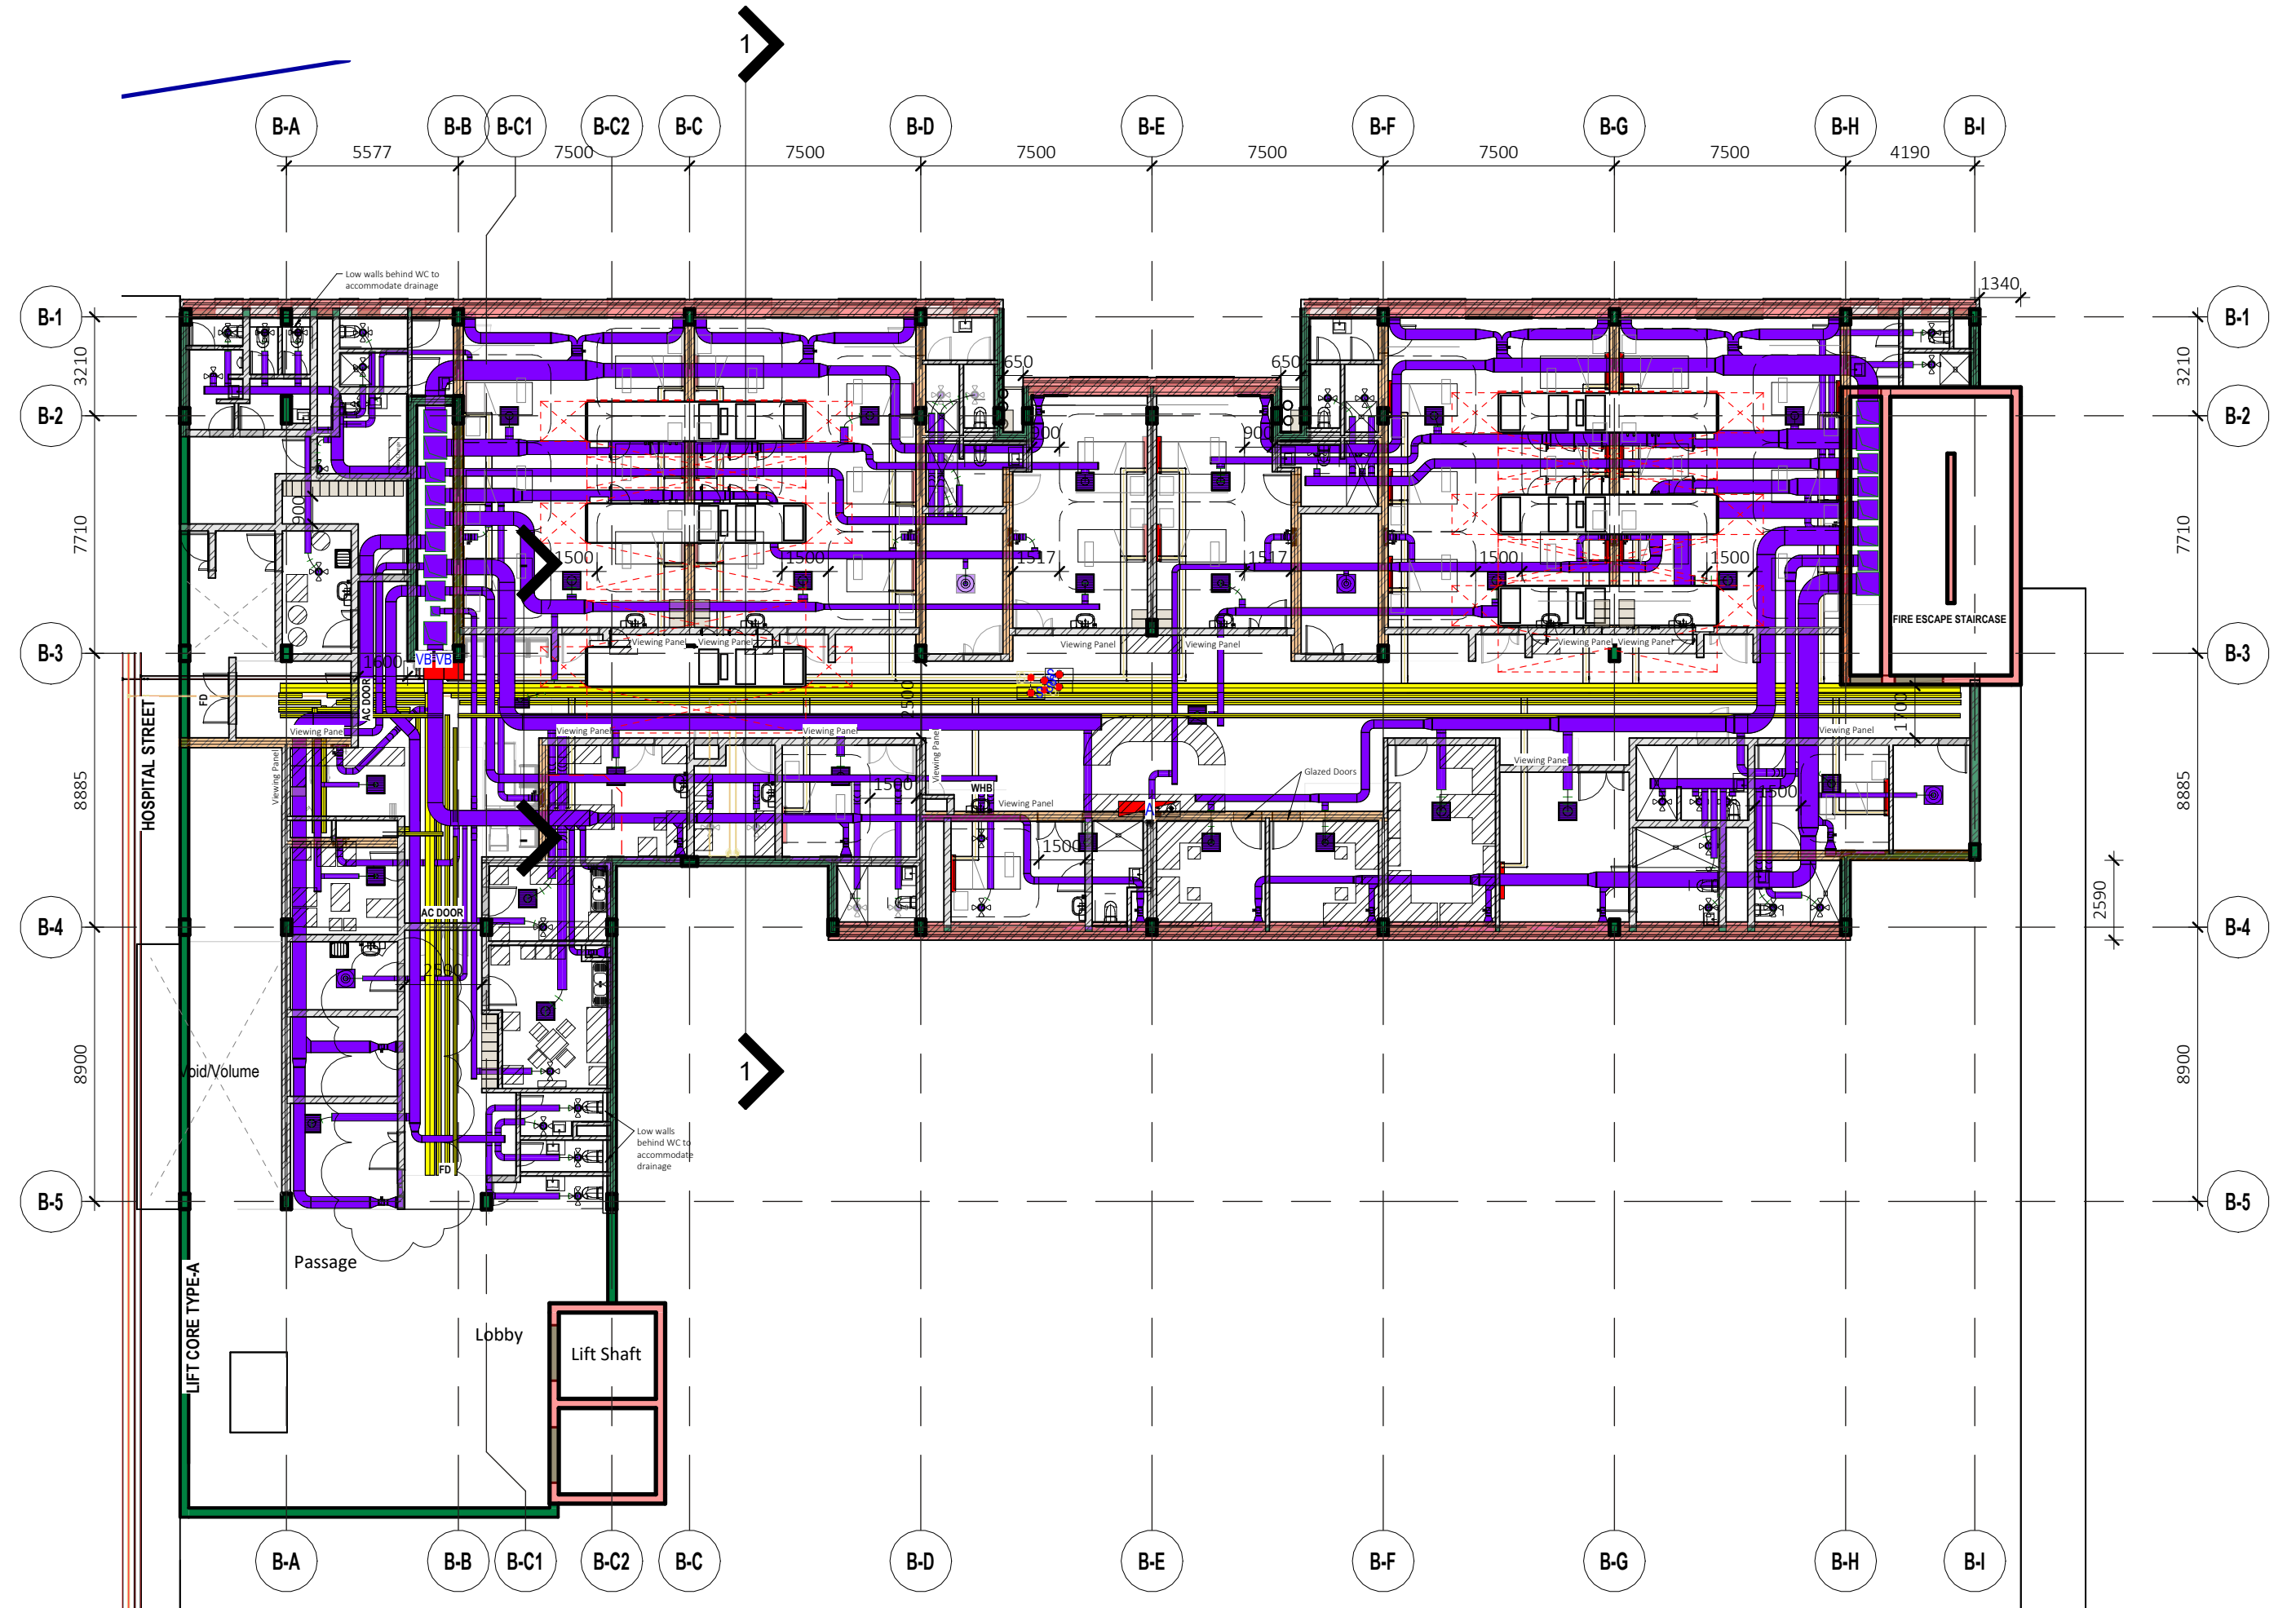

3 4 Level 4 ffl ORTHOPAEDICS 2 Cut @ 3700 above FFL
SCALE = 1 : 200

CLIENT:
WESTERN CAPE GOVERNMENT INFRASTRUCTURE

PROJECT:
BELHAR HOSPITAL



DRAWING:
4 Level 4 ffl ORTHOPAEDICS 2 _Coordination

SCALE:
1 : 200

DATE:
12/11/25

DRAWN:
BB

CHECKED:
AA

DRAWING NUMBER:
CI840025 - ARC - FL - B - DR - ARC - 1210.9

REV:
A




THIRTYTHREE 18
JOINT VENTURE

Tel: +27 (0) 21 419-7760 | Email: studio@ehharch.com
Unit G8, Victoria Junction, 56 Prestwich Street, De Waterkant, Cape Town, 8001.

DRAWING STATUS:


FOR INFORMATION

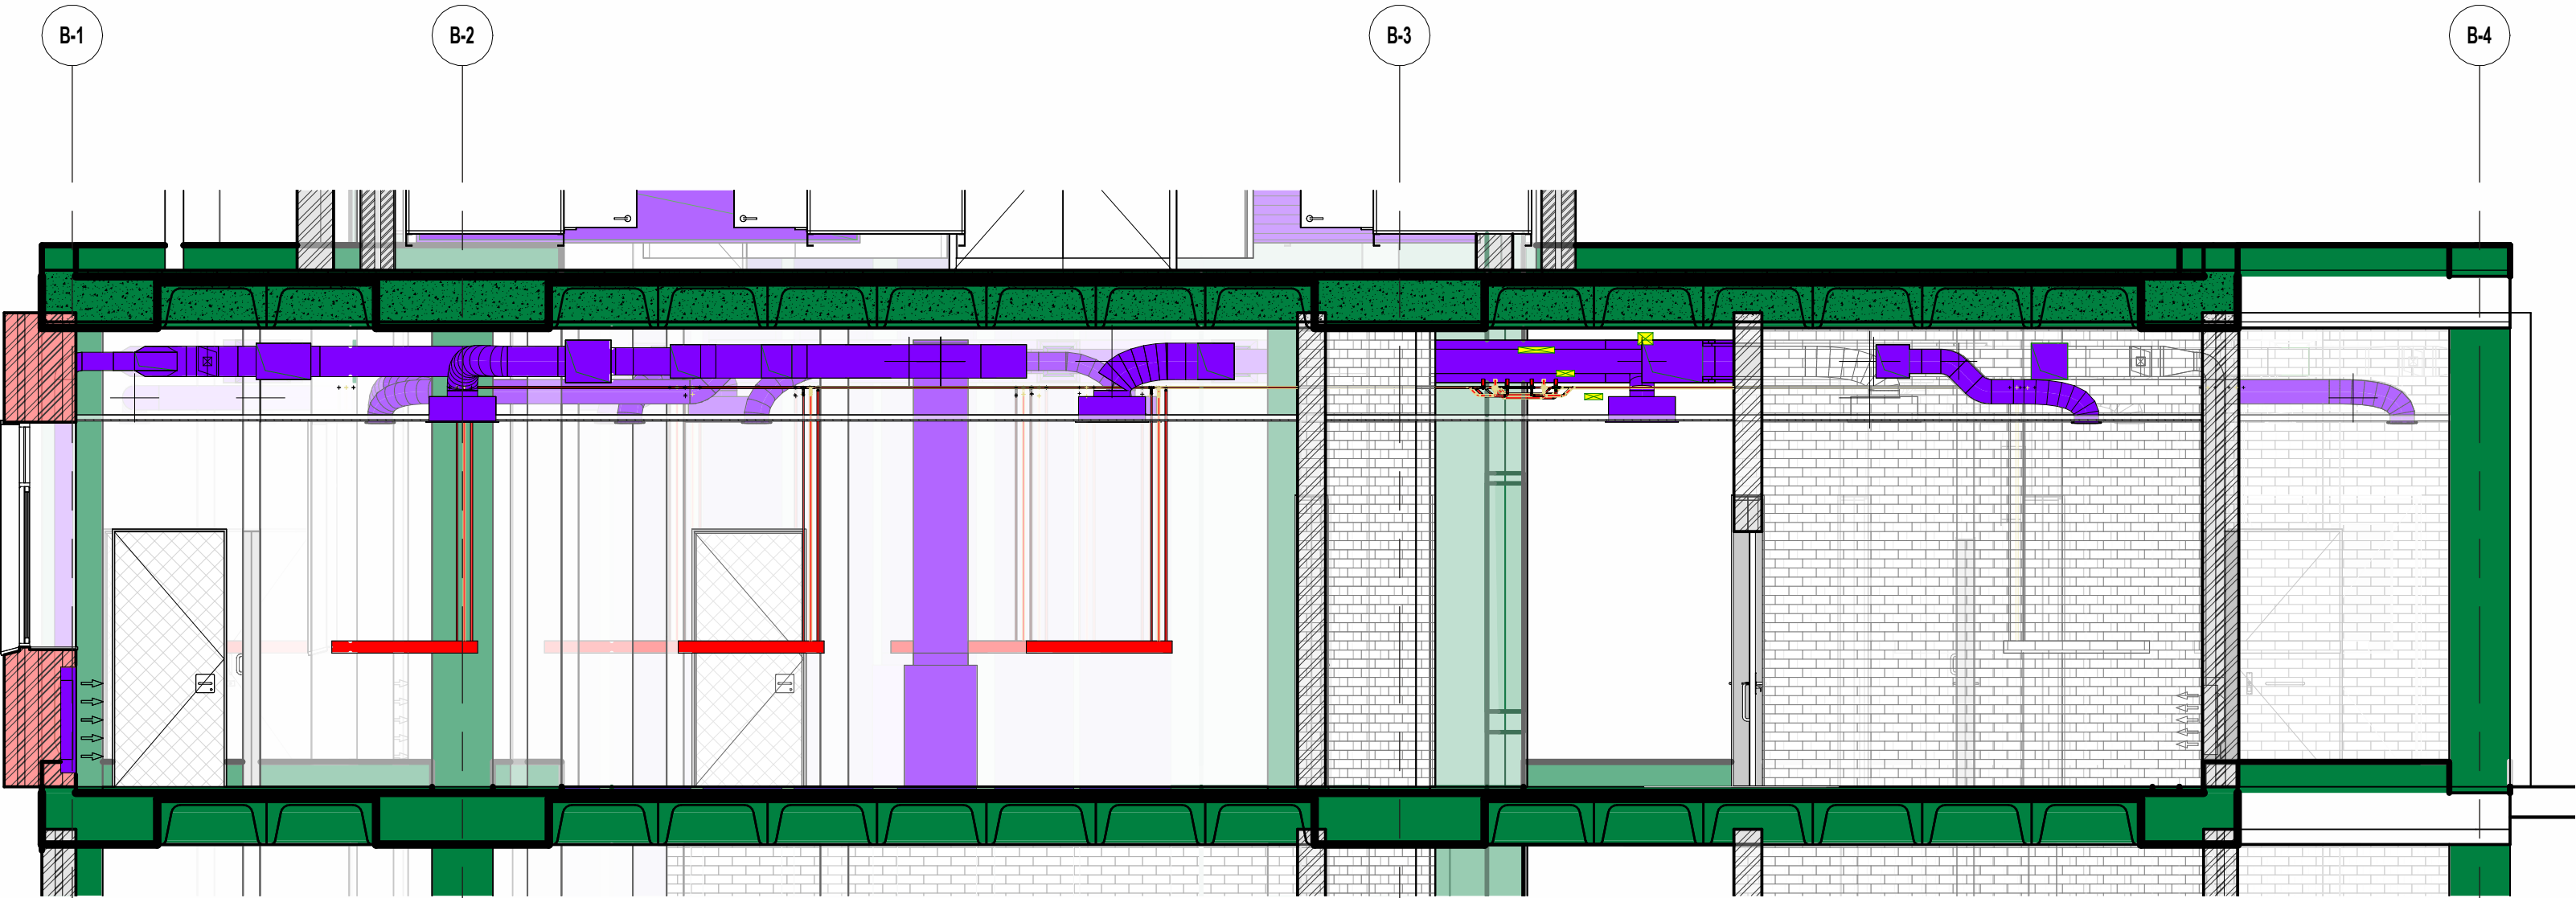


Section 31




2 Bed Ward _ Coordination

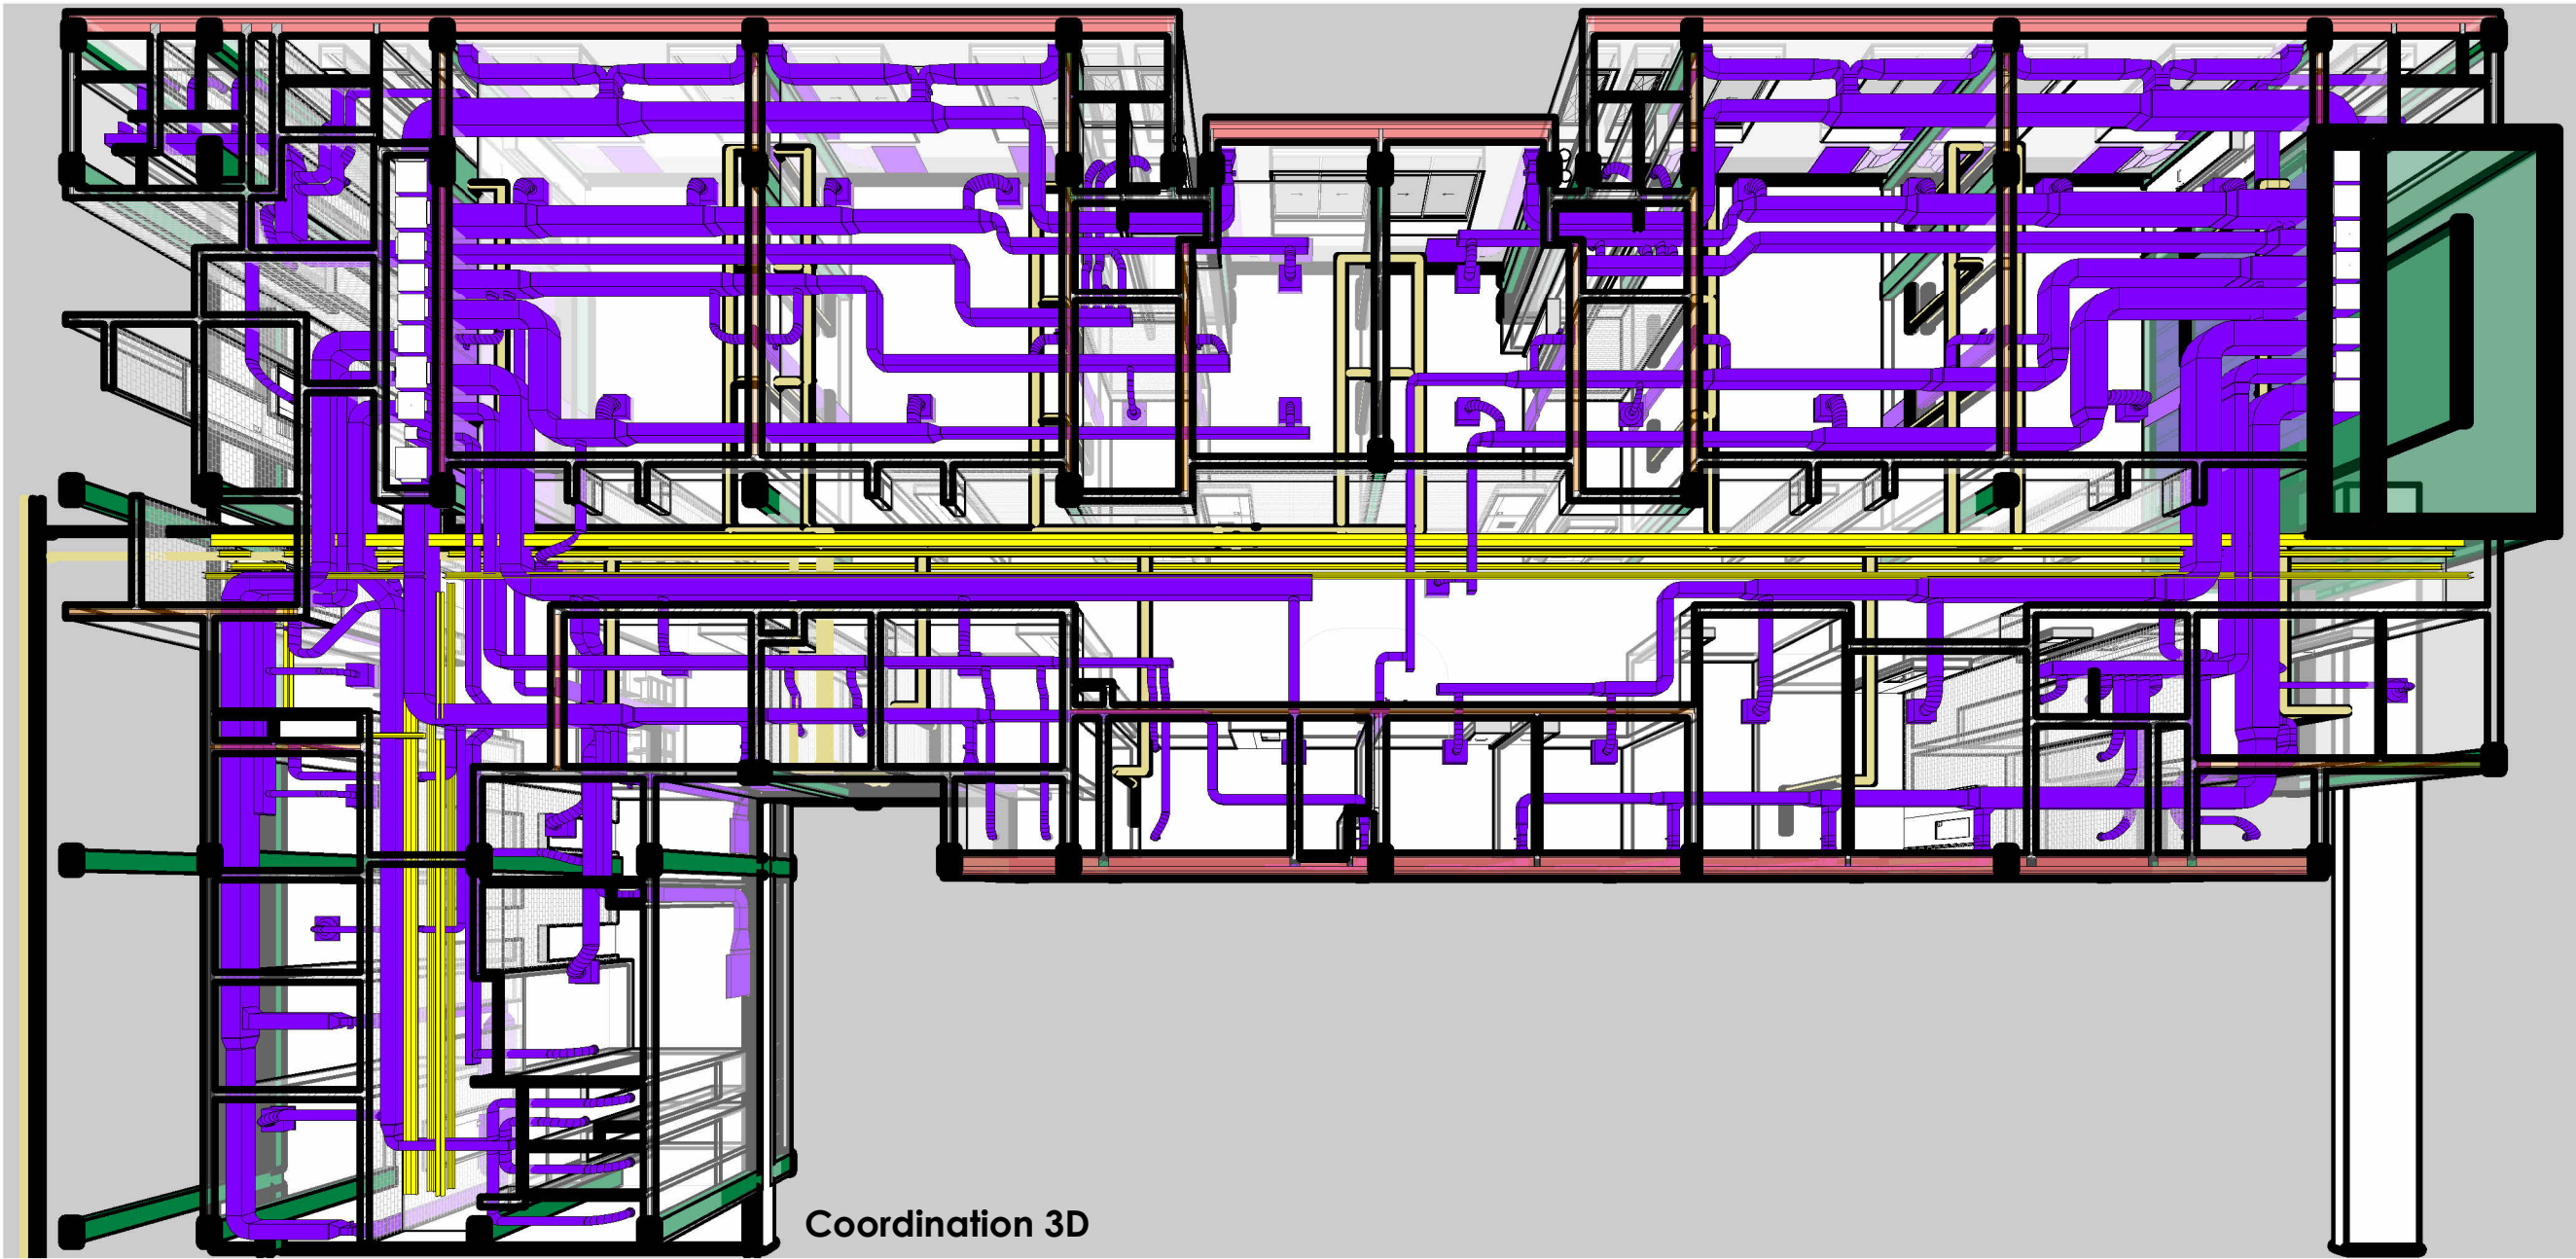

Coordination 3D

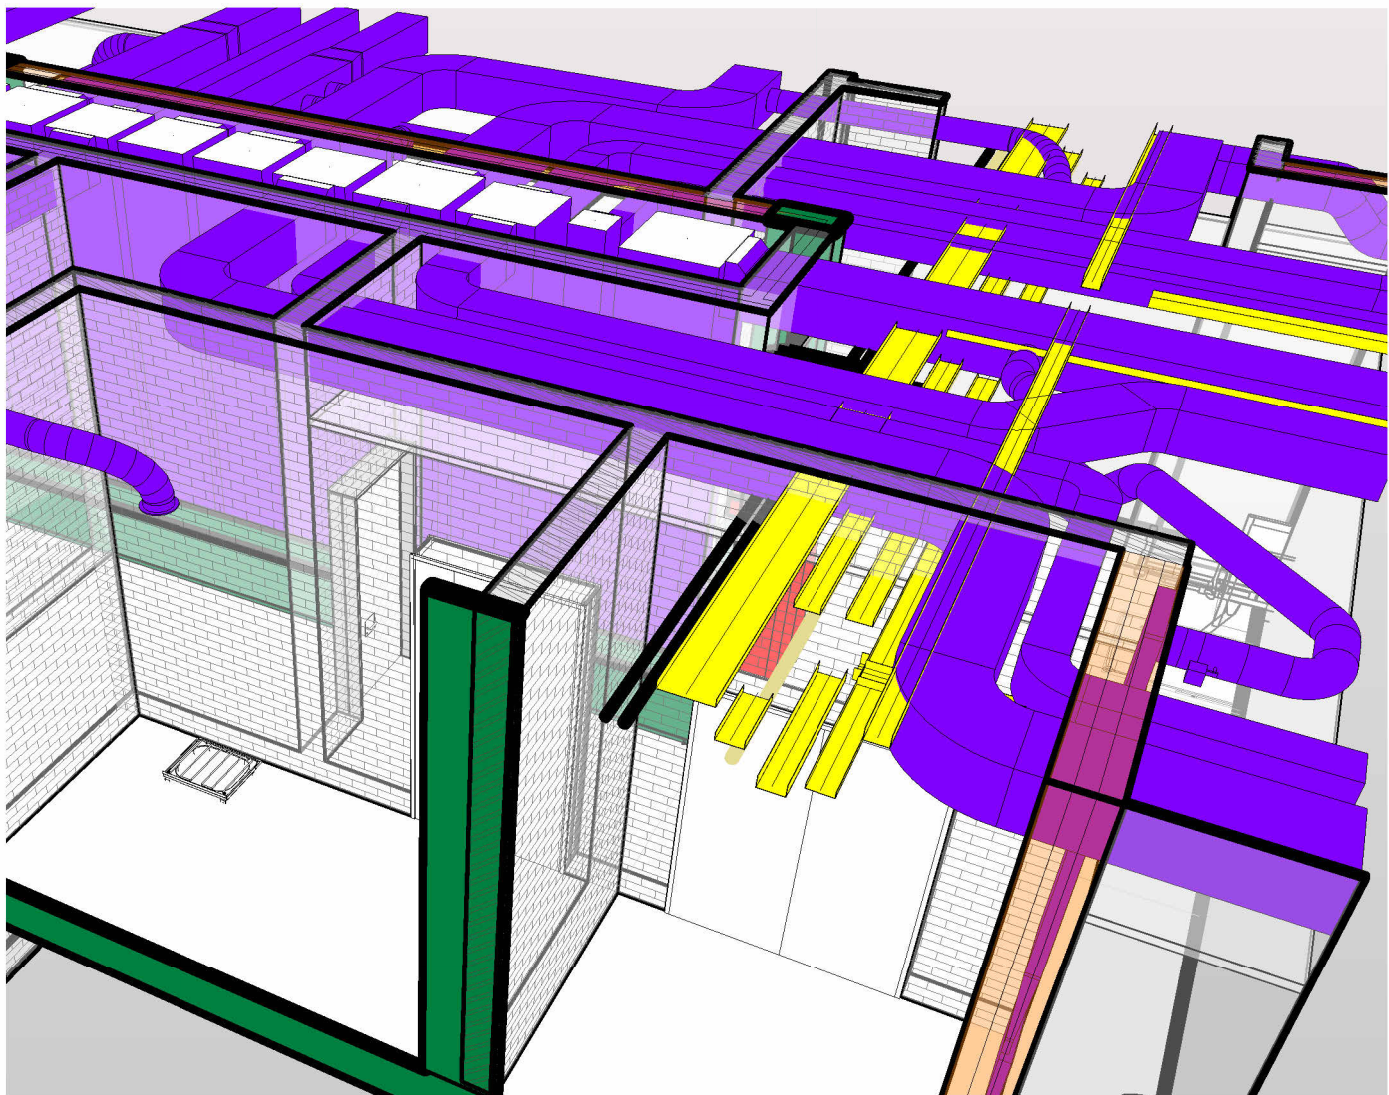

Ward Passage Ceiling Void _Coordination

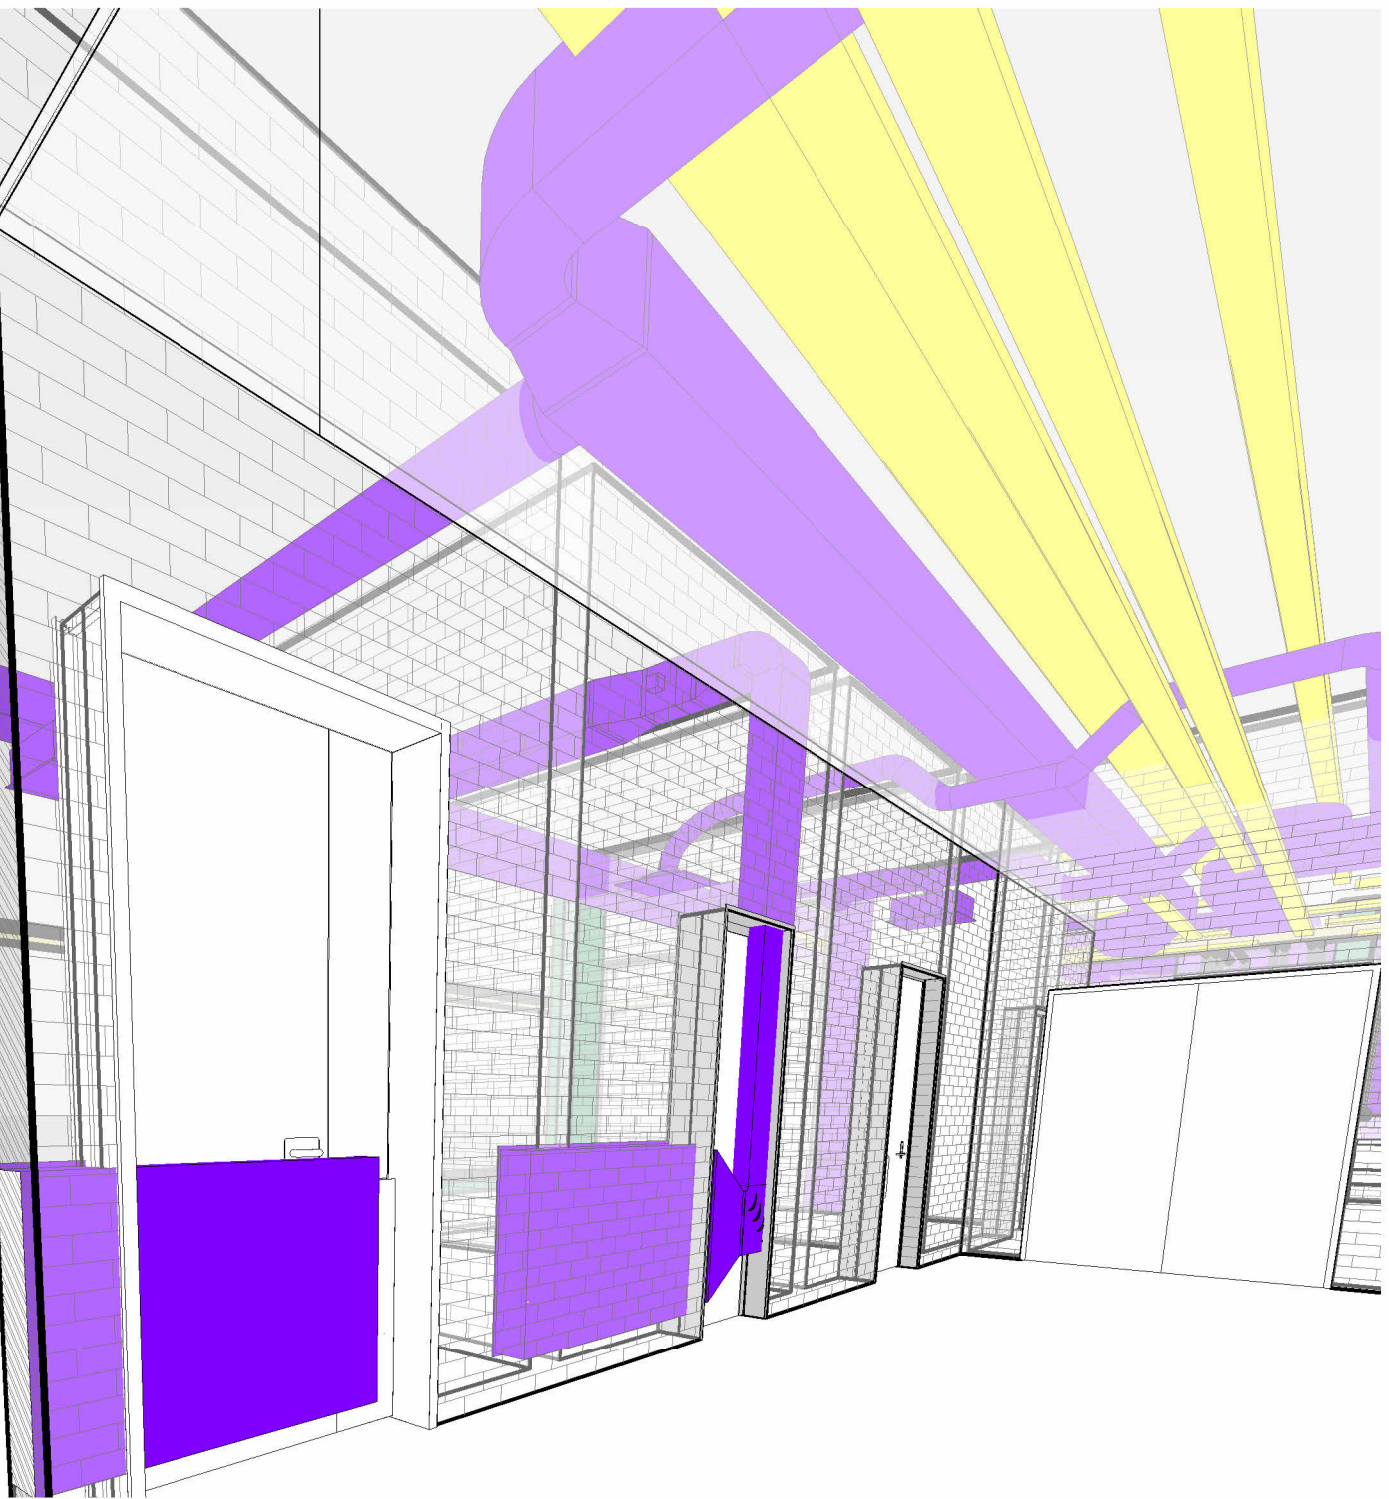

Passage HVAC Clash


GENERAL NOTES

A1

1. Contractor to verify all levels, heights and site dimensions before putting any work to hand;
2. any discrepancies to be reported to the architect immediately for clarification;
3. this drawing is not to be scaled - figured dimensions are to be used at all times;
4. all work to be carried out in strict accordance with local authorities requirements, National Building Regulations SANS 10400 and other relevant SANS standards.
5. This drawing is to be read in conjunction with all relevant consultants drawings, details and specifications.
6. All shop drawings are to be submitted for Architects approval prior to manufacture or installation.
7. Only the latest revision is to be used.
8. All dimensions are given in millimeters.
9. The Architect accepts no responsibility for errors resulting from the misinterpretation of this drawing.

© COPYRIGHT:
Please note that the copyright of the literary works, artistic works and published editions contained herein is vested with the JV Architects. Any adaption, distribution, sale or hire for, or any form of reproduction of these works, in any part or in their entirety, by any party other than the JV Architects is an infringement of this copyright, and the JV Architects reserves the right to claim damages from any party infringing this copyright, unless these rights are varied in writing.

REV	DATE	DESCRIPTION
A	2025.08.28	Deliverable 14

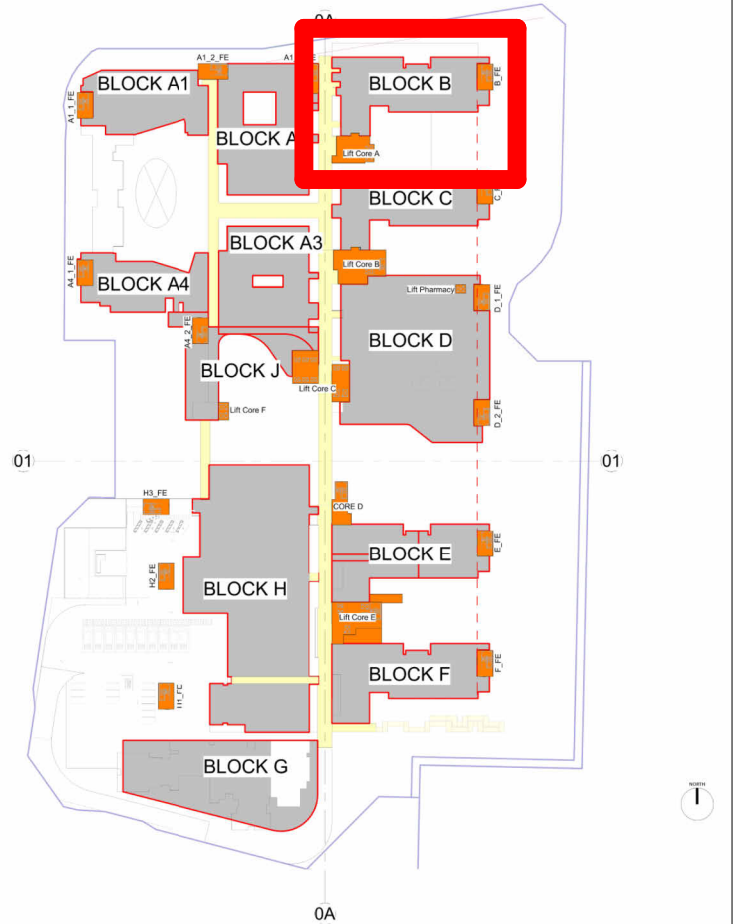

CLIENT:
WESTERN CAPE GOVERNMENT INFRASTRUCTURE

PROJECT:
BELHAR HOSPITAL



DRAWING:
4 Level 4 ffl ORTHOPAEDICS 2 _ Coordination 3D

SCALE: 1 : 50
DATE: 12/11/25

DRAWN: BB
CHECKED: AA

DRAWING NUMBER: C1840025 - ARC - FL - B - DR - ARC - 1210.10
REV: A



THIRTYTHREE 18
JOINT VENTURE

Tel: +27 (0) 21 419-7760 | Email: studio@ehharch.com
Unit G8, Victoria Junction, 56 Prestwich Street, De Waterkant, Cape Town, 8001.

DRAWING STATUS:

FOR INFORMATION

