

[illegible]

March 2016 Approved vs February 2023 Amended Submission Balance A - C	
*	
(-)189m ²	
(-)359m ²	
603m ²	
1m ²	
56m ²	
WPCA USAGE	
Comments	
Unchanged	
Unchanged	
Approved 15 April 2019	
Reduced Area	
Reduced Area	
Unchanged	
2100m ²	

THIS TABLE INCLUDES STUDENT & STADIUM SEATING ALLOWANCES

LUMS 4 SUBMISSION DECEMBER 2022	
P.O.I.-G.L.A - 7545m² * REMAINS UNCHANGED	
11 319 m² GLA	
1 619m²GLA	
73m²GLA	
851m² GLA	
19132 Seats (18500 spectator & 632 support staff)	
19 487m²	(19543m²-19487m² = 56m² SURPLUS GLA)

Off street Parking Requirements as previously approved under PT1 public transport zoning

GLA USE	USE/m2	No Students	PARKING RATIO	Total Bays Provided On SITE	Total Bays Provided On SITE
Place of Instruction		3 160	0.1 bays per student	316	432
1 bay per POI office = 21	1920			21	21
1 bay per lecture hall = 39	5625			39	39
			Total Bays for Place of Instruction	376	
Offices (Commercial) *	9399		2.5 bays per 100m ² GLA	235	264
Restaurants:	3618		1 bay per 25m ² GLA	42	41
Retail	73		2 bays per 100m ² GLA	2	2
Museum	851		1.5 bays per 100m ² GLA	13	13
TOTAL MPRL GLA USE	19 487		Total Bays for MPRL GLA Use	691	
Off street Parking Requirements For PT1 Zones					
Note: A parking department was approved in 2016 to permit 0 bays in lieu of 2775 bays for a sports stadium containing 18500 seats					
Total Existing Seats in Stadium	19519				
Seats removed as part of separate	299				
Application Case ID: 70574793					
Seats removed as part of this application (in front of restaurant and demolition permit)	510				
Seats remaining in the stadium	18710				
Seats additional to the parking departure for 18500 seats	210		3 bays per 20 seats	32	
			Sub-Total Parking Bays Required	722	
30 Motorcycle parking bays gives a credit of 7 parking bays (4 per bay)					
210 Bicycle parking bays gives a credit of 21 parking bays (10 per bay)					
Total possible credit parking bays 28 parking bays subject to 143 below					
Total credit net can exceed 2.5% credit of required bays					
TOTAL PARKING BAYS REQUIRED				(18)	
				704	
As per SANS 10400 Part S:					
Disabled Bays		812	Parking bays provided on site		
		÷ 25	Under cover car parking bays		812
			Includes uncovered car parking bays		84
		33	Includes parking bays for Disabled		33
TOTAL REGULAR PARKING BAYS PROVIDED				812	
SURPLUS PARKING					108 bays

- COMPLIANCE WITH MPBL
- HEIGHTS AND BUILDING LINES COMPLIES
- PARKING AND LOADING COMPLIES WITH PT1 ZONE
- 188 PARKING BAYS PROVIDED
- SITE ACCESS COMPLIES
- REFUSE AND WASTE MANAGEMENT COMPLIANCE
- RETAIL AREAS OCCUR ON GROUND FLOOR
- SEATING REMAINS UNCHANGED FROM LUMS 3
- PRECINCT ACCESS POINTS REMAIN UNCHANGED
ROAD CARRIAGEWAY & ROAD IMPROVEMENTS
REMAIN AS SUCH.

TABLES 3,4,5 IN MOTIVATIOIN REPORT ATTACHED

• TABLE 3 - AREAS BREAKDOWN - NORTH PAVILION
+ AUDITORIUM LVL 0

• **TABLE 4 - 3. AREAS SUMMARY - NORTH QUADRANT
(BUSINESS PARK)**

• TABLE 5- PARKING

PRECINCT PHASING AS PER SITE PLAN:

PHASE 1A
QUADRANT BUILDING
WICKET BUILDING
PARKING AND SPL

PHASE 1B:
SNAKEPIT BUILDING

PHASE 2A:
NORTH PAVILION AND AUDITORIUM

PHASE 2B:
CAMPGROUND BUILDING

All works to comply with building codes listed as specified:

[illegible]

G	Local Authority Submission	2024.09.17	BB	Local Authority
F	Local Authority Submission	2024.01.29	AL	Local Authority
E	AMENDED FOR LOCAL AUTHORITY APPROVAL	2023.03.17	MdV	LOCAL AUTHORITY
D	AMENDED FOR LOCAL AUTHORITY APPROVAL	2023.02.07	MdV	LOCAL AUTHORITY
	- Information	2022.11.11	RL	CNDP
C	Local Authority Submission	2022.10.10	NV	CNDP
B	Local Authority Submission - (changes to tables as requested by CNDP)	2022.02.21	NV	CNDP

ID	Revision Category	Date	Issued by	Issued to
Revisions				

FOR LOCAL AUTHORITY SUBMISSION ONLY

architect signature

99 buitenkant street
gardens, cape town
8001
[t] +27 21 462 1824
[f] +27 21 462 1629
[e] info@jakupa.co.za
www.jakupa.co.za

jakupa
architects and urban designers

client WPCA signature 

project title	
NCG North Pavilion	
NORTH PAVILION	

drawing title

BDM - Site Plan

location

ERF 144264 - NEWLANDS CRICKET
GROUND

date
29/10/24

scale	drawn	checked
As indicated	Md	GA

project number	stage	building	series	dwg no.	revision
----------------	-------	----------	--------	---------	----------

2321 LA NP PL 001 G

[illegible]

ID	Revision Category	Date	Issued by	Issued to
Revisions				

NCG
The Newlands Cricket Ground
1888

99 buitenkant street
gardens, cape town
8001
[t] +27 21 462 1824
[t] +27 21 462 1629
[e] info@jakupa.co.za
www.jakupa.co.za

jakupa
architects and urban designers

project title

NCG North Pavilion

location

ERF 144264 - NEWLANDS CRICKET
GROUND

scale	drawn	checked
As indicated	BB	GA

2321 LA NP PL 100 H

The drawings are copyright and remain the property of Jakupa Architects and Urban Designers Pty Ltd. Copyright is reserved by them and the drawing is issued on the condition that it is not copied, reproduced, retained or disclosed to any unauthorized person, either wholly or in part without the written consent from Jakupa.

All works to comply with building codes listed as specified:

SANS 10400-A: General Principles and Requirements
Construction to be administered by registered Professional Engineer
SANS 10400-B: Structural
Structural Design by Stephanus Hermanus Calitz PE(Eng 20080089)
SANS 10400-C: Dimensions
All dimensions to comply
SANS 10400-D: Public Safety
All works to comply
SANS 10400-E: Site Operations
Works to comply, Health and Safety Agent to oversee works during building construction
SANS 10400-F: Excavations
Excavations shall be monitored by Health and Safety Agent and Stephanus Hermanus Calitz PE(Eng 20080089)
SANS 10400-G: Foundations
Structural design by Stephanus Hermanus Calitz PE(Eng 20080089)
SANS 10400-H: Floors
Works to comply, Concrete surface beds and substructure to structural engineer's details
SANS 10400-I: Walls
Works to comply
SANS 10400-J: Roofs
Works to comply
SANS 10400-K: Glazing
Works to comply
SANS 10400-L: Stairs
Works to comply
SANS 10400-M: Lighting and Ventilation
Works to comply
SANS 10400-N: Drainage
Rational design by Gerhard R. Muller ECSA 20160086
SANS 10400-O: Non-waste-house means of sanitary disposal
Not applicable
SANS 10400-P: Stormwater Disposal
Rational design by Gerhard R. Muller ECSA 20160086
SANS 10400-Q: Fire Protection
Rational design by Gerhard R. Muller ECSA 20160086
SANS 10400-R: Space Heating
Rational design by Johannes Jacobus van Deventer ECSA 20090396
SANS 10400-S: Free Installation
Rational design by Gerhard R. Muller ECSA 20160086
SANS 10400-T: Energy Efficiency
Rational design by Gerhard R. Muller ECSA 20160086



H	Local Authority Submission	2024.11.11	BB	Local Authority
G	Local Authority Submission	2024.10.29	BB	Local Authority
F	Local Authority Submission	2024.10.28	BB	Local Authority
E	Local Authority Submission	2024.10.07	BB	Local Authority
D	Local Authority Submission	2024.09.17	BB	Local Authority
C	Local Authority Submission	2024.01.29	AL	Local Authority
B	Local Authority Submission	2021.08.27	NV	Local Authority
A	Local Authority Submission	2021.08.10	NV	Local Authority

ID	Revision Category	Date	Issued by	Issued to
Revisions				

FOR LOCAL AUTHORITY SUBMISSION ONLY



architect  signature

99 buitenkant street
gardens, cape town
8001
(t) +27 21 462 1824
(f) +27 21 462 1629
[e]info@jakupa.co.za
www.jakupa.co.za

 architects and urban designers

client  signature

WPCA

project title

NCG North Pavilion

drawing title

Level 2 Plan

location

ERF 144264 - NEWLANDS CRICKET GROUND

date

11/11/24

scale drawn checked

As indicated BB GA

project number stage building series dwg no. revision

2321 LA NP PL 101 H



LA_LEVEL 3 CS 1
SCALE: 1 : 100

The drawings are copyright and remain the property of Jakupa Architects and Urban Designers Pty Ltd. Copyright is reserved by them and the drawing is issued on the condition that it is not copied, reproduced, retained or disclosed to any unauthorized person, either wholly or in part without the written consent from Jakupa.

- All works to comply with building codes listed as specified:
- SANS 10400-A: General Principles and Requirements
 - Construction to be administered by professional Pathway 2025
 - SANS 10400-B: Structural
 - Structural Design by Stephana Hermanus Calitz PEEng 50808089
 - SANS 10400-C: Dimensions
 - All dimensions to comply
 - SANS 10400-D: Public Safety
 - All works to comply
 - SANS 10400-E: Site Operations
 - Works to comply, Health and Safety Agent to oversee works during building construction
 - SANS 10400-F: Excavations
 - Excavations shall be monitored by Health and Safety Agent and Stephana Hermanus Calitz PEEng 50808089
 - SANS 10400-G: Foundations
 - Structural design by Stephana Hermanus Calitz PEEng 50808089
 - SANS 10400-H: Floors
 - Works to comply, Concrete surface beds and substructure to structural engineer's details
 - SANS 10400-I: Walls
 - Works to comply
 - SANS 10400-J: Roofs
 - Works to comply
 - SANS 10400-K: Glazing
 - Works to comply
 - SANS 10400-L: Scaffolding
 - Works to comply
 - SANS 10400-M: Lighting and Ventilation
 - Works to comply
 - SANS 10400-N: Drainage
 - Rational design by Gerhard R Muller ECSA 20160086
 - SANS 10400-O: Non-waste-house means of sanitary disposal
 - Not applicable
 - SANS 10400-P: Stormwater Disposal
 - Rational design by Gerhard R Muller ECSA 20160086
 - SANS 10400-Q: Fire Protection
 - Rational design by Gerhard R Muller ECSA 20160086
 - SANS 10400-R: Space Heating
 - Rational design by Johannes Jacobus van Deventer ECSA 20090396
 - SANS 10400-S: Fire Installation
 - Rational design by Gerhard Gou ECSA 20070309
 - SANS 10400-T: Energy Efficiency
 - Rational design by Graham Sher SACAP 4190

H	Local Authority Submission	2024.11.11	BB	Local Authority
G	Local Authority Submission	2024.10.29	BB	Local Authority
F	Local Authority Submission	2024.10.28	BB	Local Authority
E	Local Authority Submission	2024.10.07	BB	Local Authority
D	Local Authority Submission	2024.09.17	BB	Local Authority
C	Local Authority Submission	2024.01.29	AL	Local Authority
B	Local Authority Submission	2021.08.27	NV	Local Authority
A	Local Authority Submission	2021.08.10	NV	Local Authority

ID	Revision Category	Date	Issued by	Issued to
Revisions				

FOR LOCAL AUTHORITY SUBMISSION ONLY

NCG

The Newlands Cricket Ground

1888

architect

client

99 buitenkant street
gardens, cape town
8001
(t) +27 21 462 1824
(f) +27 21 462 1629
(e) info@jakupa.co.za
www.jakupa.co.za

client
WPCA

project title
NCG North Pavilion

drawing title
Level 3 Plan

location
ERF 144264 - NEWLANDS CRICKET GROUND

date
11/11/24

scale
As indicated

drawn
BB

checked
GA

project number	stage	building	series	dwg no.	revision
2321	LA	NP	PL	102	H

The drawings are copyright and remain the property of Jakupa Architects and Urban Designers Pty Ltd. Copyright is reserved by them and the drawing is issued on the condition that it is not copied, reproduced, retained or disclosed to any unauthorized person, either wholly or in part without the written consent from Jakupa.

All works to comply with building codes listed as specified:

SANS 10400-A: General Principles and Requirements
SANS 10400-B: Structure
SANS 10400-C: Dimensions
SANS 10400-D: Fire Protection
SANS 10400-E: Sanitation
SANS 10400-F: Site Operations
SANS 10400-G: Excavations
SANS 10400-H: Walls
SANS 10400-I: Floors
SANS 10400-J: Foundations
SANS 10400-K: Roofs
SANS 10400-L: Glazing
SANS 10400-M: Stairs
SANS 10400-N: Lighting and Ventilation
SANS 10400-O: Drainage
SANS 10400-P: Non-water-borne means of sanitary disposal
SANS 10400-Q: Stormwater Disposal
SANS 10400-R: Fire Protection
SANS 10400-S: Fridge Installation
SANS 10400-T: Energy Efficiency
SANS 10400-U: Energy Efficiency
SANS 10400-V: Energy Efficiency
SANS 10400-W: Energy Efficiency
SANS 10400-X: Energy Efficiency
SANS 10400-Y: Energy Efficiency
SANS 10400-Z: Energy Efficiency



1 LA_LEVEL 4 CS 1
SCALE: 1 : 100

H	Local Authority Submission	2024.11.11	BB	Local Authority
G	Local Authority Submission	2024.10.29	BB	Local Authority
F	Local Authority Submission	2024.10.28	BB	Local Authority
E	Local Authority Submission	2024.10.07	BB	Local Authority
D	Local Authority Submission	2024.09.17	BB	Local Authority
C	Local Authority Submission	2024.01.29	AL	Local Authority
B	Local Authority Submission	2021.08.27	NV	Local Authority
A	Local Authority Submission	2021.08.10	NV	Local Authority

ID	Revision Category	Date	Issued by	Issued to
Revisions				

FOR LOCAL AUTHORITY SUBMISSION ONLY



architect signature

99 buitenkant street
gardens, cape town
8001
(t) +27 21 462 1824
(f) +27 21 462 1629
[e]info@jakupa.co.za
www.jakupa.co.za



client signature

WPCA

project title
NCG North Pavilion

drawing title
Level 4 Plan

location
ERF 144264 - NEWLANDS CRICKET GROUND

date
11/11/24


scale drawn checked
As indicated BB GA

project number stage building series dwg no. revision

2321 LA NP PL 103 H

The drawings are copyright and remain the property of Jakupa Architects and Urban Designers Pty Ltd. Copyright is reserved by them and the drawing is issued on the condition that it is not copied, reproduced, retained or disclosed to any unauthorized person, either wholly or in part without the written consent from Jakupa.

All works to comply with building codes listed as specified:
SANS 10400-A: General Principles and Requirements
Construction to be administered by registered Professional Engineer 6235
SANS 10400-B: Structural
Structural Design by Stephanus Hermanus Calitz PEng 20080089
SANS 10400-C: Dimensions
All dimensions to comply
SANS 10400-D: Public Safety
All works to comply
SANS 10400-E: Site Operations
Works to comply, Health and Safety Agent to oversee works during building construction
SANS 10400-F: Escalators
Escalators shall be monitored by Health and Safety Agent and Stephanus Hermanus Calitz PEng 20080089
SANS 10400-G: Foundations
Structural design by Stephanus Hermanus Calitz PEng 20080089
SANS 10400-H: Floors
Works to comply, Concrete surface beds and substructure to structural engineer's details
SANS 10400-I: Walls
Works to comply
SANS 10400-J: Roofs
Works to comply
SANS 10400-K: Cladding
Works to comply
SANS 10400-L: Stairs
Works to comply
SANS 10400-M: Lighting and Ventilation
Works to comply
SANS 10400-N: Drainage
Rational design by Gerhard R. Muller ECSA 20160086
SANS 10400-O: Non-water-borne means of sanitary disposal
Not applicable
SANS 10400-P: Stormwater Disposal
Rational design by Gerhard R. Muller ECSA 20160086
SANS 10400-Q: Fire Protection
Rational design by Gerhard R. Muller ECSA 20160086
SANS 10400-R: Space Heating
Rational design by Gerhard R. Muller ECSA 20160086
SANS 10400-S: Fire Installation
Rational design by Gerhard R. Muller ECSA 20160086
SANS 10400-T: Energy Efficiency
Rational design by Gerhard R. Muller ECSA 20160086

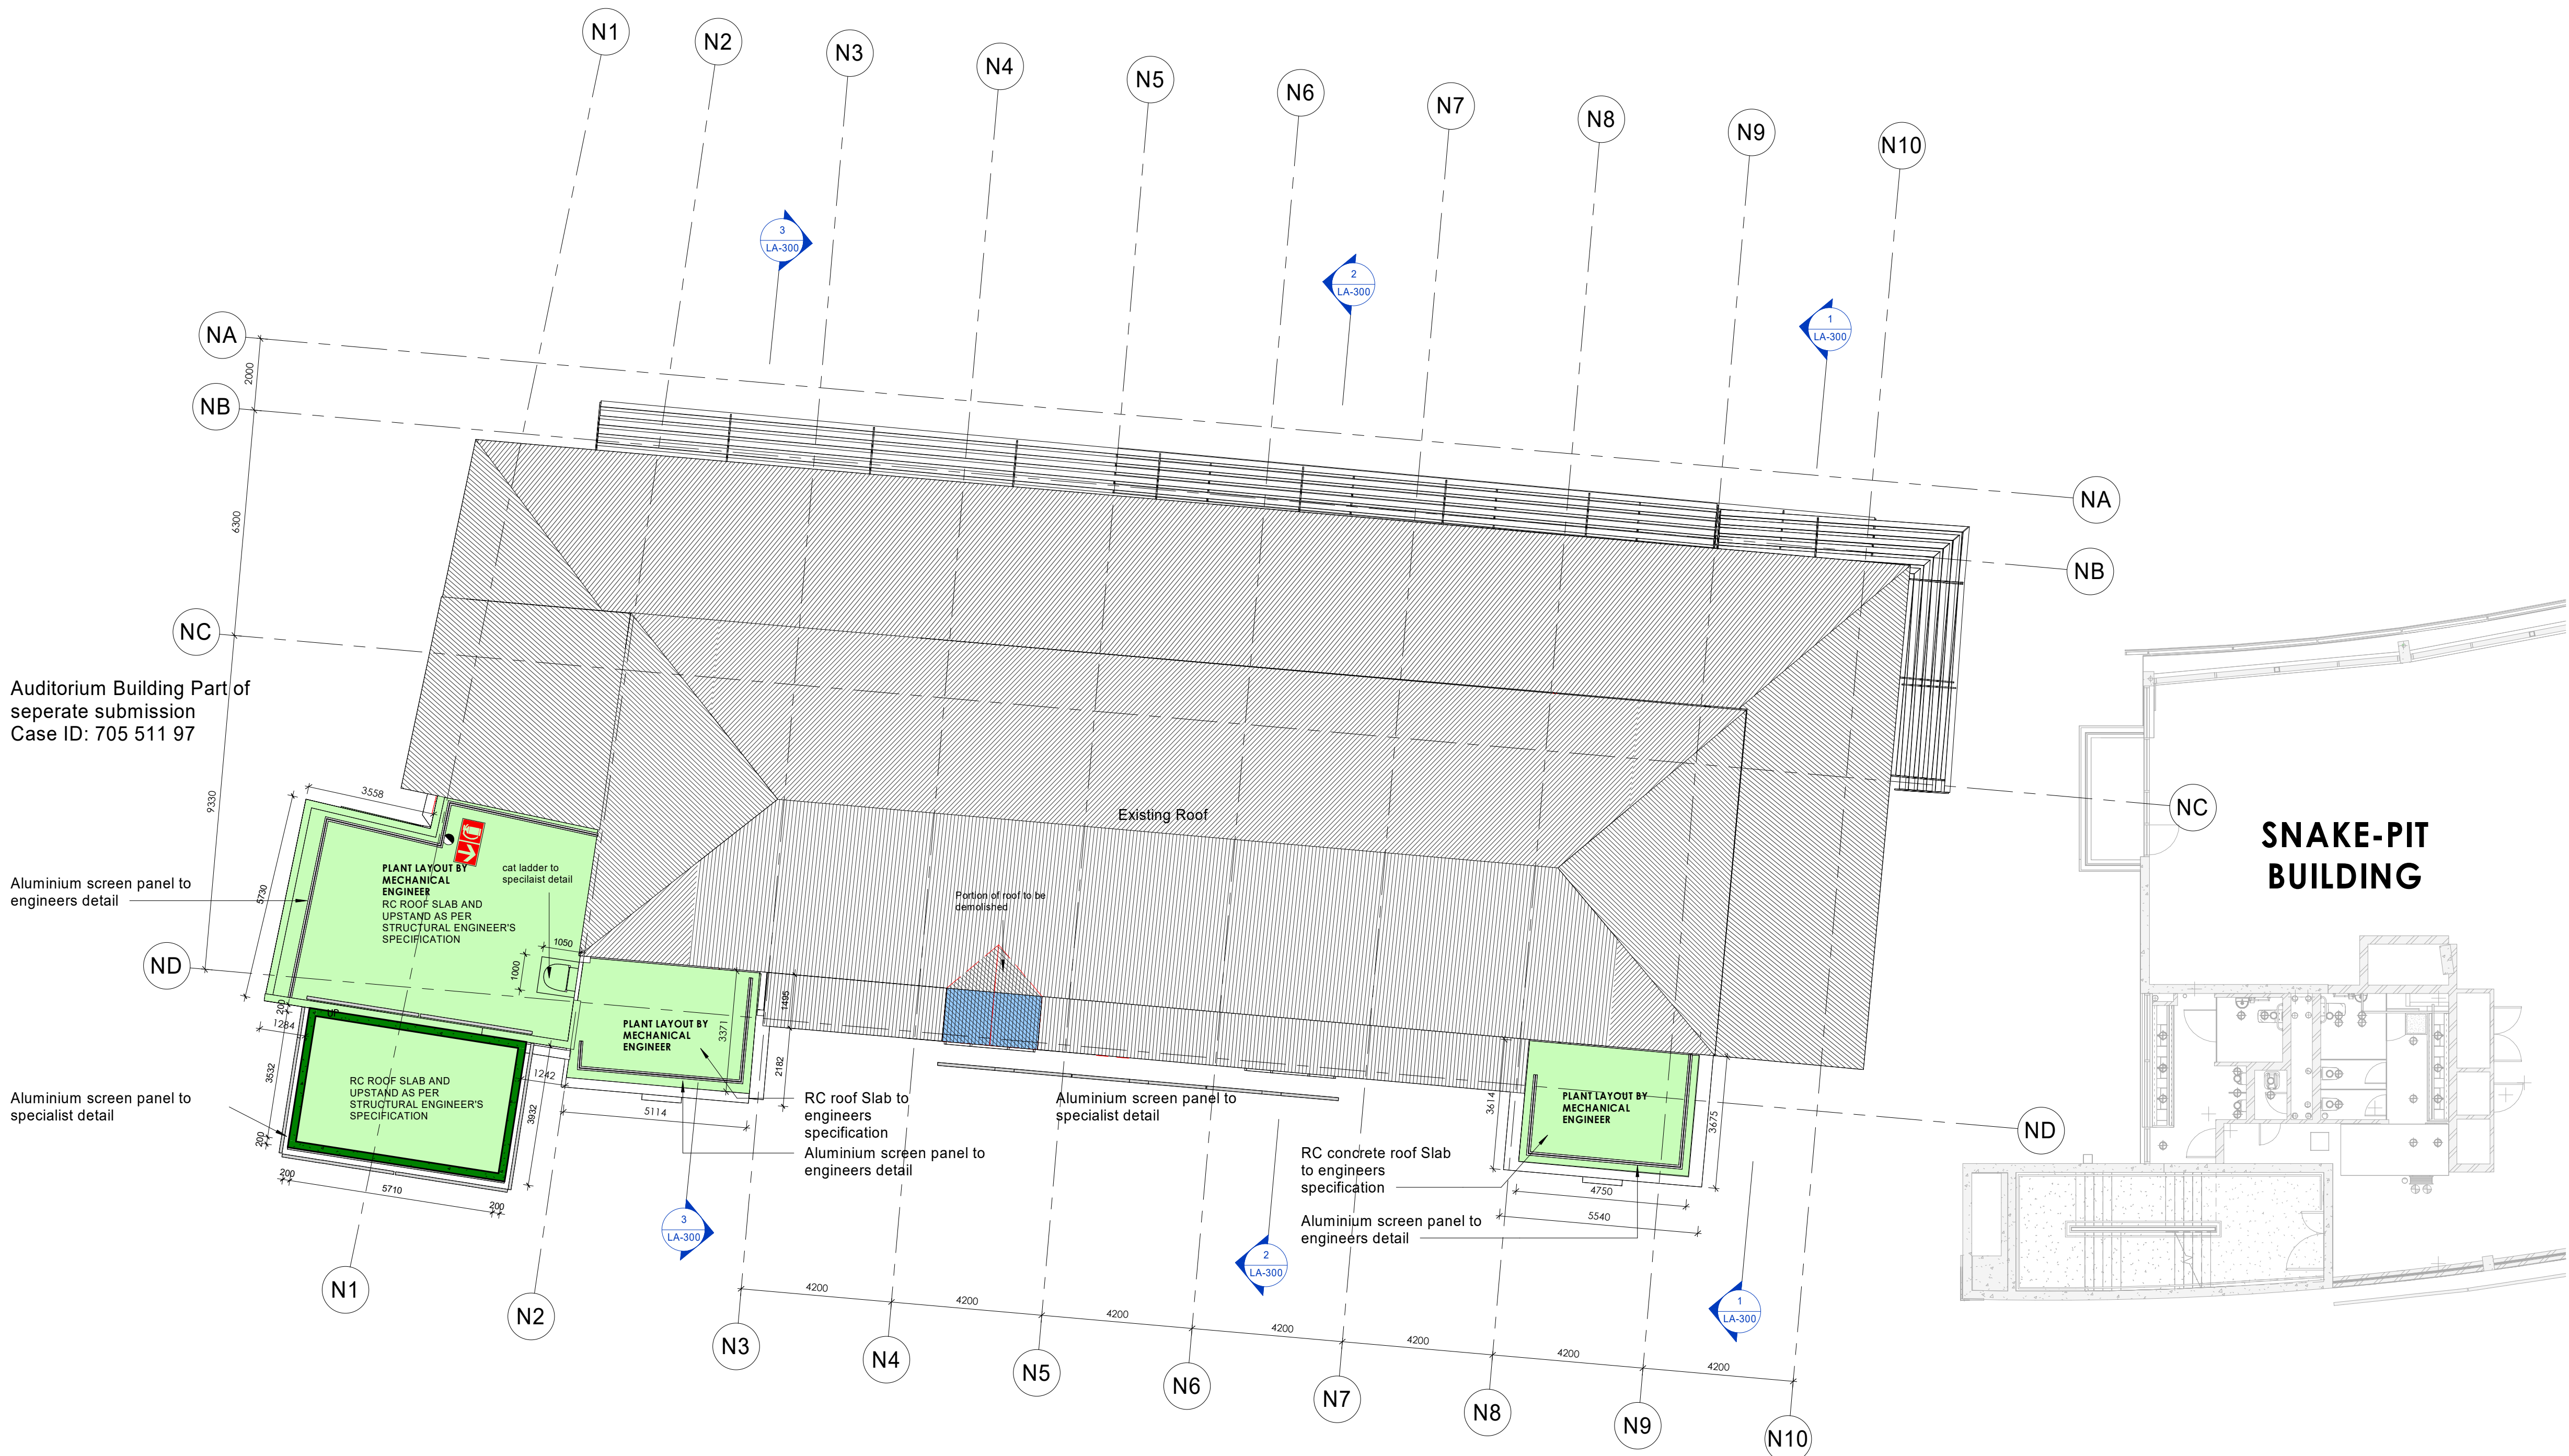

F	Local Authority Submission	2024.11.11	BB	Local Authority
E	Local Authority Submission	2024.10.29	BB	Local Authority
D	Local Authority Submission	2024.09.17	BB	Local Authority
C	Local Authority Submission	2024.01.29	AL	Local Authority
B	Local Authority Submission	2021.08.27	NV	Local Authority
A	Local Authority Submission	2021.08.10	NV	Local Authority

ID	Revision Category	Date	Issued by	Issued to
Revisions				

FOR LOCAL AUTHORITY SUBMISSION ONLY



architect  signature

99 buitenkant street
gardens, cape town
8001
(t) +27 21 462 1824
(f) +27 21 462 1629
(e) info@jakupa.co.za
www.jakupa.co.za



client  signature

WPCA

project title

NCG North Pavilion

drawing title

Roof Plan

location

ERF 144264 - NEWLANDS CRICKET GROUND

date

11/11/24

scale drawn checked


As indicated BB GA

project number stage building series dwg no. revision


2321 LA NP PL 104 F

All works to comply with building codes listed as specified:

- SANS 10400-A: General Principles and Requirements
- Construction to be administered by programme Fether Patch 6235
- SANS 10400-B: Structural
- Structural design by Stephanus Hermanus Calitz PEEng 20080089
- All dimensions to comply
- SANS 10400-C: Dimensions
- All dimensions to comply
- SANS 10400-D: Public Safety
- All works to comply
- SANS 10400-E: Site Questions
- Works to comply Health and Safety Agent to oversee works during building construction
- SANS 10400-F: Excavations
- Excavations shall be monitored by Health and Safety Agent and Stephanus Hermanus Calitz PEEng 20080089
- SANS 10400-H: Foundations
- Structural design by Stephanus Hermanus Calitz PEEng 20080089
- SANS 10400-J: Floors
- Works to comply Concrete surface beds and substructure to structural engineer's details
- SANS 10400-K: Walls
- Works to comply
- SANS 10400-L: Roofs
- Works to comply
- SANS 10400-M: Cladding
- Works to comply
- SANS 10400-N: Stairs
- Works to comply
- SANS 10400-O: Lighting and Ventilation
- Works to comply
- SANS 10400-P: Drainage
- Rational design by Gerhard R. Muller ECSA 20160086
- SANS 10400-Q: Non-water borne messes or sanitary disposal
- Not applicable
- SANS 10400-R: Stormwater Disposal
- Rational design by Gerhard R. Muller ECSA 20160086
- SANS 10400-T: Fire Protection
- Rational design by Gerhard R. Muller ECSA 20160086
- SANS 10400-V: Space Heating
- Rational design by Gerhard R. Muller ECSA 20160086
- SANS 10400-W: Space Heating
- Rational design by Gerhard R. Muller ECSA 20160086
- SANS 10400-X: Fire Installation
- Rational design by Gerhard R. Muller ECSA 20160086
- SANS 10400-Y: Fire Installation
- Rational design by Gerhard R. Muller ECSA 20160086
- SANS 10400-ZA: Energy Efficiency
- Rational design by Gertie Shep SACAP 4190

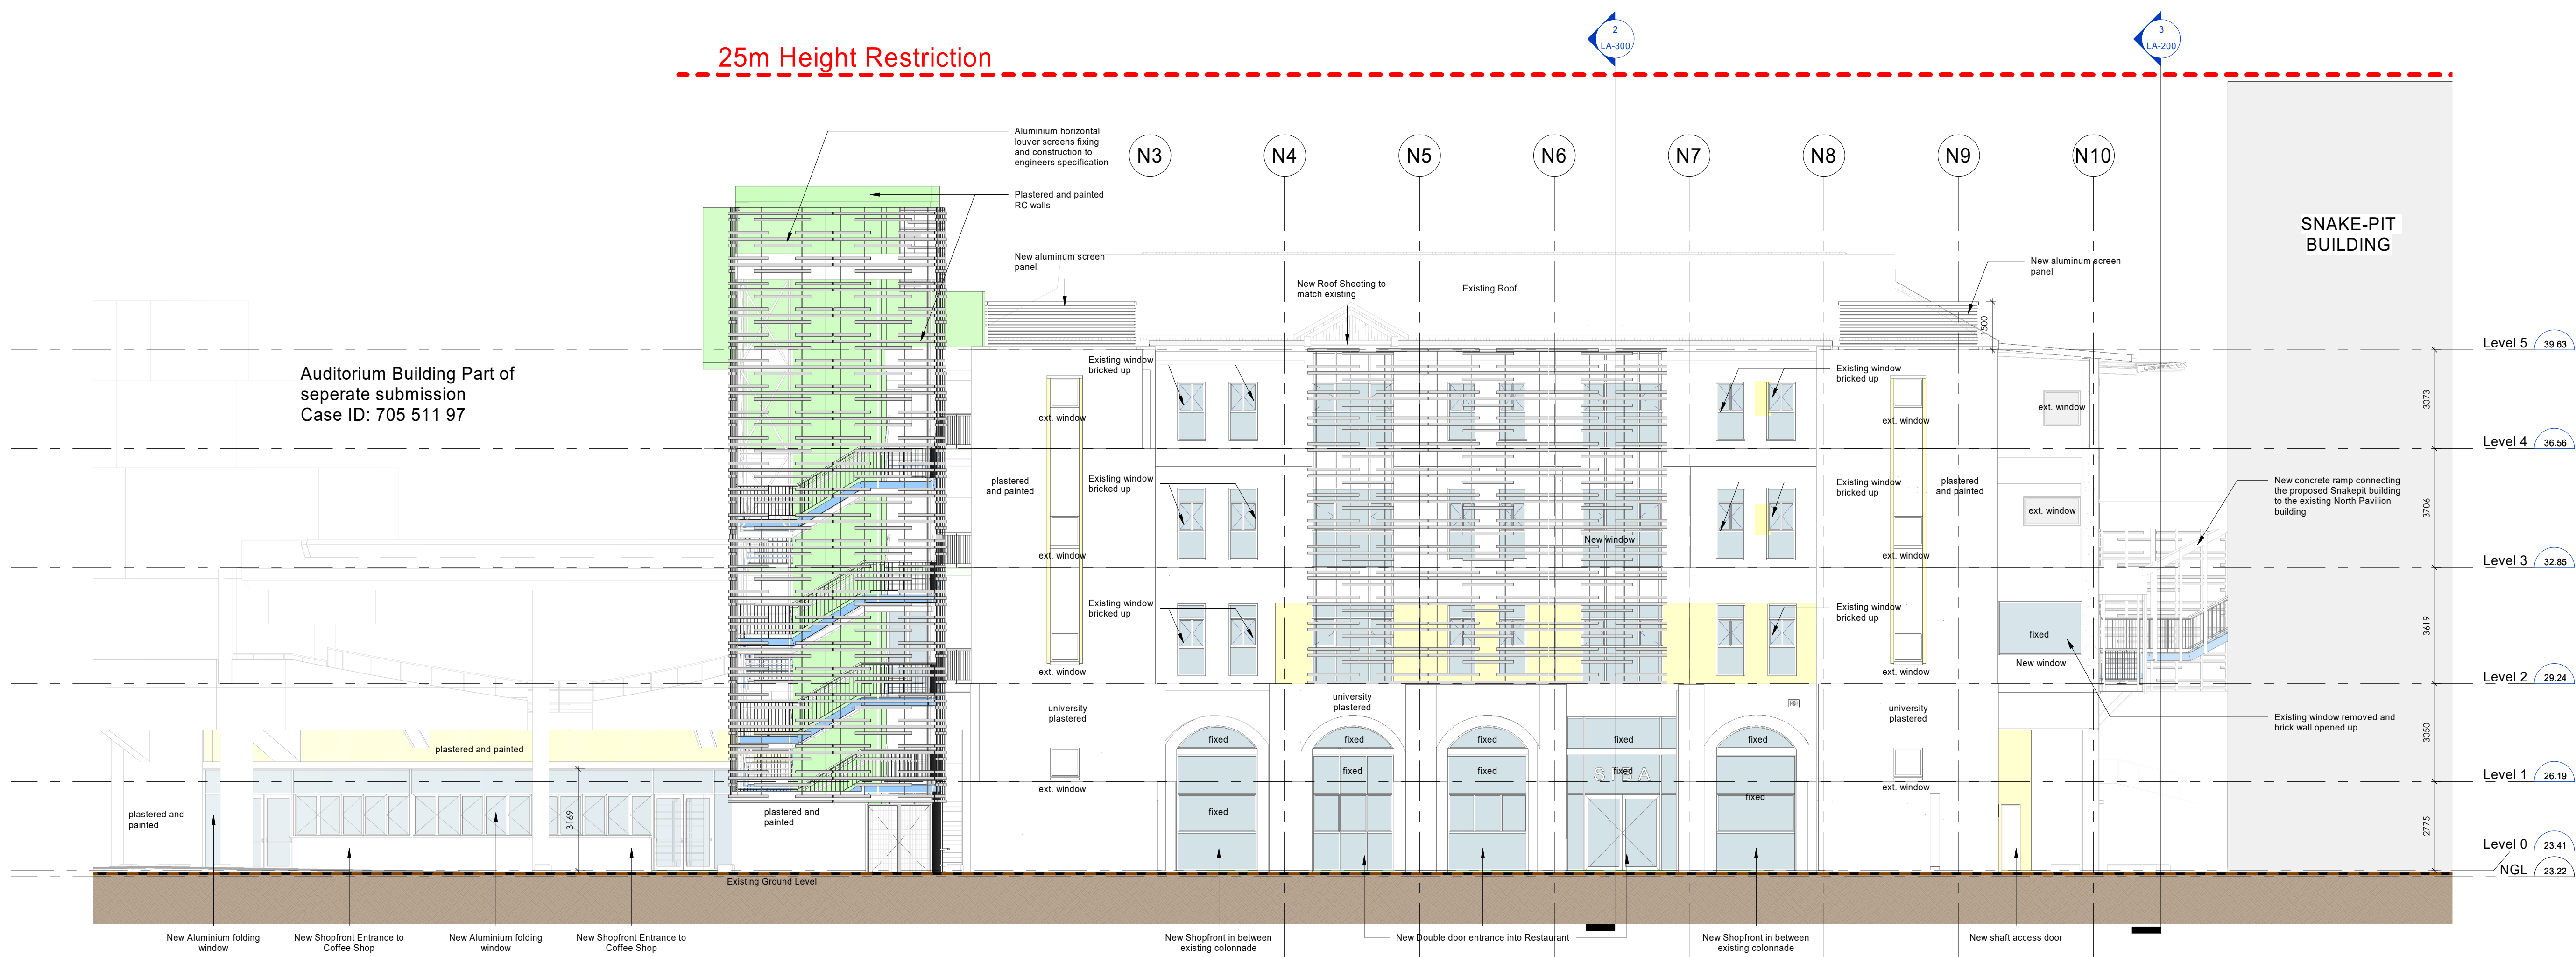

1 LA North Elevation
SCALE: 1 : 100

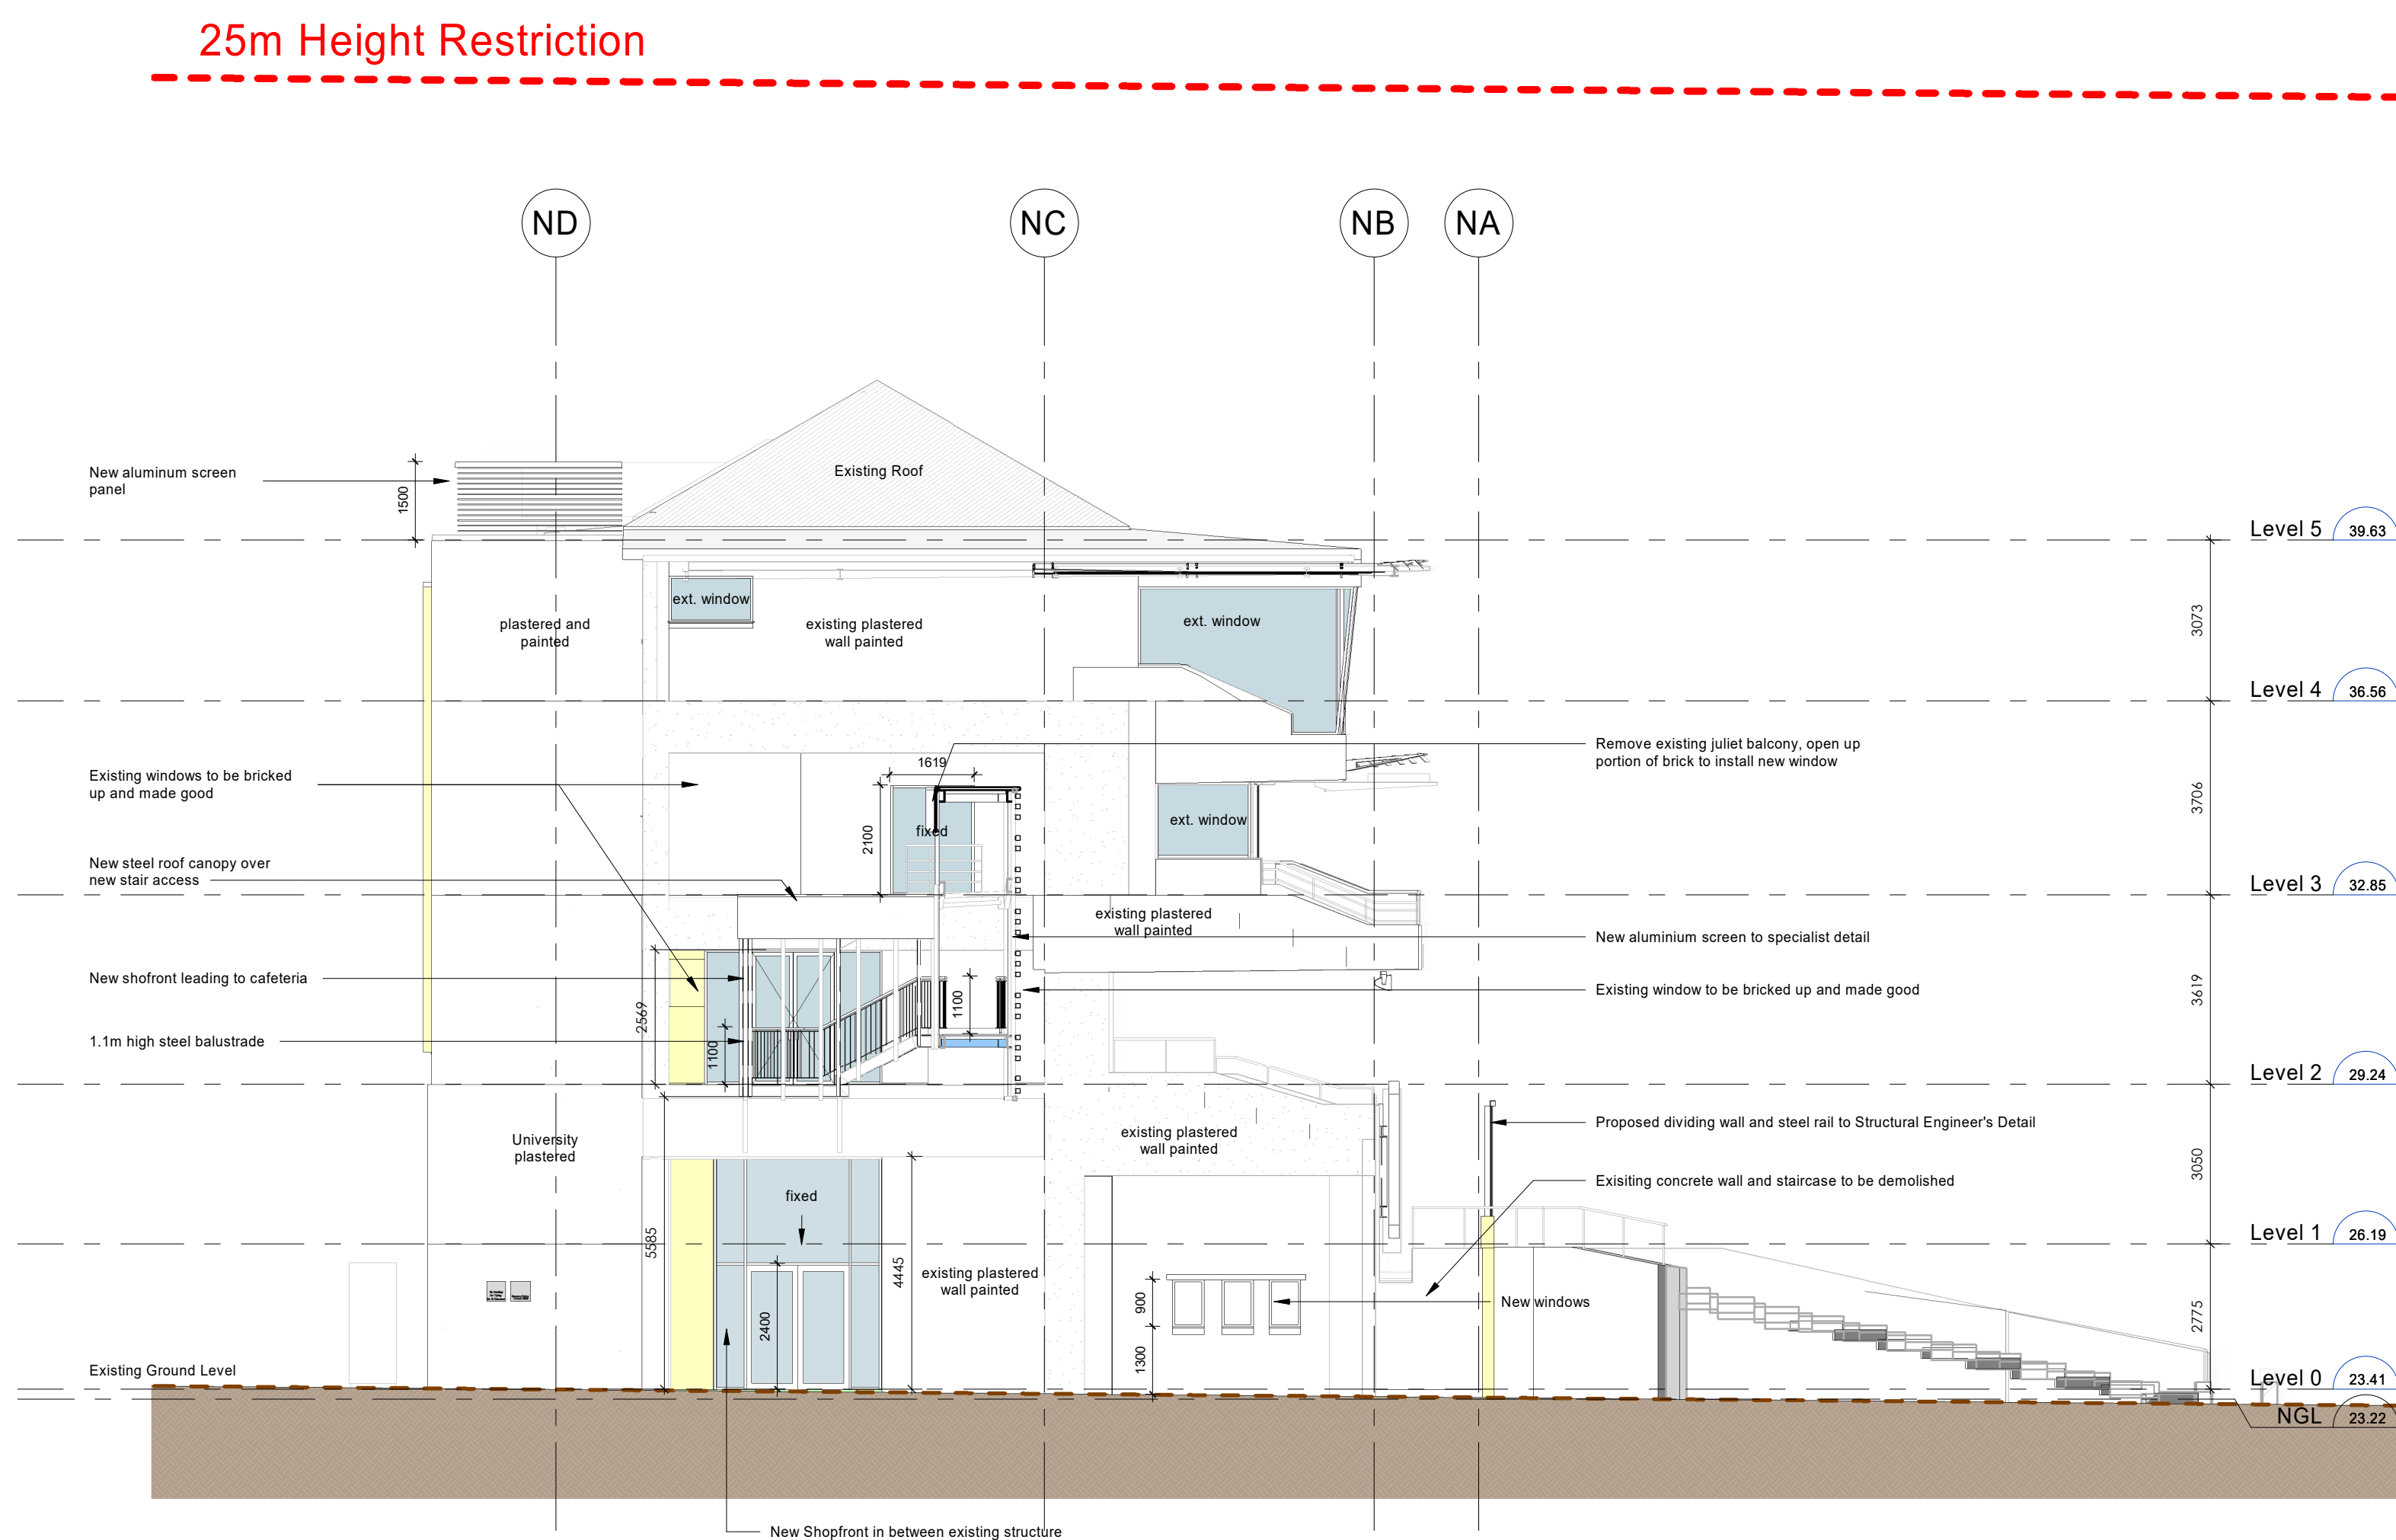

3 LA West Elevation
SCALE: 1 : 100

D	Local Authority Submission	2024.09.17	BB	Local Authority
C	Local Authority Submission	2024.01.29	AL	Local Authority
B	Local Authority Submission	2021.08.27	NV	Local Authority
A	Local Authority Submission	2021.08.10	NV	Local Authority

ID	Revision Category	Date	Issued by	Issued to
Revisions				

FOR LOCAL AUTHORITY SUBMISSION ONLY



architect  signature

99 buitenkant street
gardens, cape town
8001
(t) +27 21 462 1824
(f) +27 21 462 1629
(e) info@jakupa.co.za
www.jakupa.co.za



client  signature

WPCA

project title
NCG North Pavilion

drawing title
Elevations


location
ERF 144264 - NEWLANDS CRICKET GROUND

date
11/11/24

scale drawn checked
As indicated BB GA

project number stage building series dwg no. revision

2321 LA NP EL 200 D

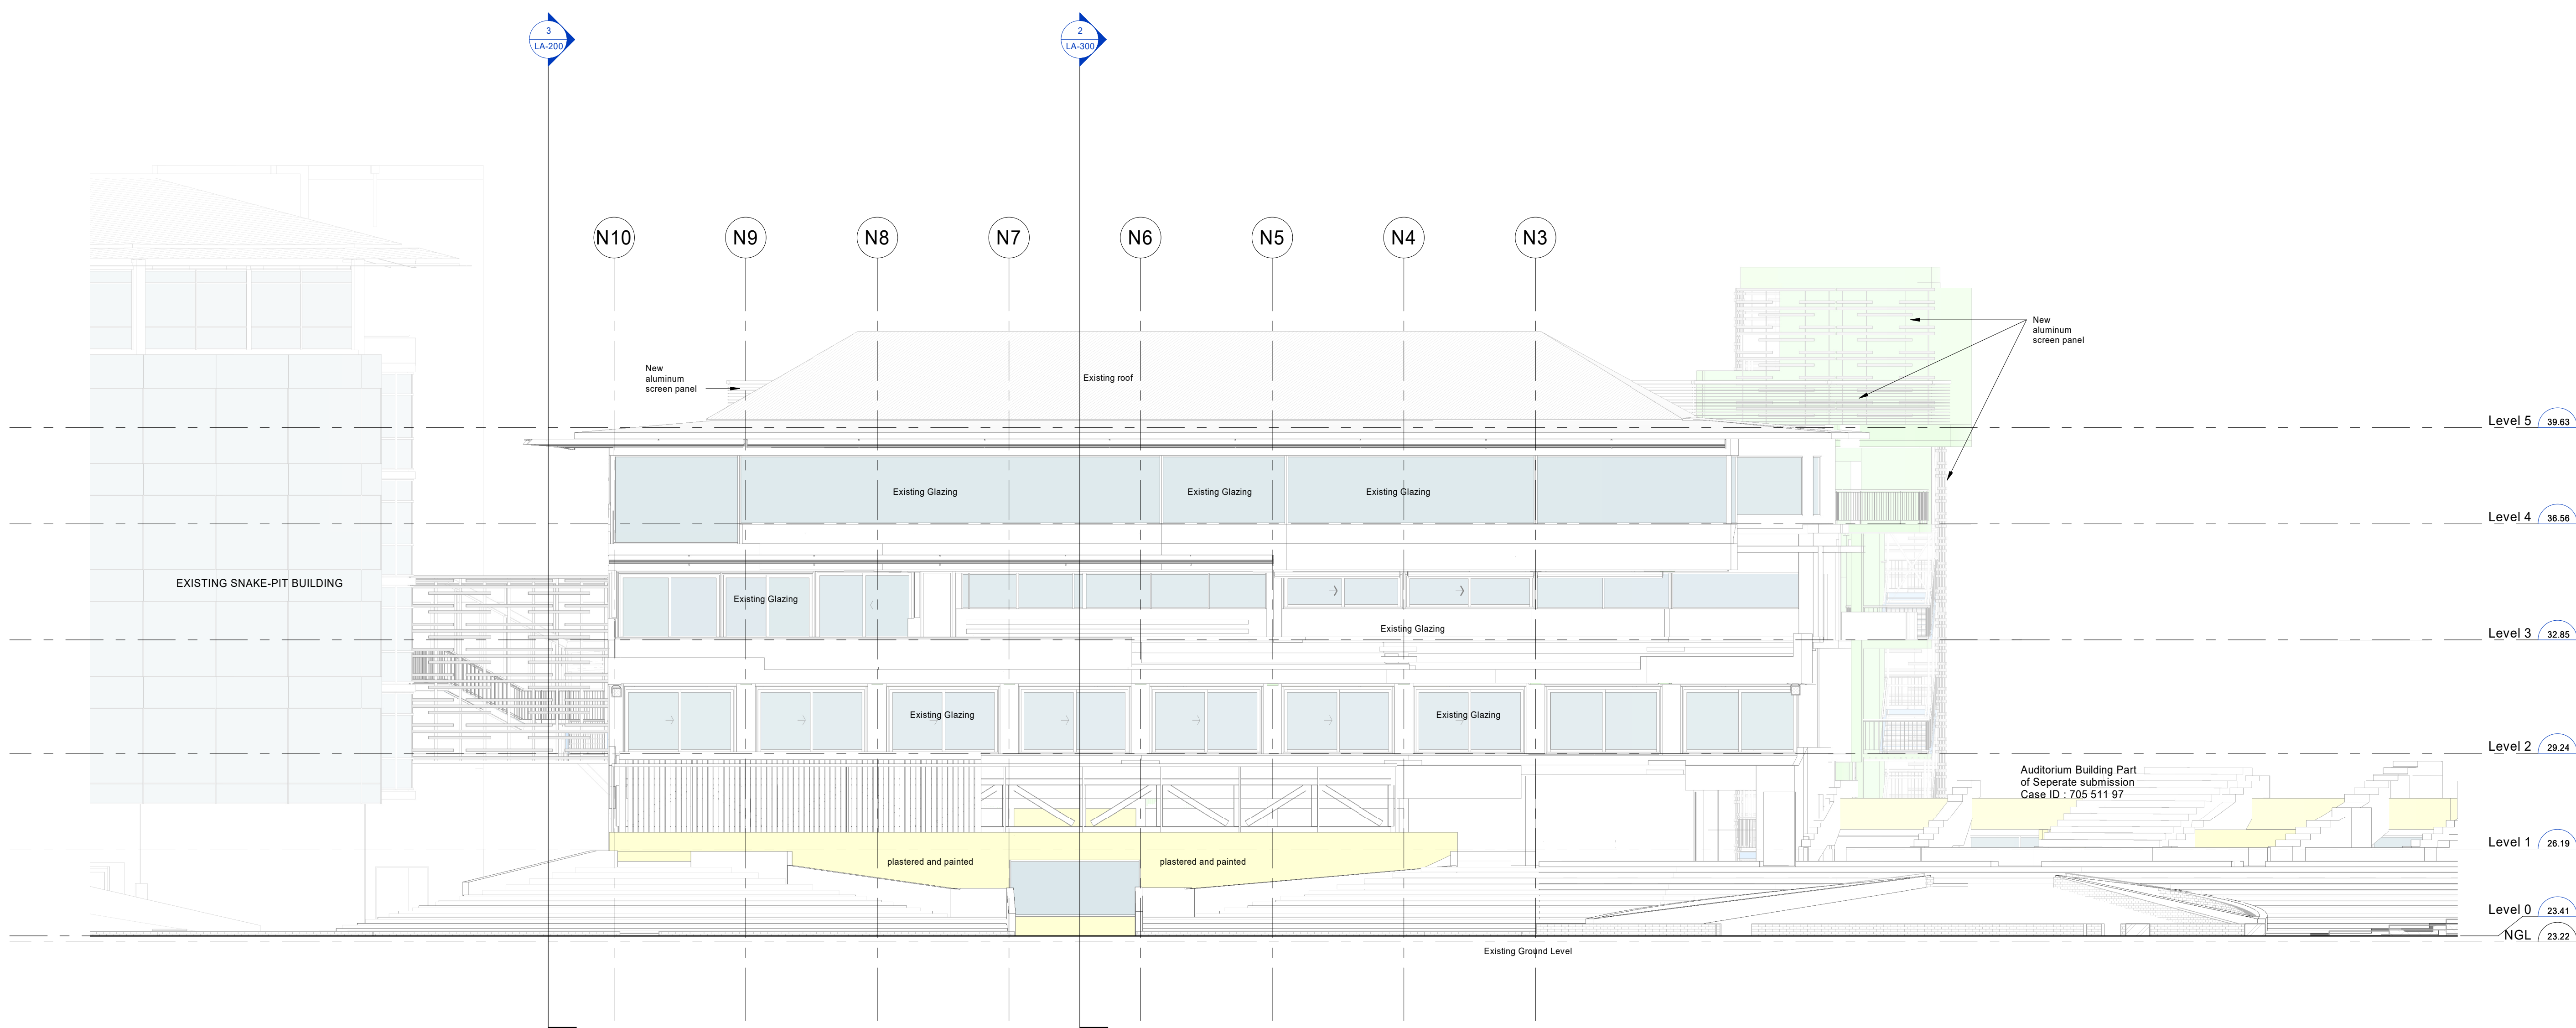

1 LA South Elevation
SCALE: 1 : 100

The drawings are copyright and remain the property of Jakupa Architects and Urban Designers Pty Ltd. Copyright is reserved by them and the drawing is issued on the condition that it is not copied, reproduced, retained or disclosed to any unauthorized person, either wholly or in part without the written consent from Jakupa.

- All works to comply with building codes listed as specified:
- SANS 10400-A: General Principles and Requirements
 - Construction to be administered by programme: Fallow Patch 6235
 - SANS 10400-B: Structural
 - Structural Design by Stephanus Hermanus Calitz PEEng 20080089
 - All dimensions to comply
 - SANS 10400-C: Dimensions
 - SANS 10400-D: Public Safety
 - All works to comply
 - SANS 10400-E: Site Operations
 - Works to comply: Health and Safety Agent to oversee works during building construction
 - SANS 10400-F: Excavations
 - Excavations shall be monitored by Health and Safety Agent and Stephanus Hermanus Calitz PEEng 20080089
 - SANS 10400-H: Foundations
 - Structural design by Stephanus Hermanus Calitz PEEng 20080089
 - SANS 10400-J: Floors
 - Works to comply: Concrete surface beds and substructure to structural engineer's details
 - SANS 10400-K: Walls
 - Works to comply
 - SANS 10400-L: Roofs
 - Works to comply
 - SANS 10400-M: Cladding
 - Works to comply
 - SANS 10400-N: Stairs
 - Works to comply
 - SANS 10400-O: Lighting and Ventilation
 - Works to comply
 - SANS 10400-P: Drainage
 - Rational design by Gerhard R. Muller ECSA 20160086
 - SANS 10400-Q: Non-water-borne wastes of sanitary disposal
 - Not applicable
 - SANS 10400-R: Stormwater Disposal
 - Rational design by Gerhard R. Muller ECSA 20160086
 - SANS 10400-T: Fire Protection
 - Rational design by Gerhard R. Muller ECSA 20070099
 - SANS 10400-V: Space Heating
 - Rational design by Gerhard R. Muller ECSA 20090098
 - SANS 10400-W: Fire Installation
 - Rational design by Gerhard R. Muller ECSA 20070099
 - SANS 10400-XA: Energy Efficiency
 - Rational design by Gertie Sher SACAP 4190

C	Local Authority Submission	2024.01.29	AL	Local Authority
B	Local Authority Submission	2021.08.27	NV	Local Authority
A	Local Authority Submission	2021.08.10	NV	Local Authority

ID	Revision Category	Date	Issued by	Issued to
Revisions				

FOR LOCAL AUTHORITY SUBMISSION ONLY



architect  signature

99 buitenkant street
gardens, cape town
8001
[t] +27 21 462 1824
[f] +27 21 462 1629
[e] info@jakupa.co.za
www.jakupa.co.za



client  signature

WPCA

project title
NCG North Pavilion

drawing title
Elevations 2

location
ERF 144264 - NEWLANDS CRICKET GROUND

date
11/11/24

scale drawn checked
As indicated BB GA

project number stage building series dwg no. revision


2321 LA NP EL 201 C

25m Height Restriction




1 LA_SECTION A-A
SCALE: 1 : 100

25m Height Restriction

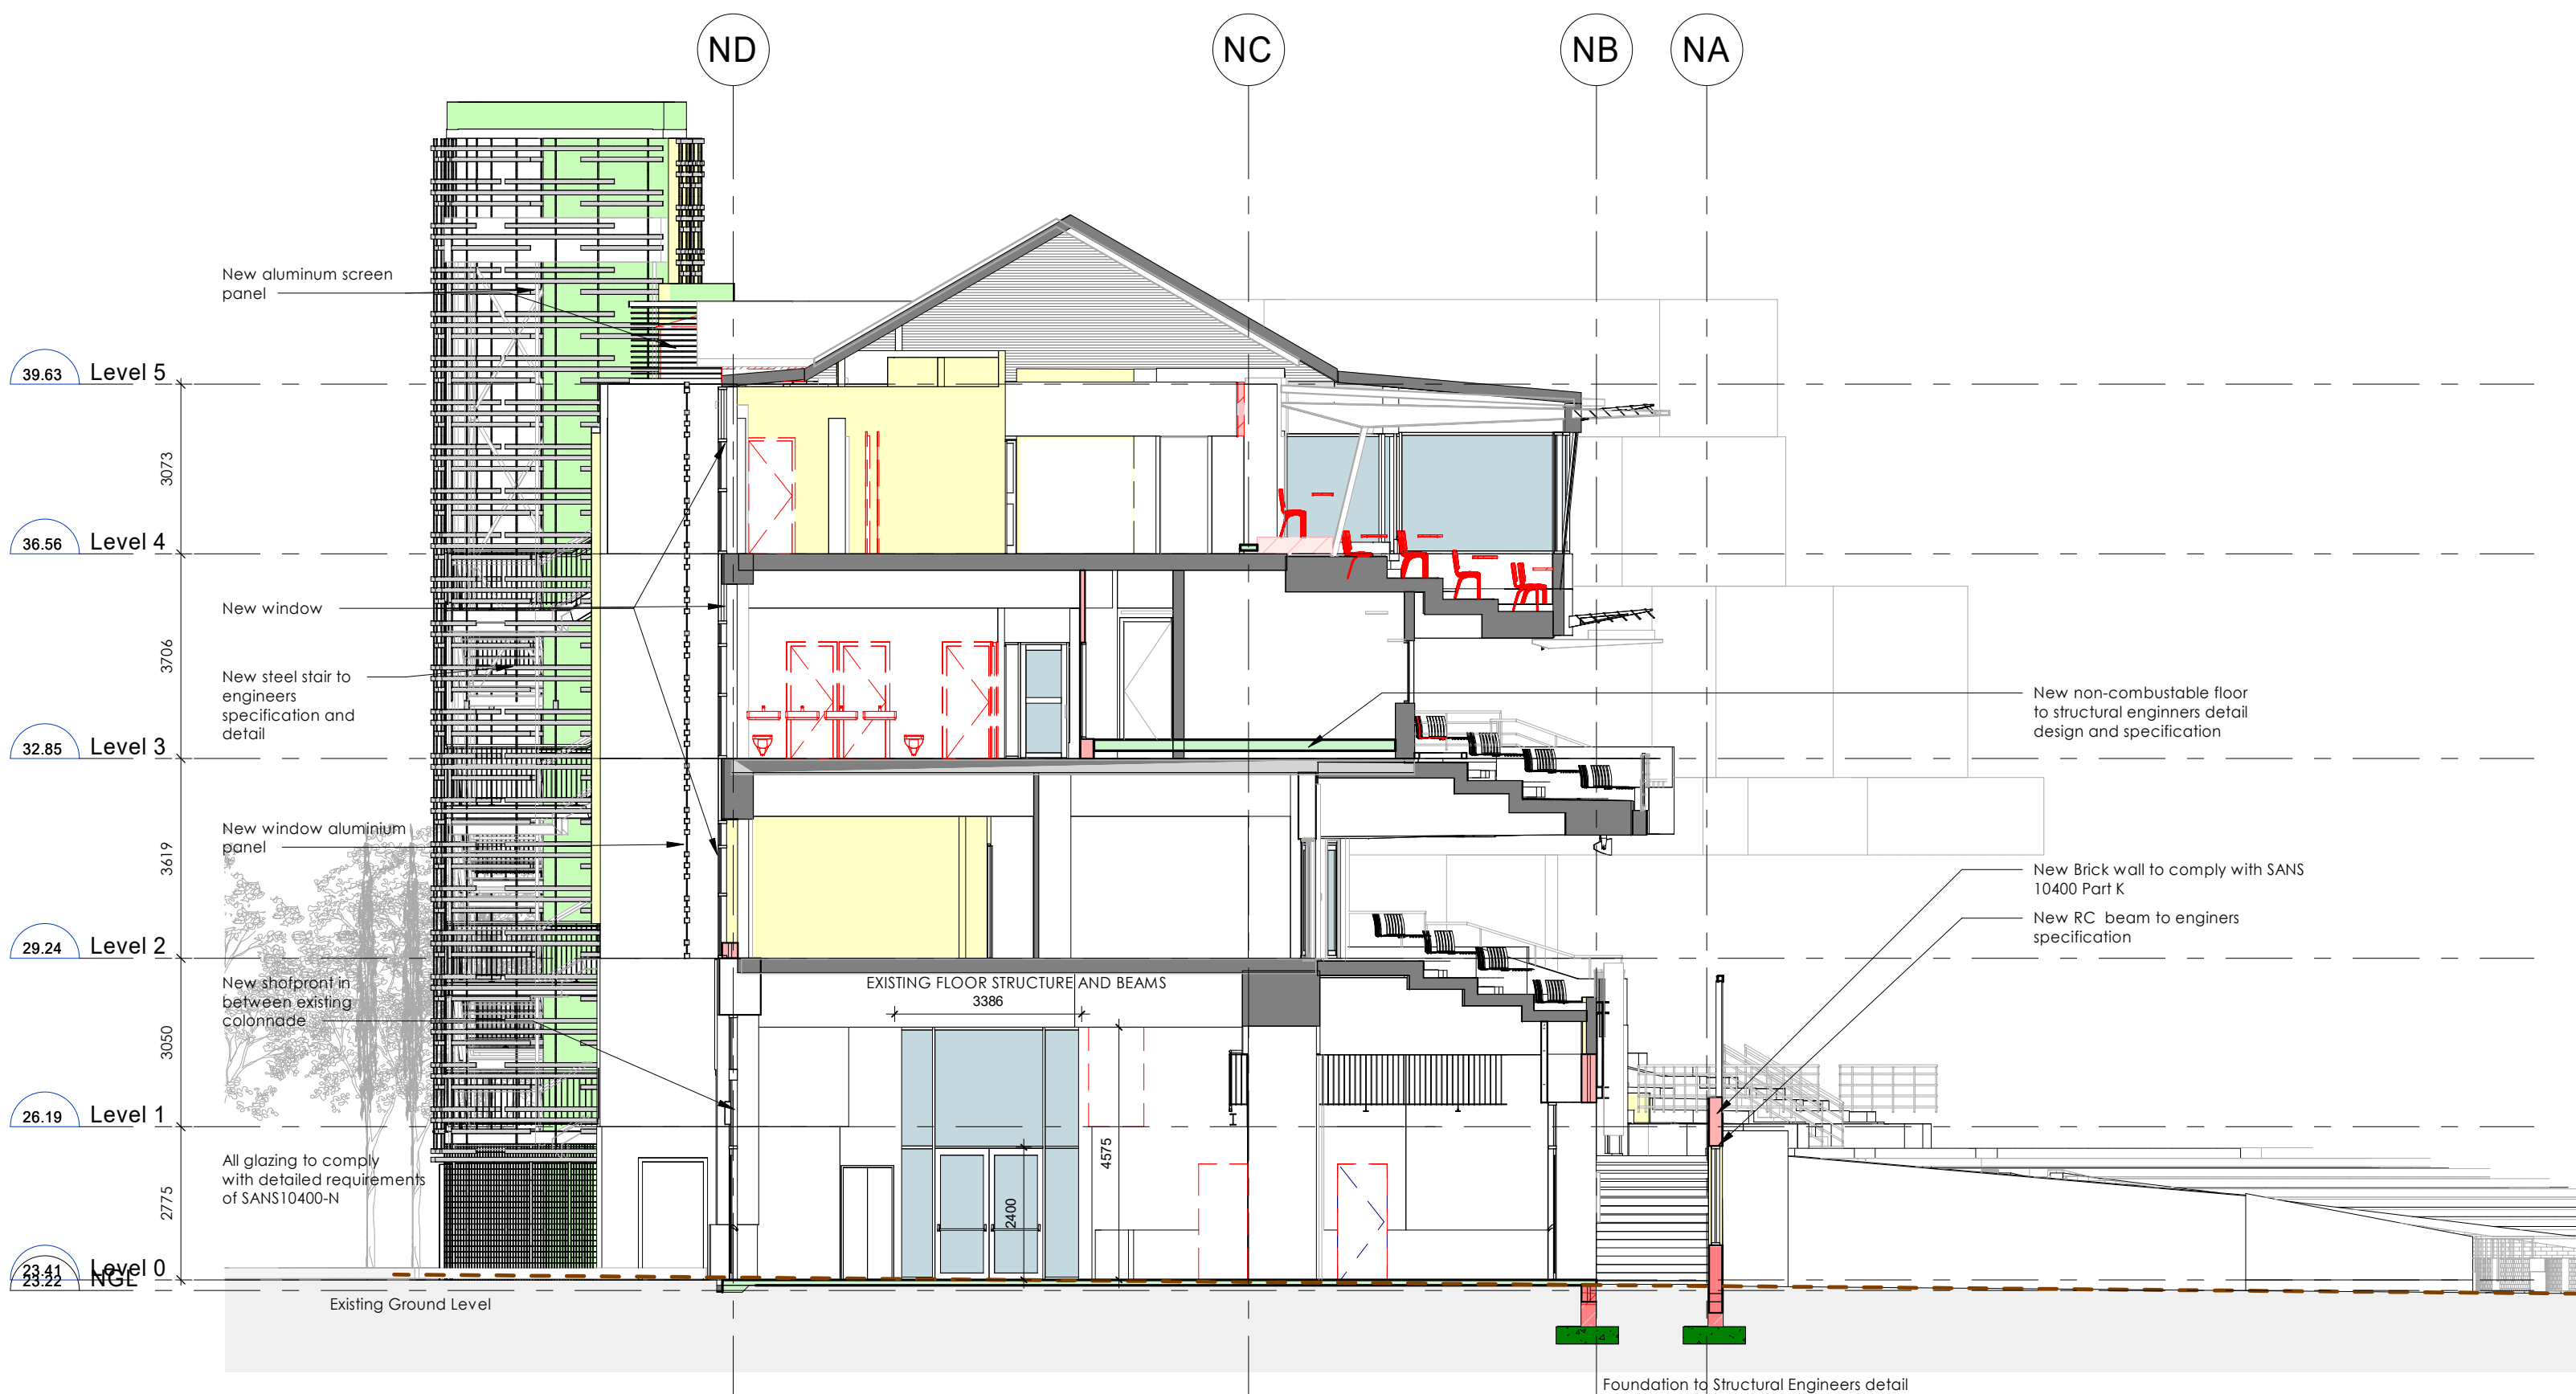

2 LA_SECTION B-B
SCALE: 1 : 100

25m Height Restriction

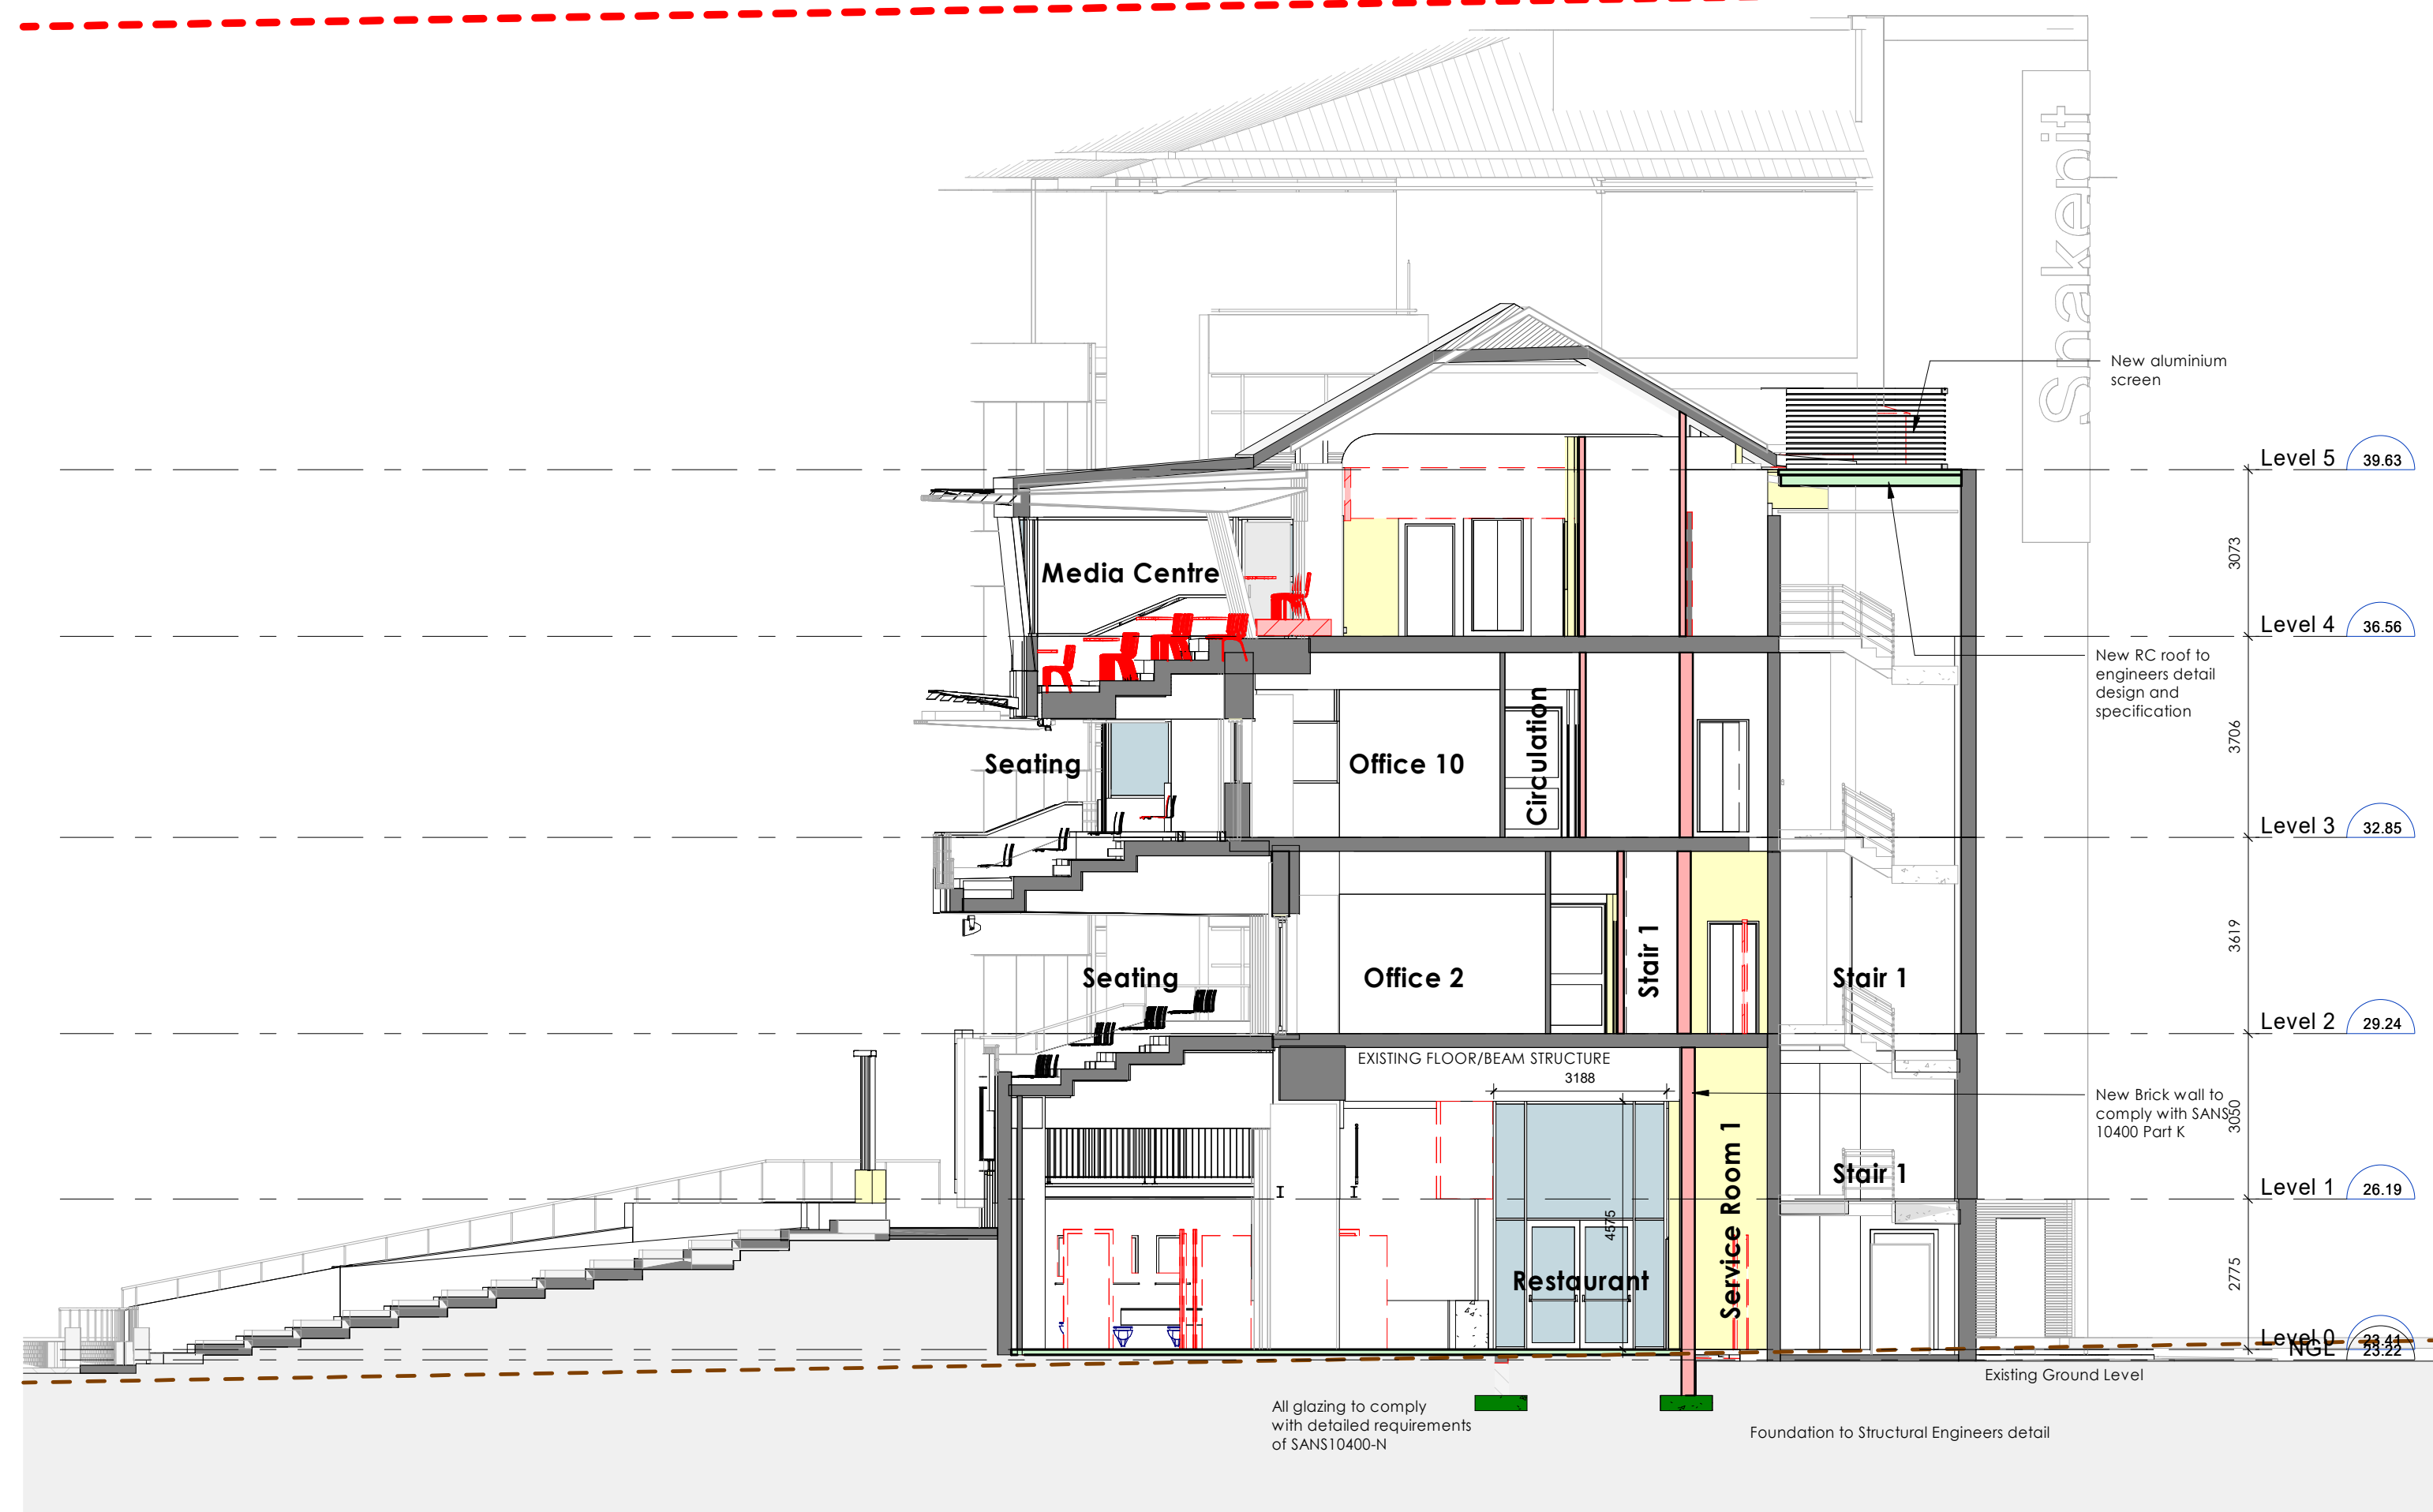

3 LA_SECTION C-C
SCALE: 1 : 100

C	Local Authority Submission	2024.01.29	AL	Local Authority
B	Local Authority Submission	2021.08.27	NV	Local Authority
A	Local Authority Submission	2021.08.10	NV	Local Authority

ID	Revision Category	Date	Issued by	Issued to
Revisions				

FOR LOCAL AUTHORITY SUBMISSION ONLY



architect signature

99 buitenkant street
gardens, cape town
8001
(t) +27 21 462 1824
(f) +27 21 462 1629
(e) info@jakupa.co.za
www.jakupa.co.za



client signature

WPCA

project title
NCG North Pavilion

drawing title
Sections

location
ERF 144264 - NEWLANDS CRICKET
GROUND

date
11/11/24

scale drawn checked
1 : 100 NV GA

project number stage building series dwg no. revision

2321 LA NP SE 300 C