




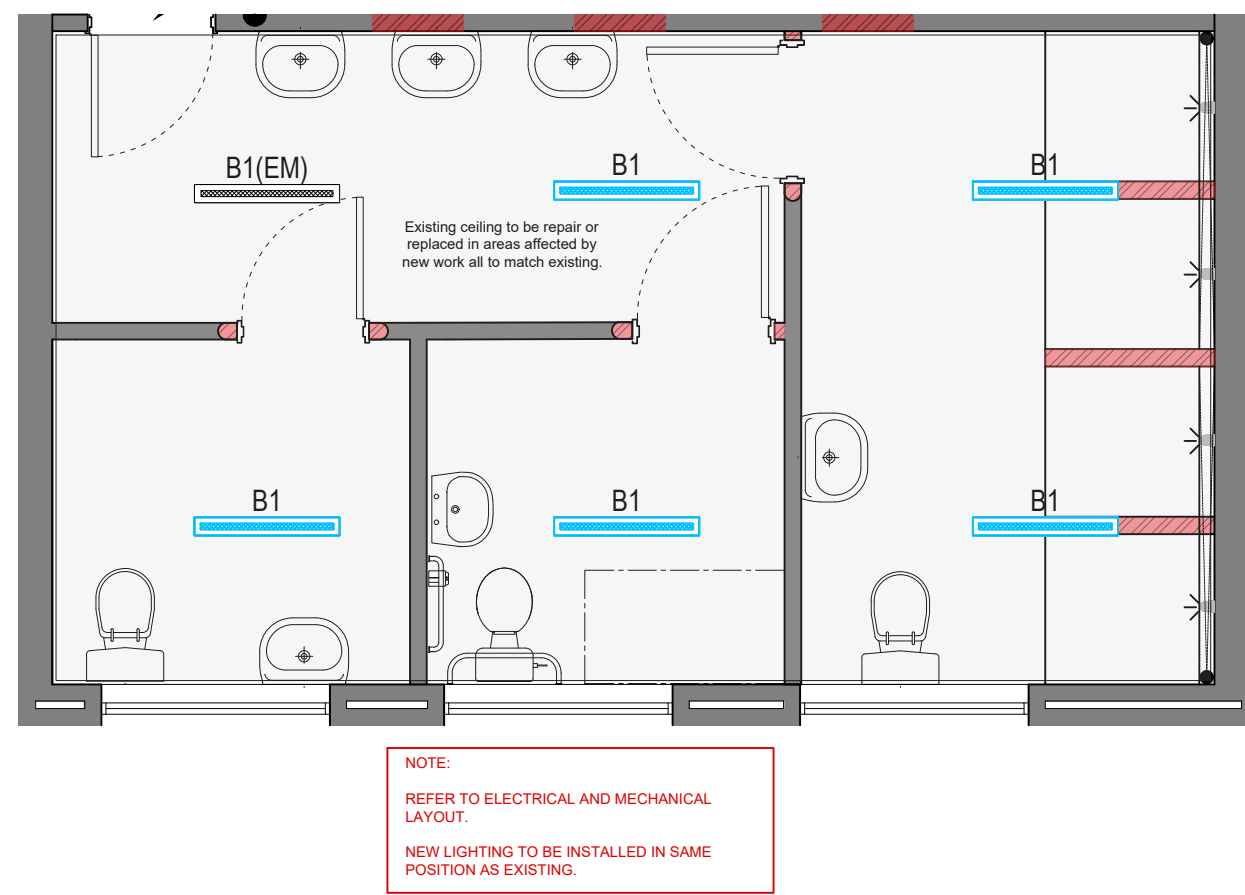


REFLECTED CEILING LAYOUT

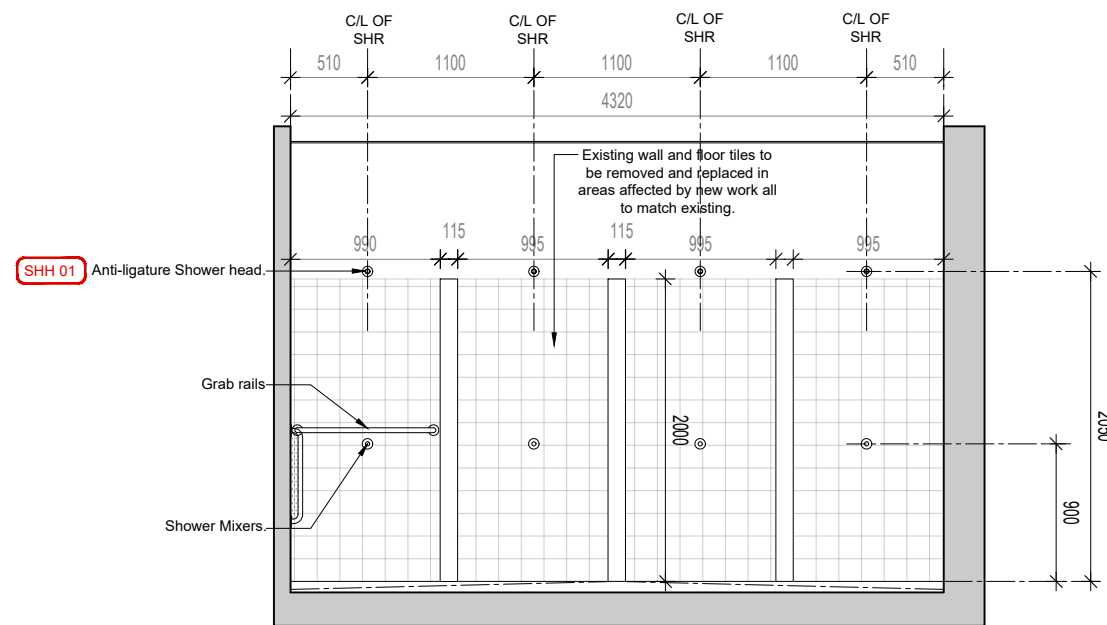

ELEVATION 2
SCALE:1:50

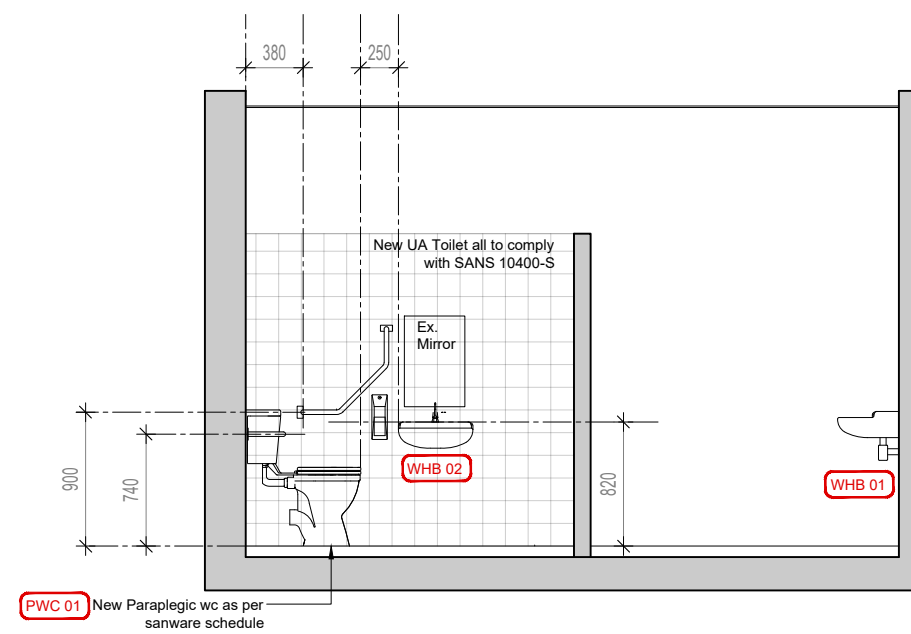



ELEVATION 4
SCALE:1:50

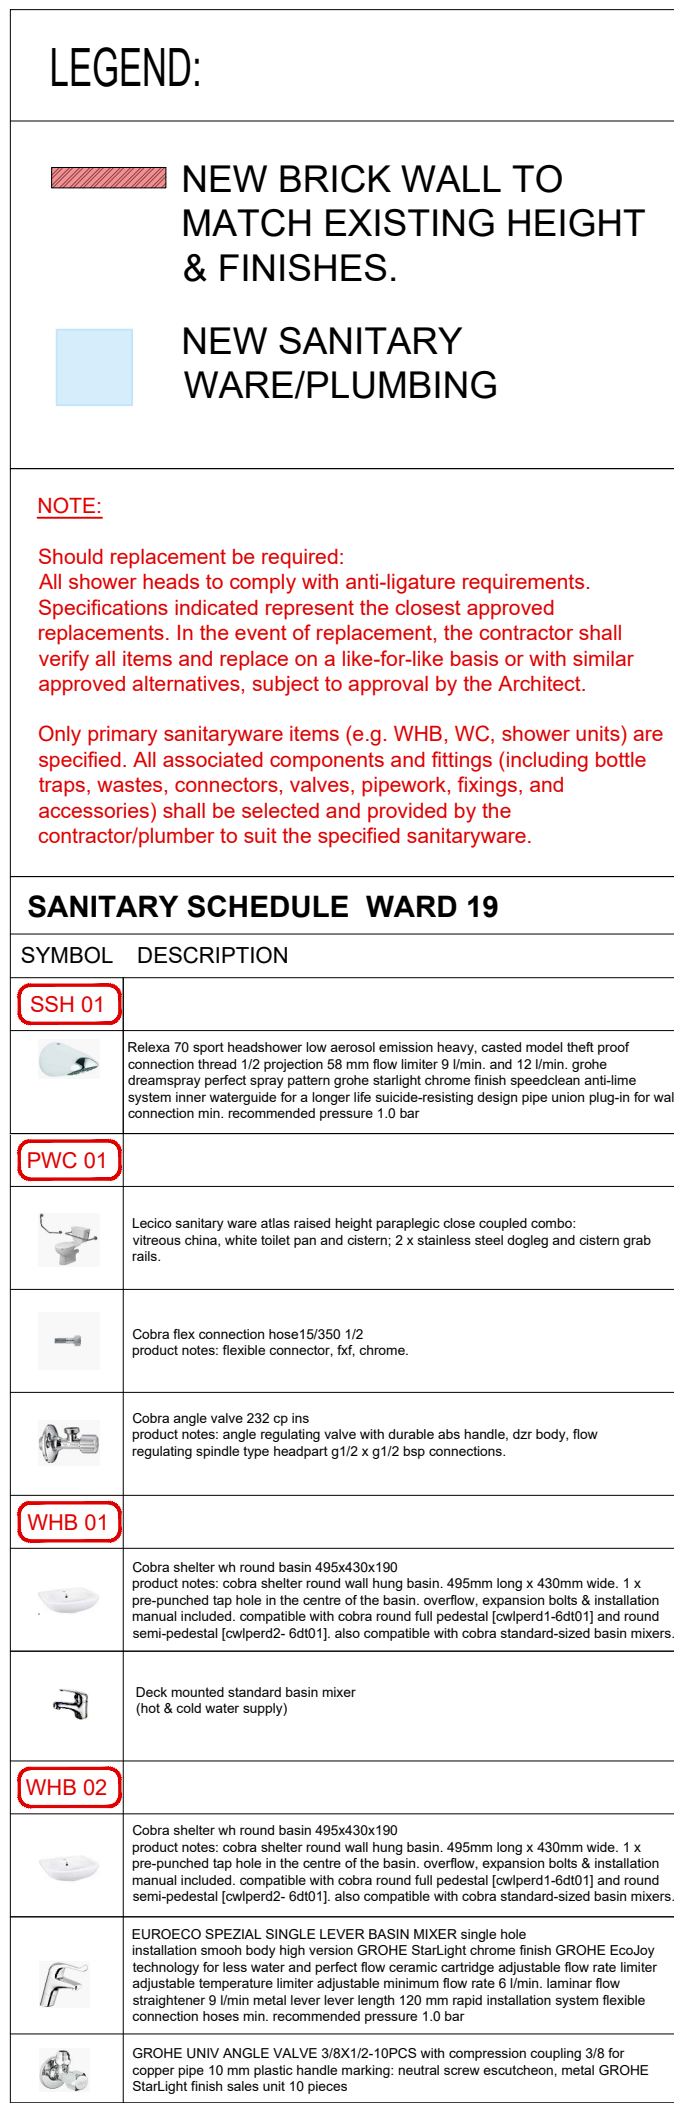

LIGHTING LEGEND

SYMBOL	DESCRIPTION
	DISTRIBUTION BOARD
	SURFACE LED LIGHT 34W DIMMABLE
	SURFACE LED LIGHT 34W DIMMABLE - WITH 1HR BATTERY BACK UP
	RECESSED VANDAL RESISTANT LIGHT FITTING 24W - WITH INTEGRATED NIGHT LIGHT
	RECESSED VANDAL RESISTANT LIGHT FITTING 24W - WITH 1HR BATTERY BACK UP
	VAPOUR PROOF LED LIGHT 34W
	VAPOUR PROOF LED LIGHT 34W - WITH 1HR BATTERY BACK UP
	LED BATTEN LIGHT FITTING 34W
	LED DOWNLIGHT 12W
	LED DOWNLIGHT 12W - WITH 1HR BATTERY BACK UP
	VANDAL RESISTENT BULKHEAD 15W LED (IP65)
	VANDAL RESISTENT BULKHEAD 15W LED (IP65) - WITH 1HR BATTERY BACK UP
	EXTERNAL BULKHEAD LED (IP65) @1200mm AFFL. OR RETAIN EXISTING HEIGHT OF EXISTING FITTING
	EXTERNAL BULKHEAD LED (IP65) @1200mm AFFL. OR RETAIN EXISTING HEIGHT OF EXISTING FITTING - WITH 1HR BATTERY BACK UP
	RECESSED 600x600mm LED PANEL
	LIGHT SWITCH PANEL
	1 LEVER SWITCH @1200mm AFFL
	2 LEVER SWITCH @1200mm AFFL

[illegible]

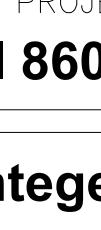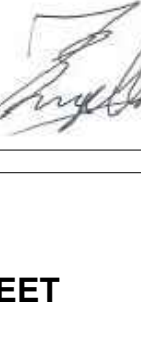	Western Cape Government FOR YOU	Infrastructure
PGWC PROJECT NO. HCI 860041		
Lentegeur Hospital Renovation & Refurbishment		
CAPE TOWN		
		
 BRINK STOKES MKHIZE architects + landscape architects 216 Main Road, PO Box 2702, Somerset West, 7130 T 021 851 6561 F 321 851 6560 W www.bsrmdesign.com 2020 ARCHITECTS		
ARCHITECT: Francois Engelbrecht SACAP: PrArch 20565		
DRAWING TITLE WARD 19 28 BATHROOMS ROOM DATA SHEET		

SCALE: 1:100	DATE: JUNE 2026	AUTHOR: PS
PROJECT NO: 2K017	DWG NO: 19-301	REV: B