



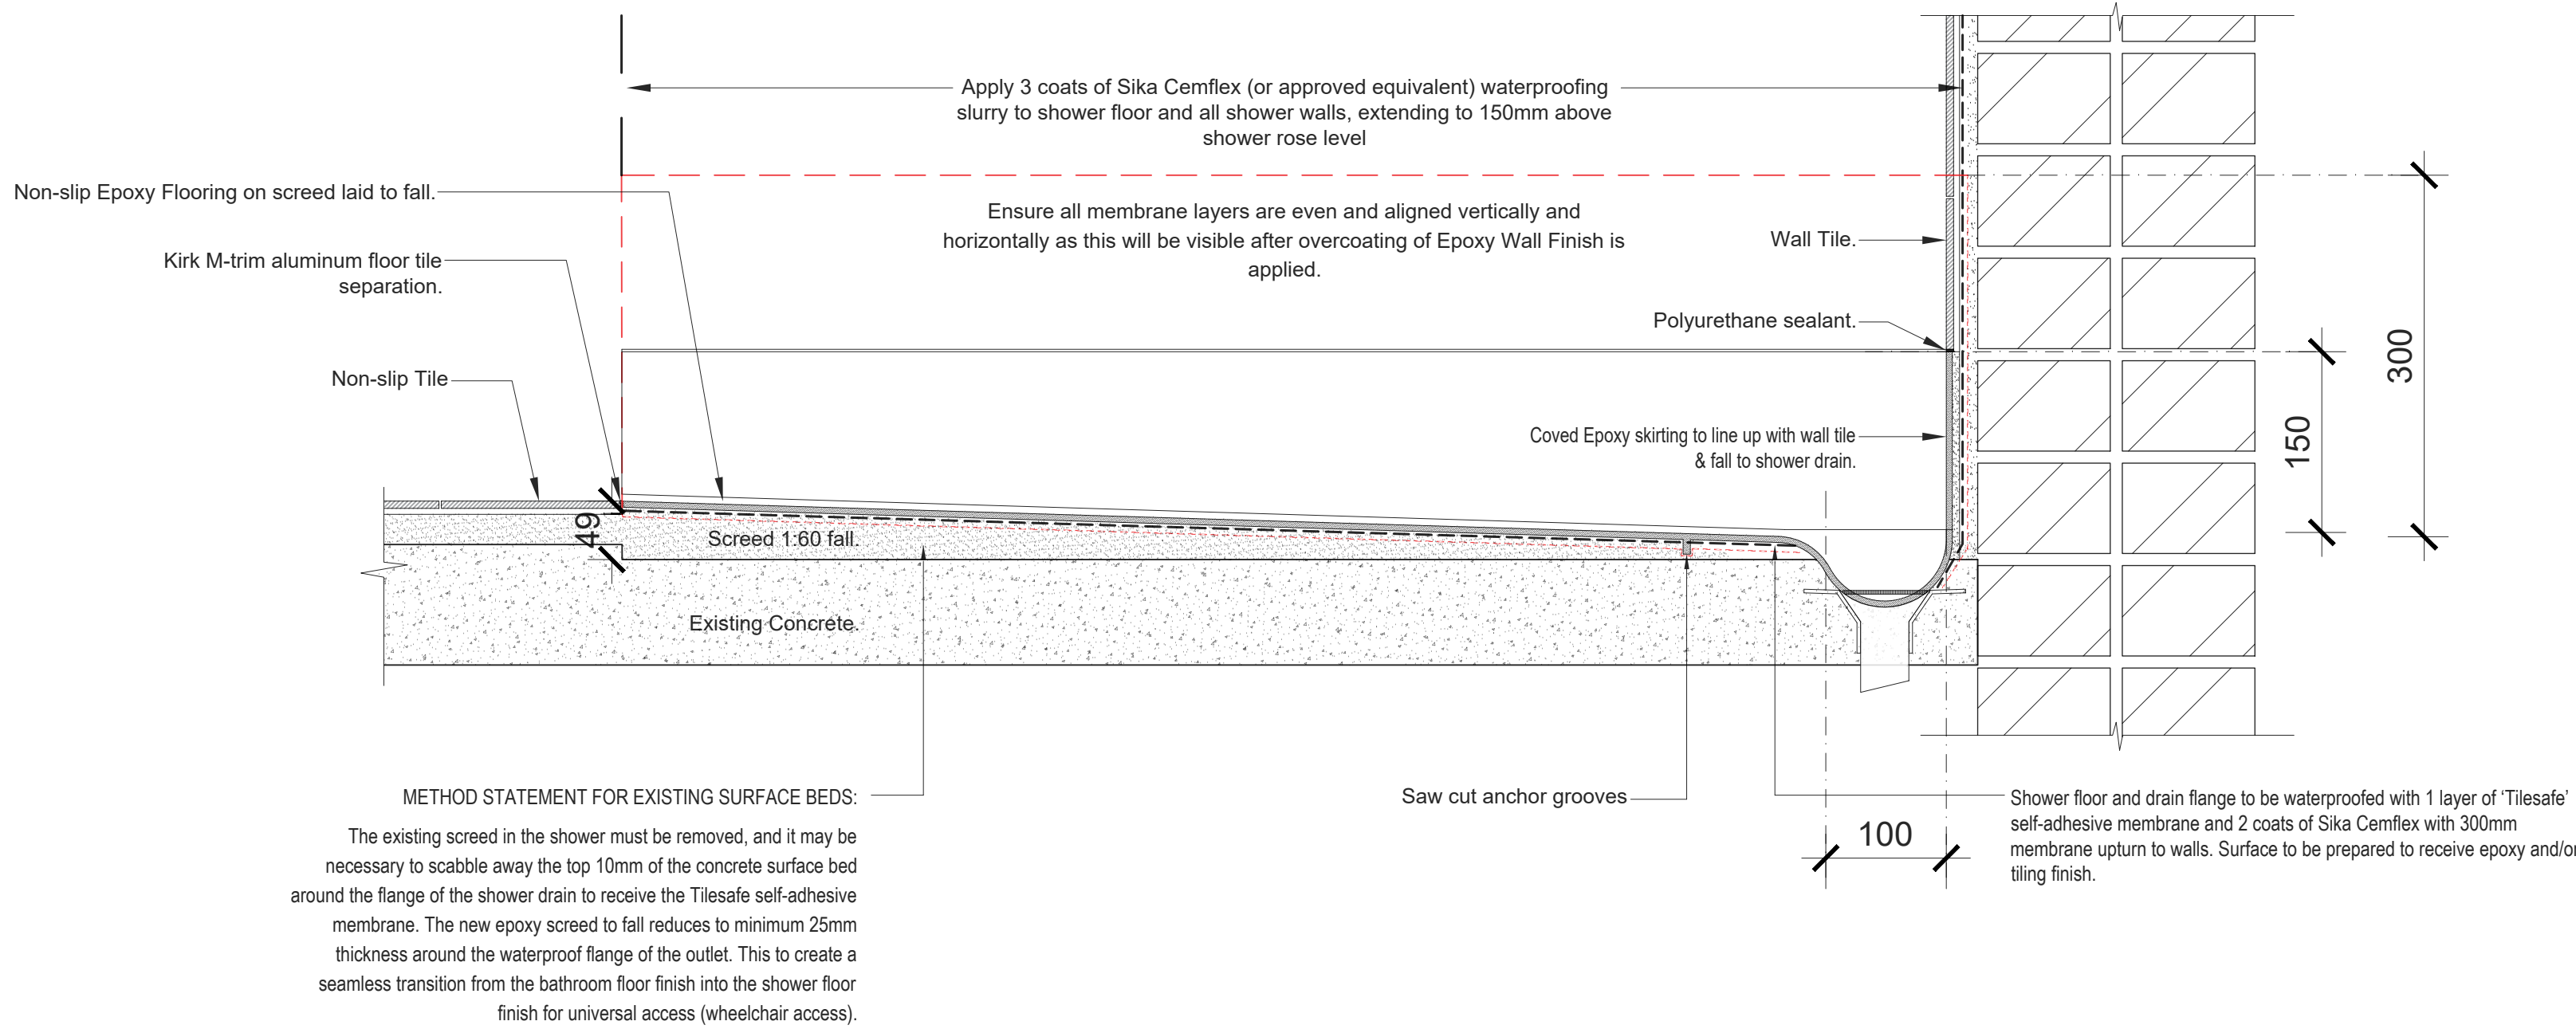


DETAIL SECTION A-A

SCALE:1:5

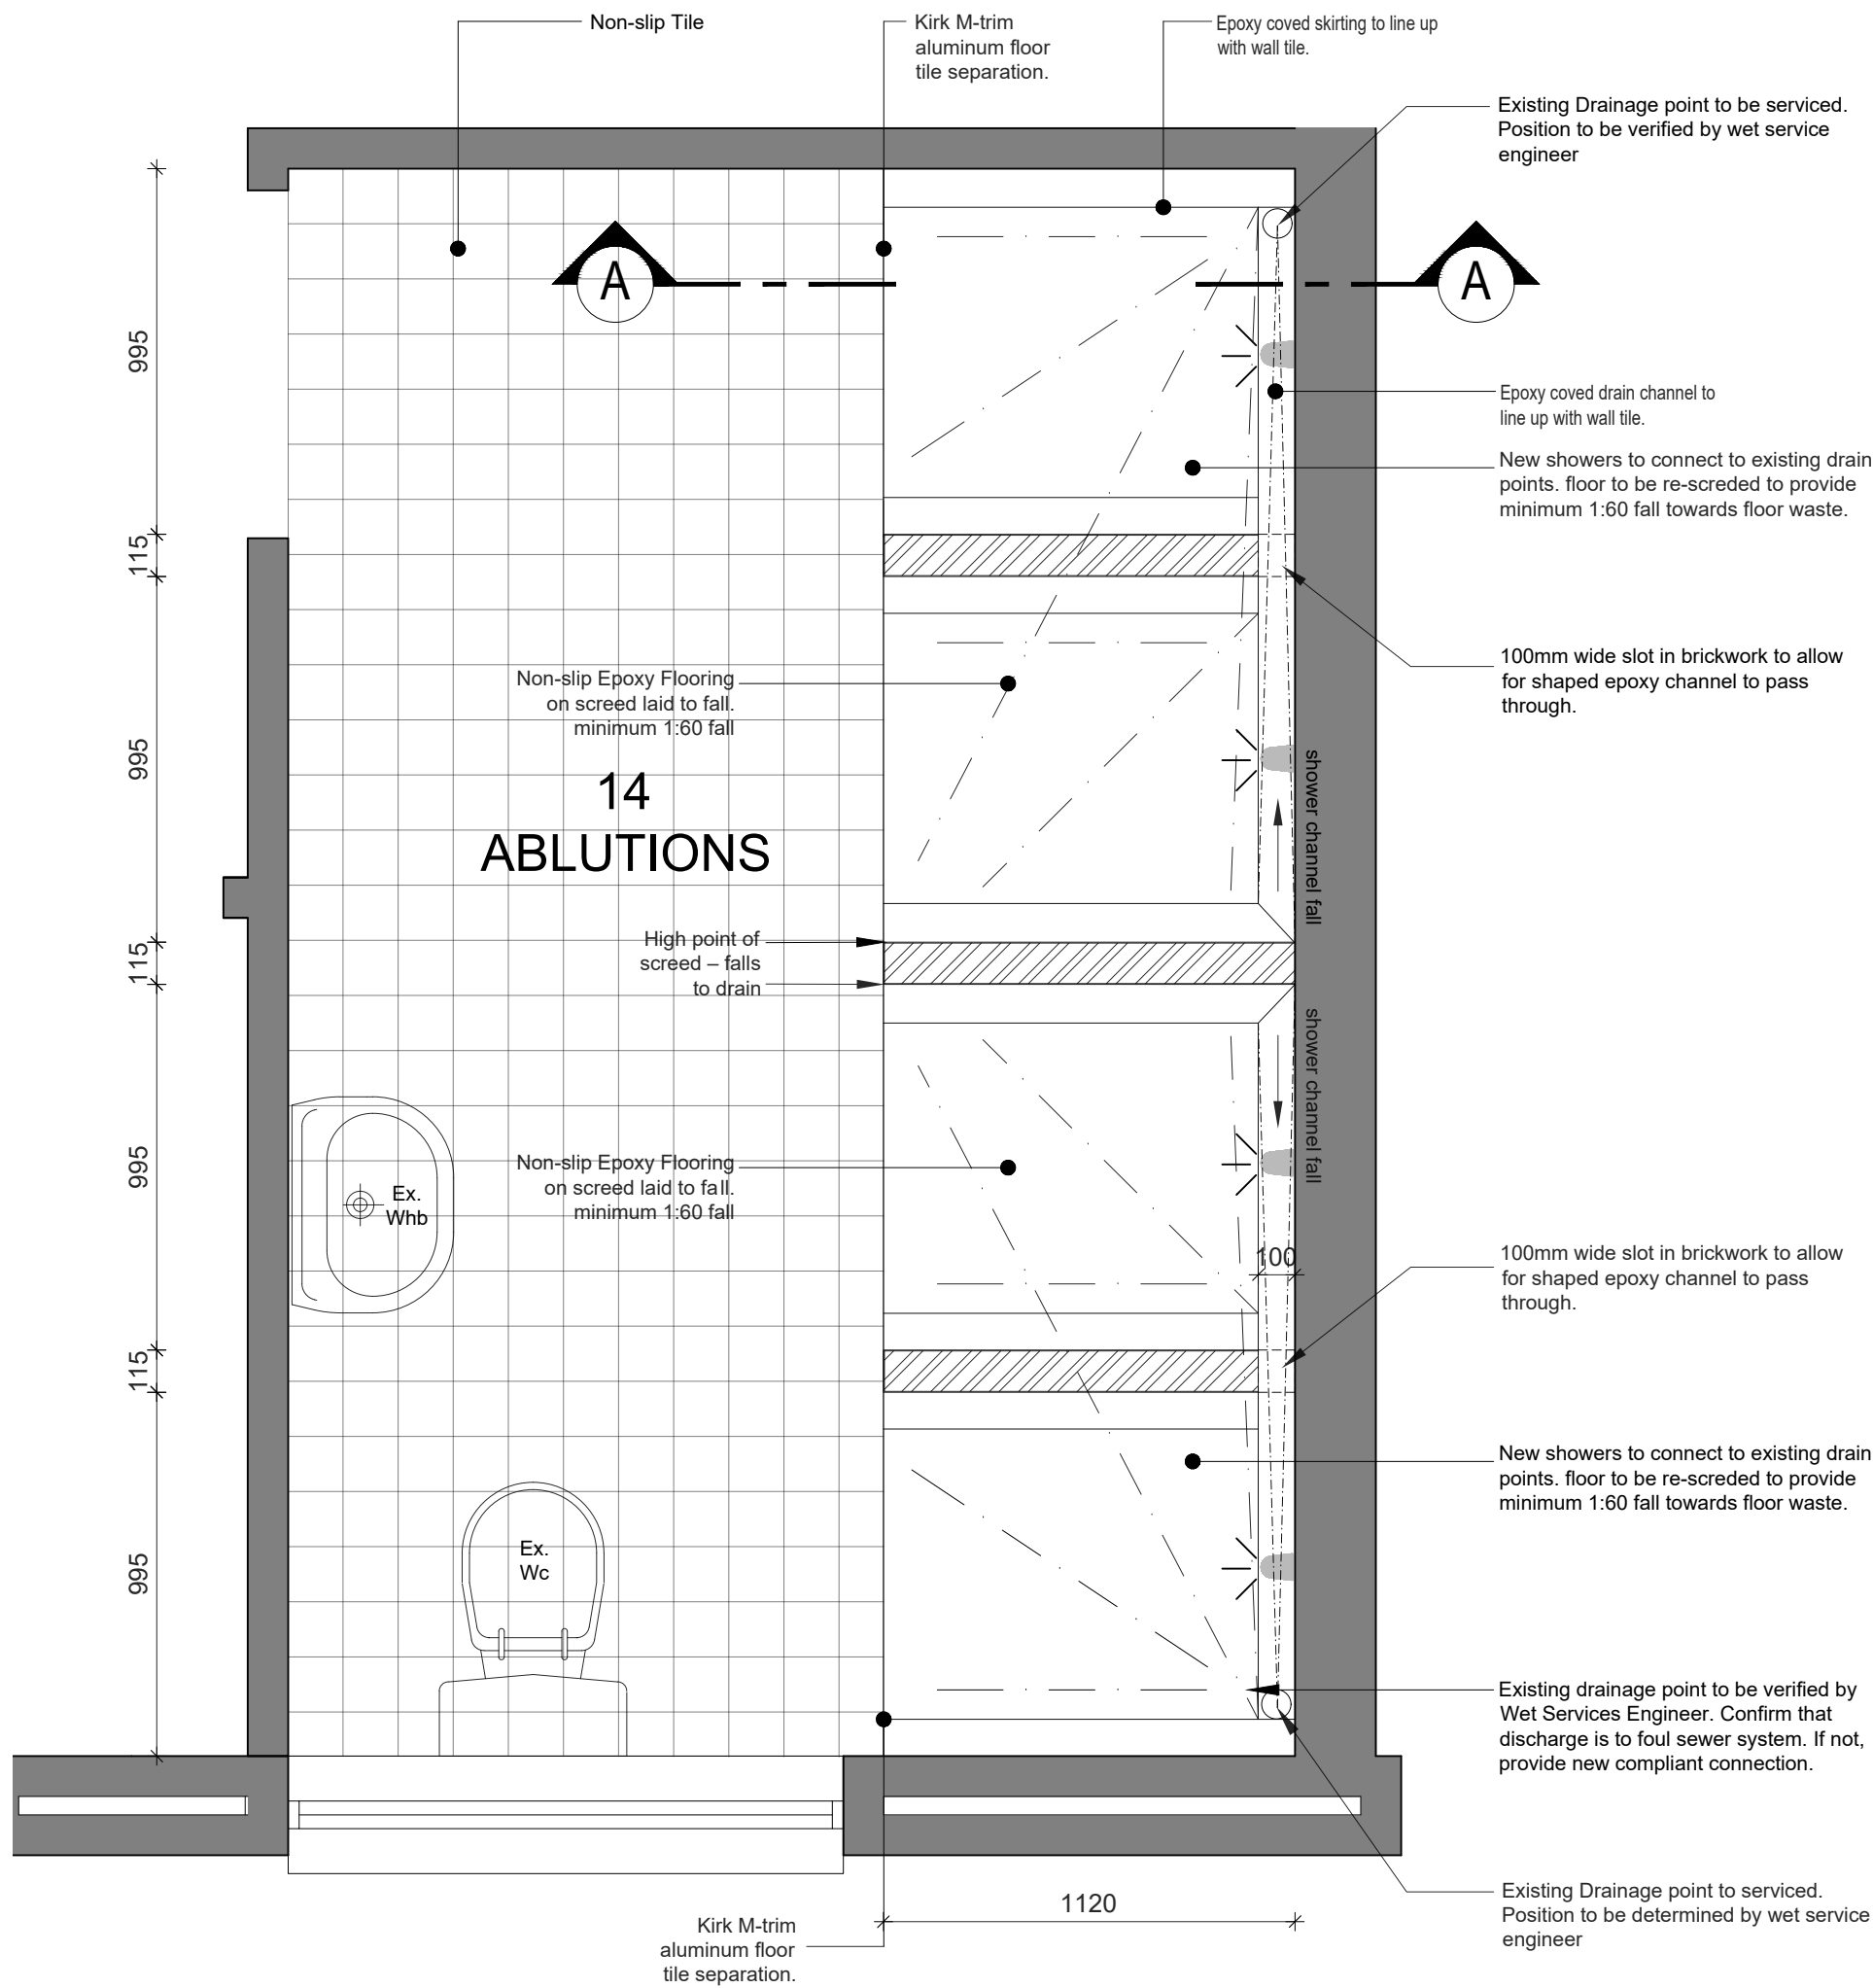

14 ABLUTIONS WARD 19 PLAN

SCALE:1:20

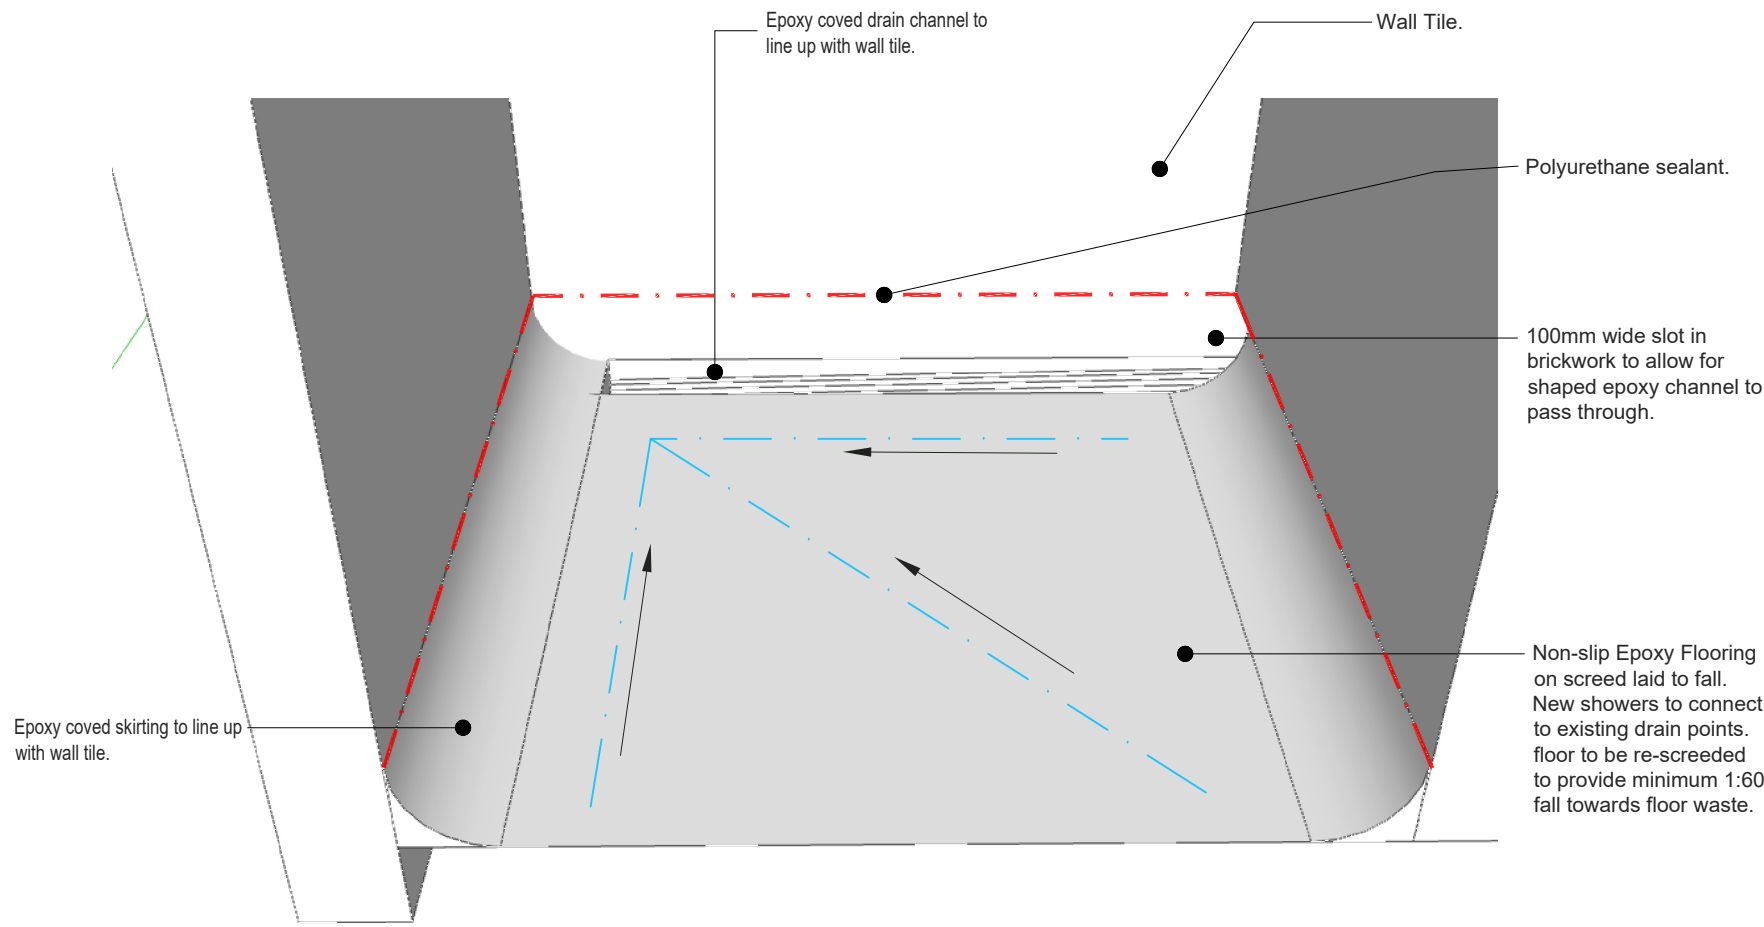


14 ABLUTIONS WARD 19 PLAN PERSPECTIVE

SCALE: N.T.S

NOTE:

EXISTING SLAB THICKNESS AND CONDITION TO BE VERIFIED ON SITE PRIOR TO INSTALLATION

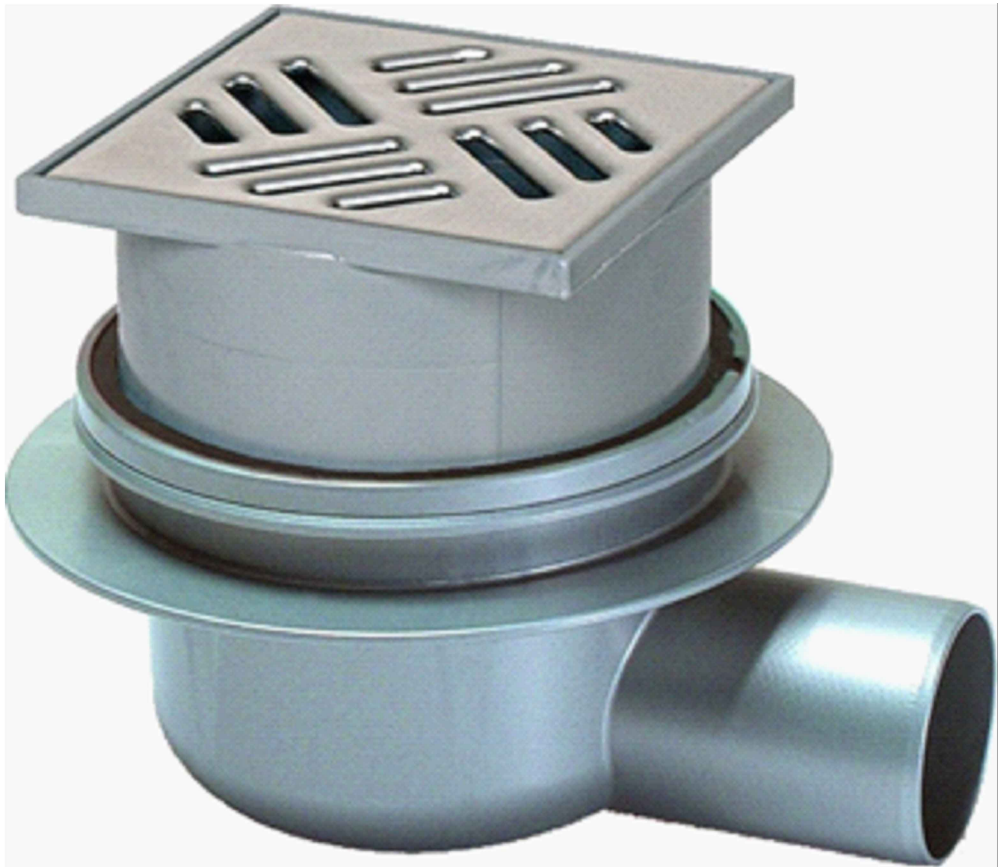

NEW SHOWER TRAP TO BE INSTALLED:

Euro-drain-kessel-50mm-classic-floor-drain-art-nr-40-150-20/PLID72867140

The 50mm outlet pipe to fall must be chased into the existing surface bed, subject to structural engineer's approval and repair method.

Should the proposed system be deemed unsuitable due to existing slab thickness or site conditions, an alternative drainage solution shall be proposed.

This drawing is the copyright of BMS Architects do not scale and refer to figured dimensions only. All levels and dimensions must be checked on site prior to setting out and or manufacture. Any discrepancies must be reported to Architects immediately.

REV.	DESCRIPTION	DATE	BY
A	Issue for Tender	11/03/2026	RC
B	Floor drain revised	10/04/2026	RC
C	REVISED AS PER COMMENTS RECEIVED ON STAGE 4 REPORT	18/06/2026	PS



PCWC PROJECT NO.
HCI 860041

**LENTEGEUR Transitional Care
Renovation & Refurbishment**

**MITCHELLS PLAIN,
CAPE TOWN**



ARCHITECT:

DRAWING TITLE
**WARD 19
SHOWER WATERPROOFING DETAIL**

SCALE: 1:20/1:5	DATE: APRIL 2026	AUTHOR: PS
PROJECT NO: 2K017	DWG NO: 402	REV: C