






GROUND FLOOR PLAN
SCALE 1:100

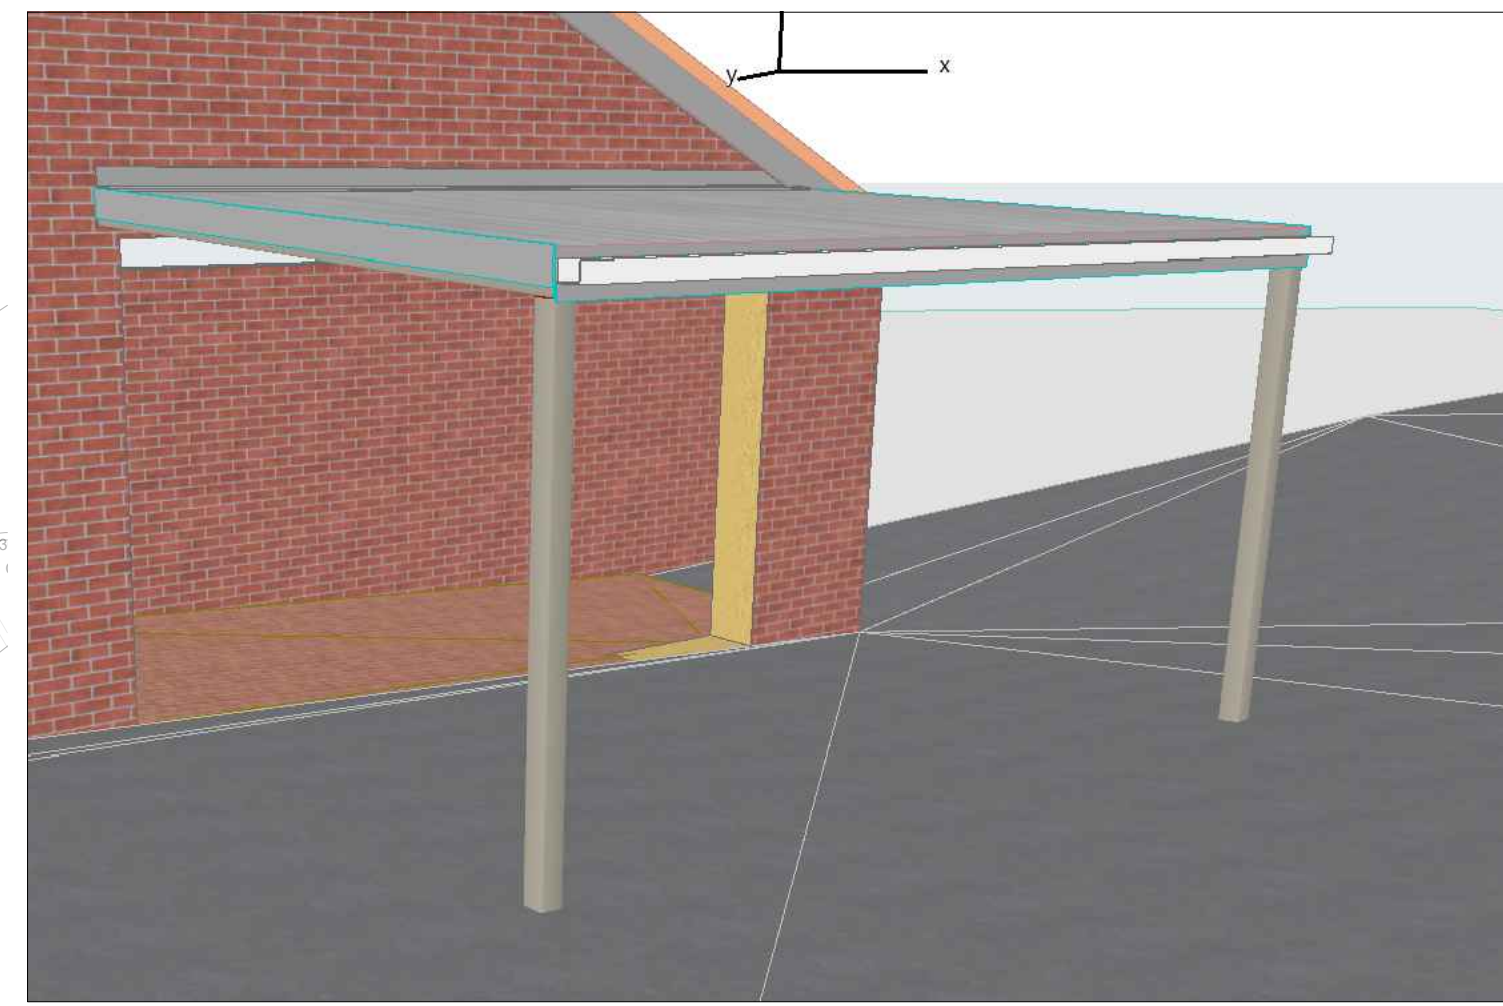

3D
SCALE N.T.S

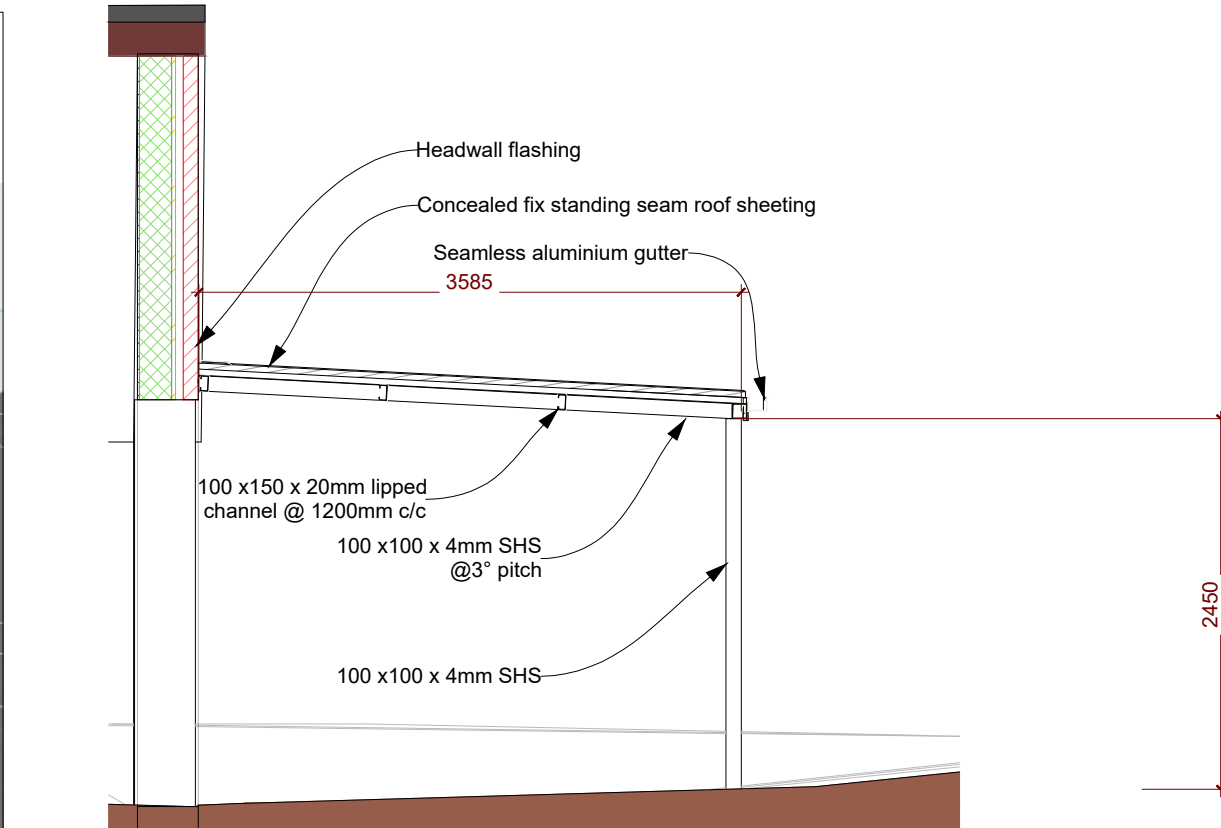


BUILDING SECTION 02
SCALE 1:50

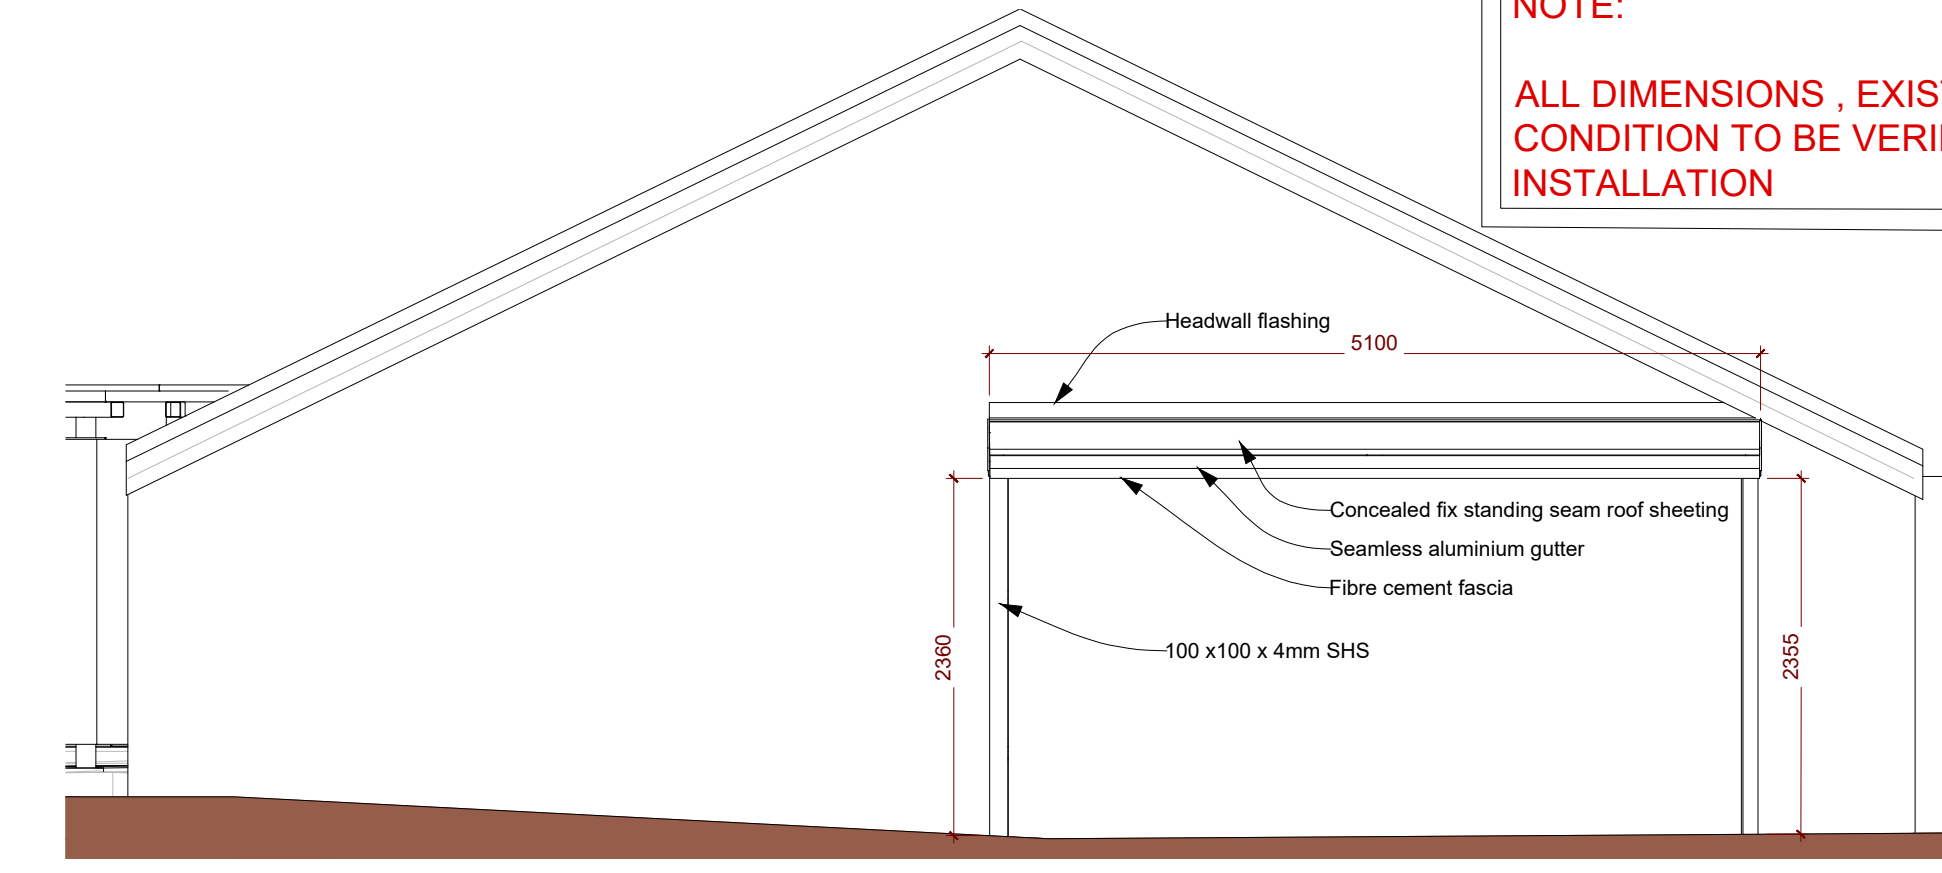


BUILDING ELEVATION
SCALE 1:50


NOTE:
ALL DIMENSIONS, EXISTING SLAB THICKNESS AND
CONDITION TO BE VERIFIED ON SITE PRIOR TO
INSTALLATION

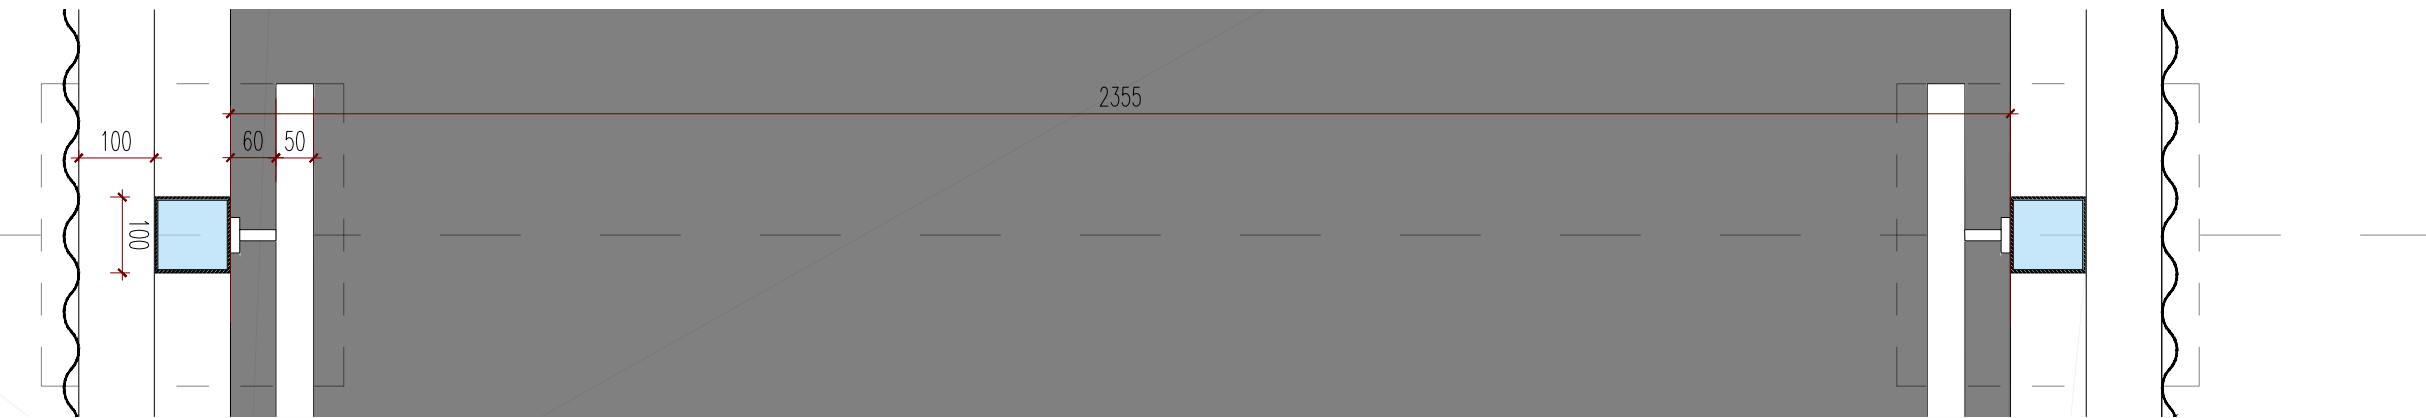


GROUND FLOOR CALL OUT
SCALE 1:10

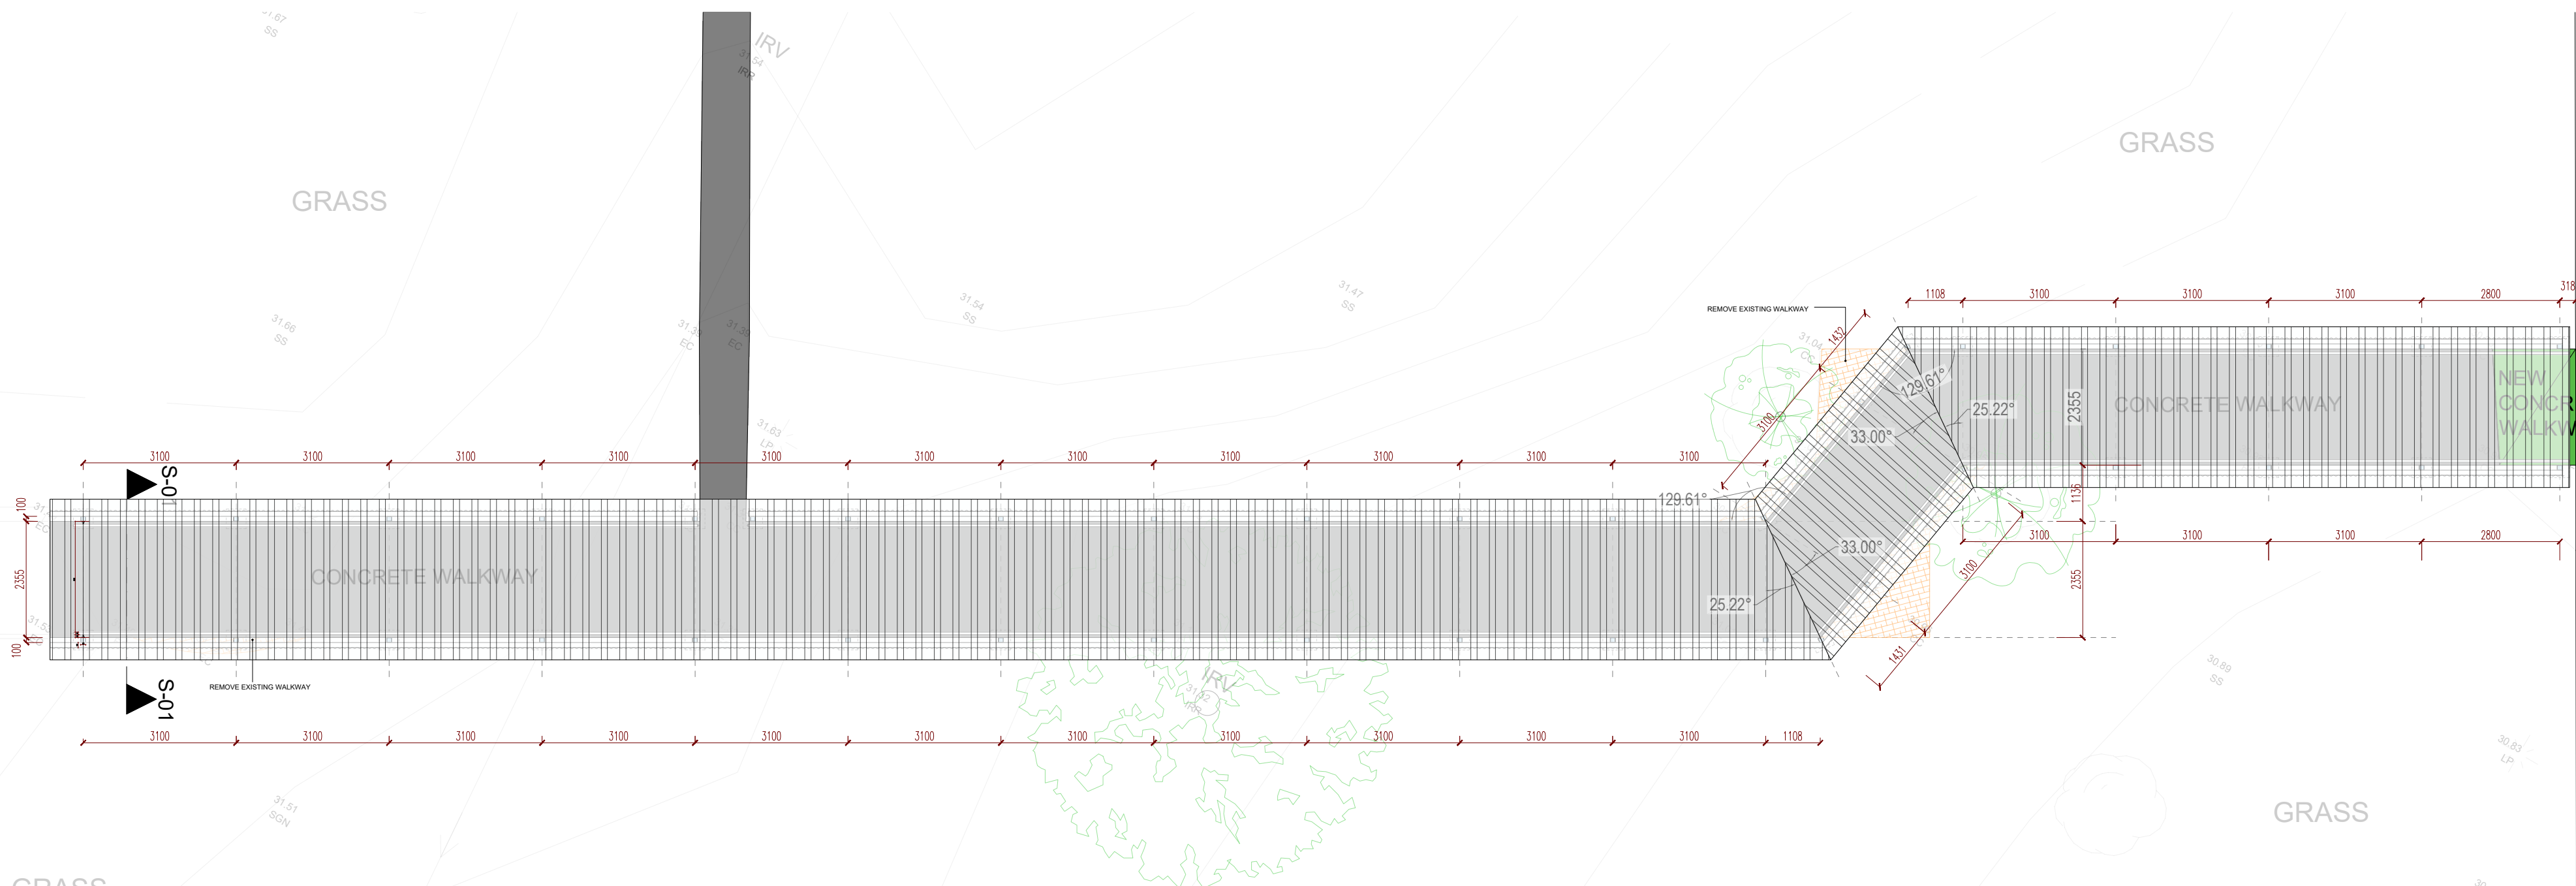


ROOF PLAN
SCALE 1:100

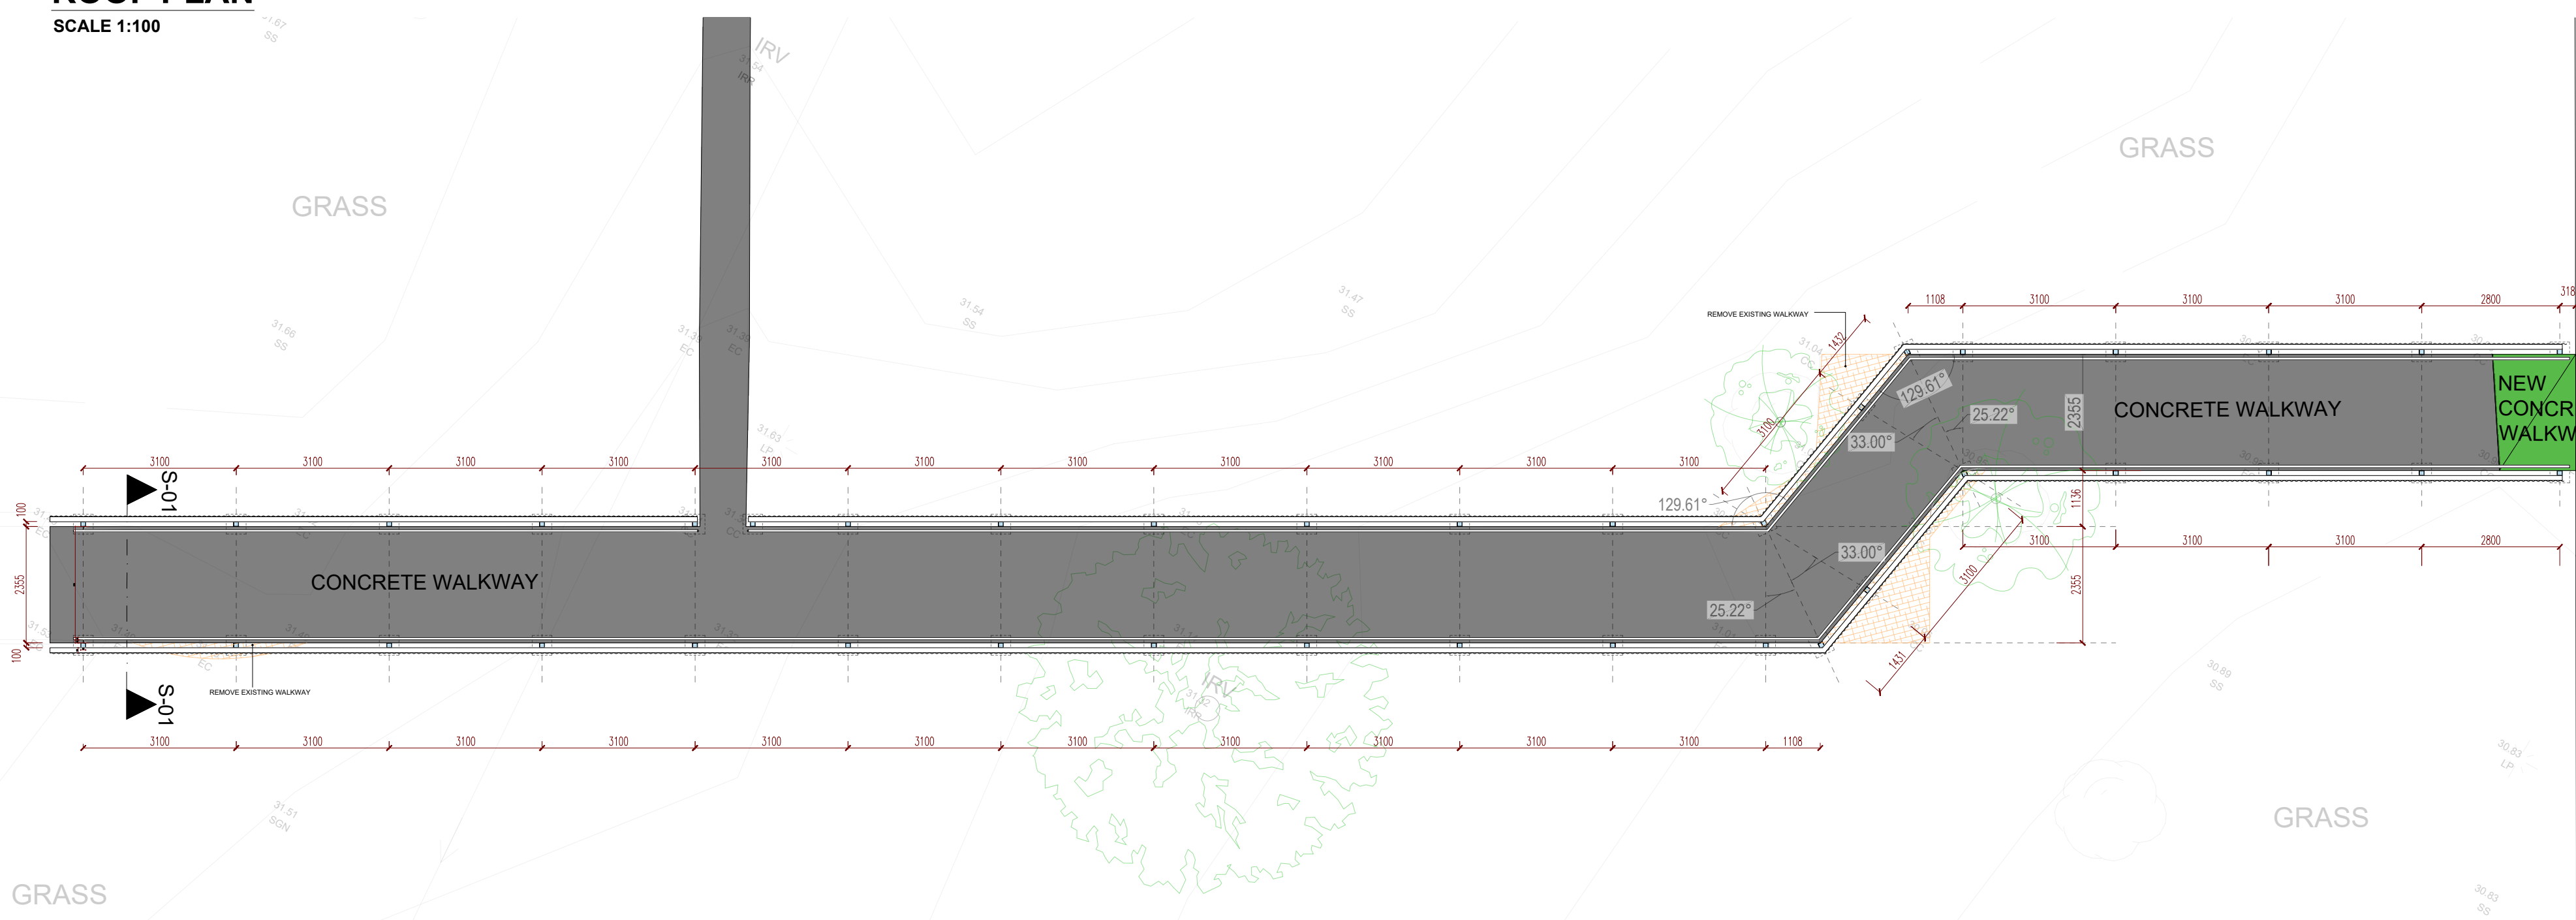

GROUND FLOOR PLAN
SCALE 1:100

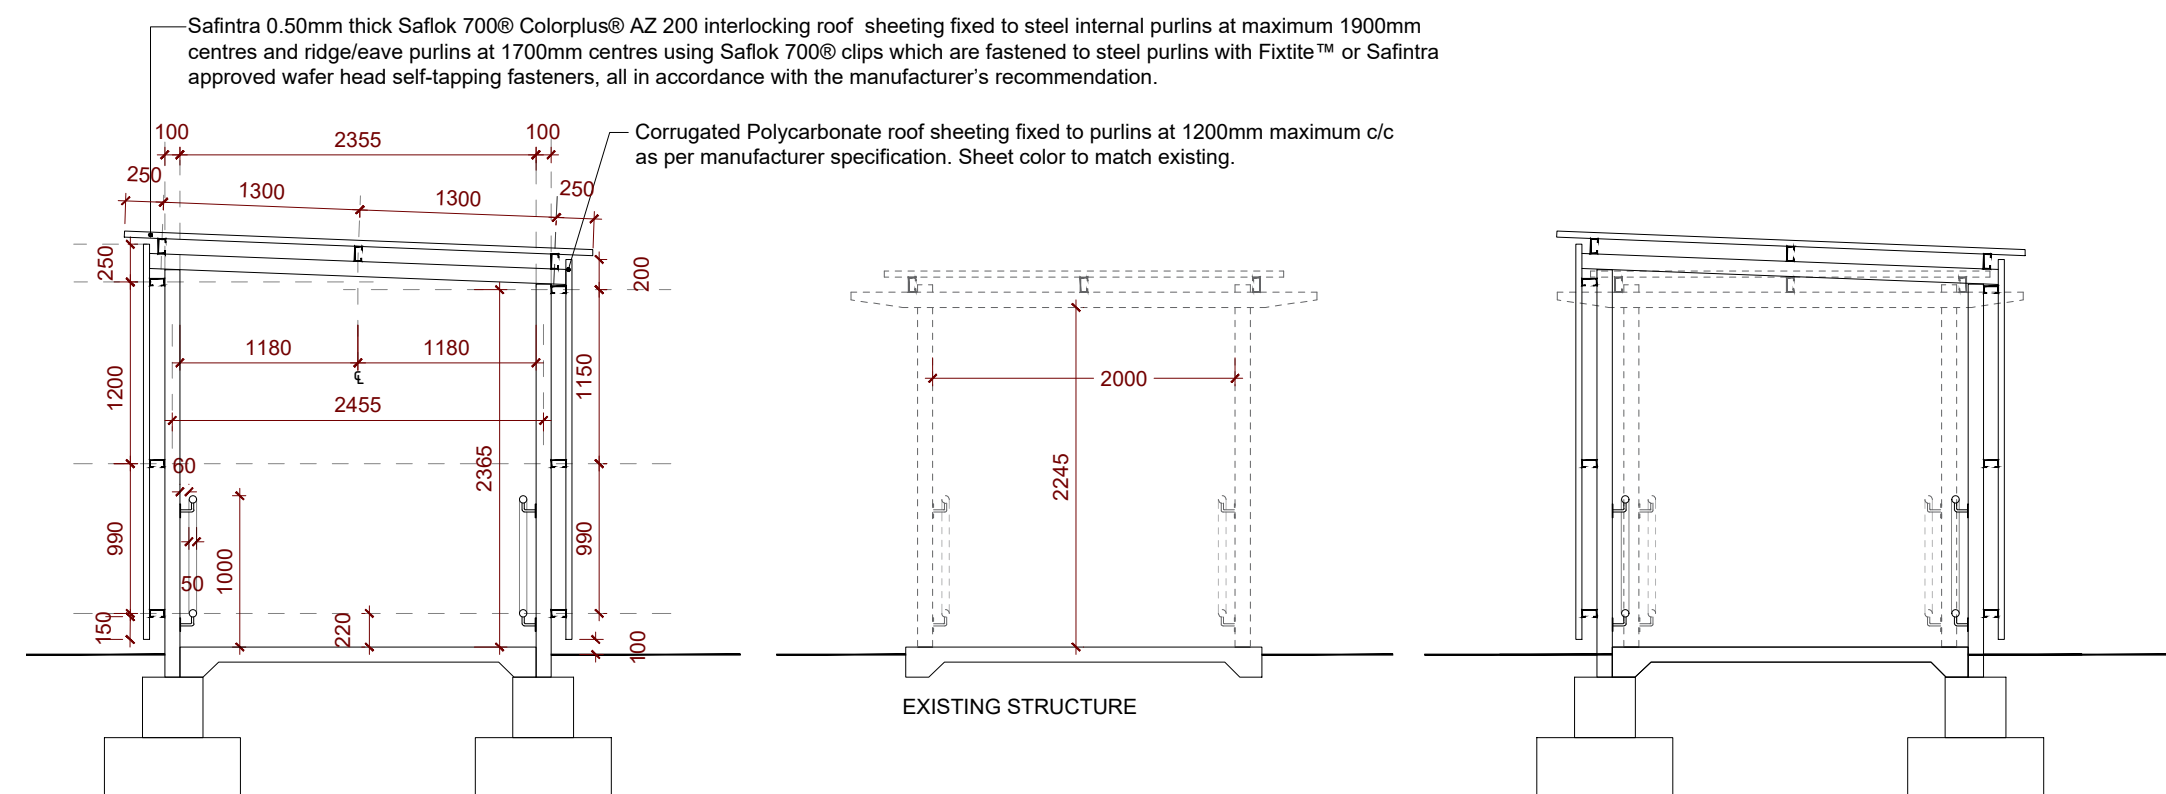

BUILDING SECTION 01
SCALE 1:50

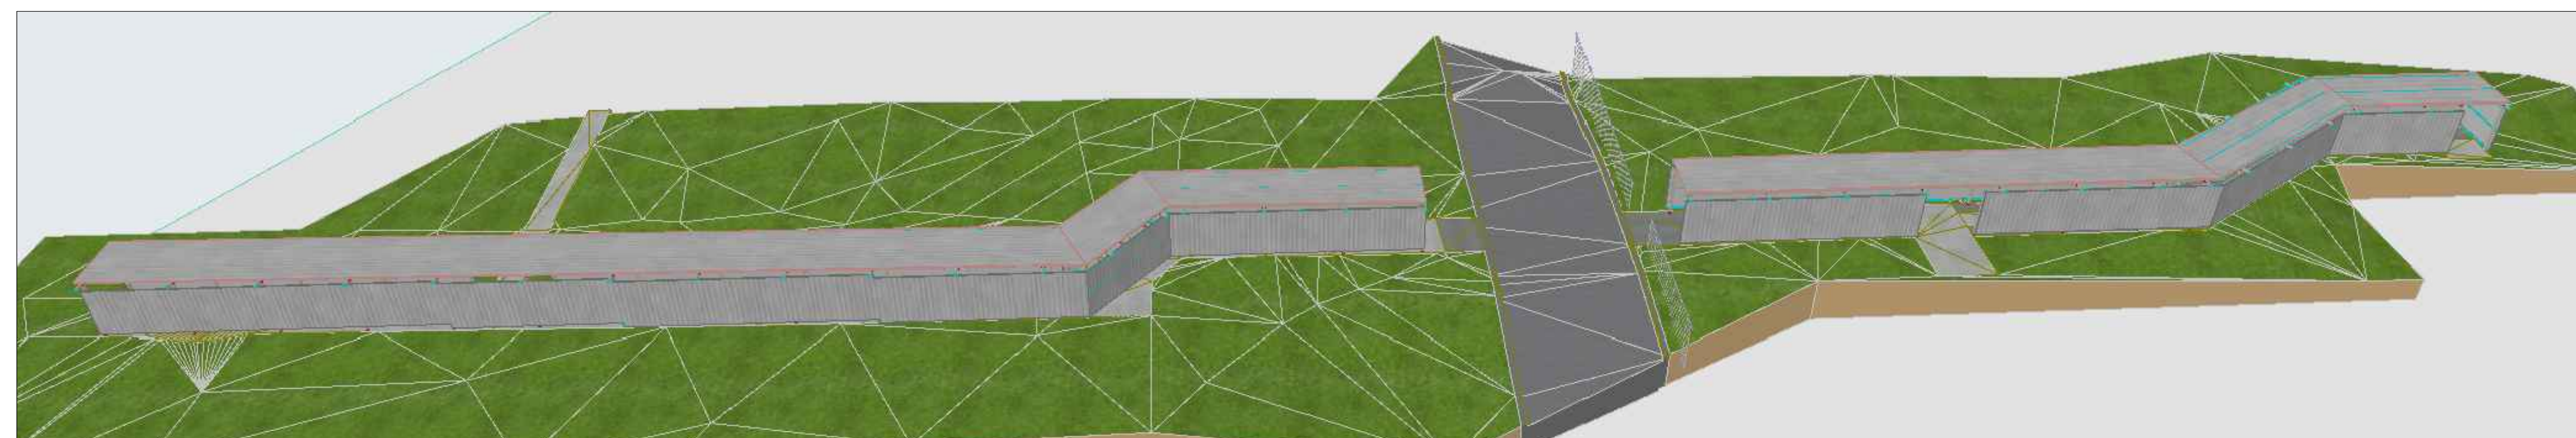

BUILDING 3D
SCALE N.T.S

This drawing is the copyright of BMS Architects do note scale and refer to figured dimensions only. All levels and dimensions must be checked on site prior to setting out and or manufacture. Any discrepancies must be reported to Architects immediately.

REV.	DESCRIPTION	DATE	BY
A	Issue for Tender	19/06/2026	BB



PGWC PROJECT NO.
HCI 860041

**LENTEGEUR Transitional Care
Renovation & Refurbishment**

**MITCHELLS PLAIN,
CAPE TOWN**



ARCHITECT:

DRAWING TITLE
WALKWAY AND CANOPY DETAILS

STAGE 4

SCALE: 1:20/1:5	DATE: JUNE 2026	AUTHOR: BB
PROJECT NO: 2K017	DWG NO: 420	REV: A